




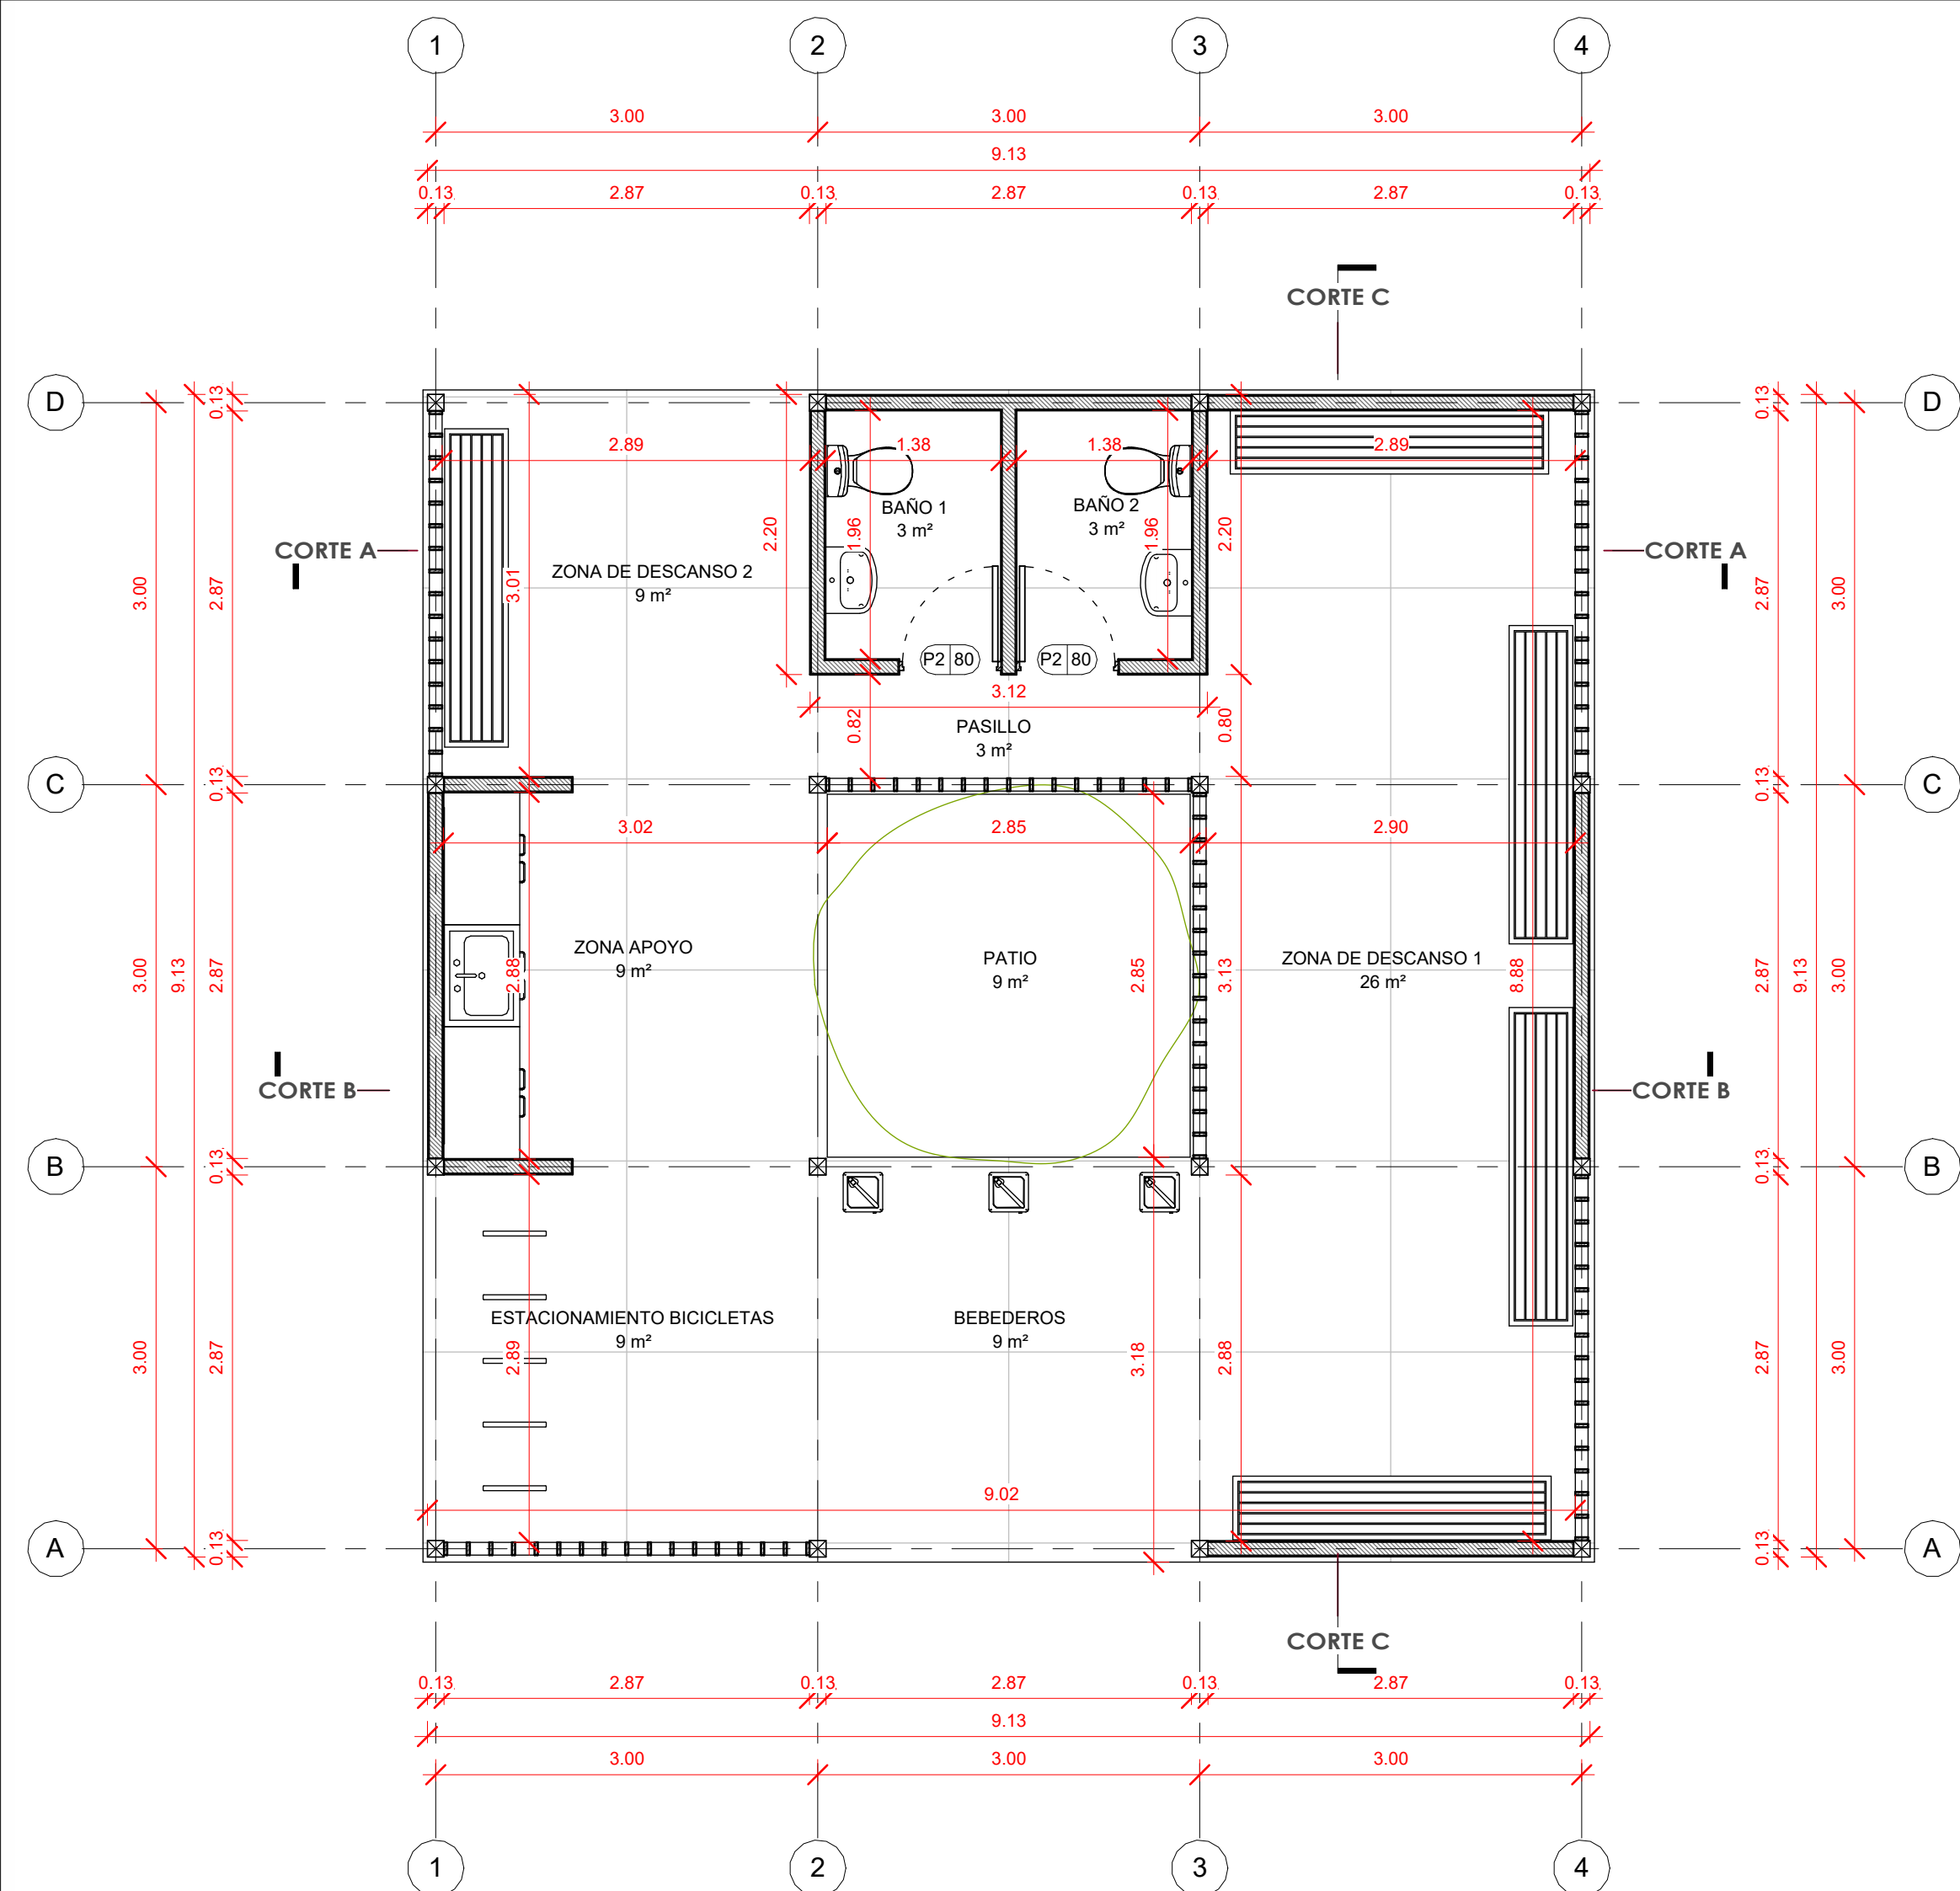


1 PLANTA DE ARQUITECTURA
1 : 50

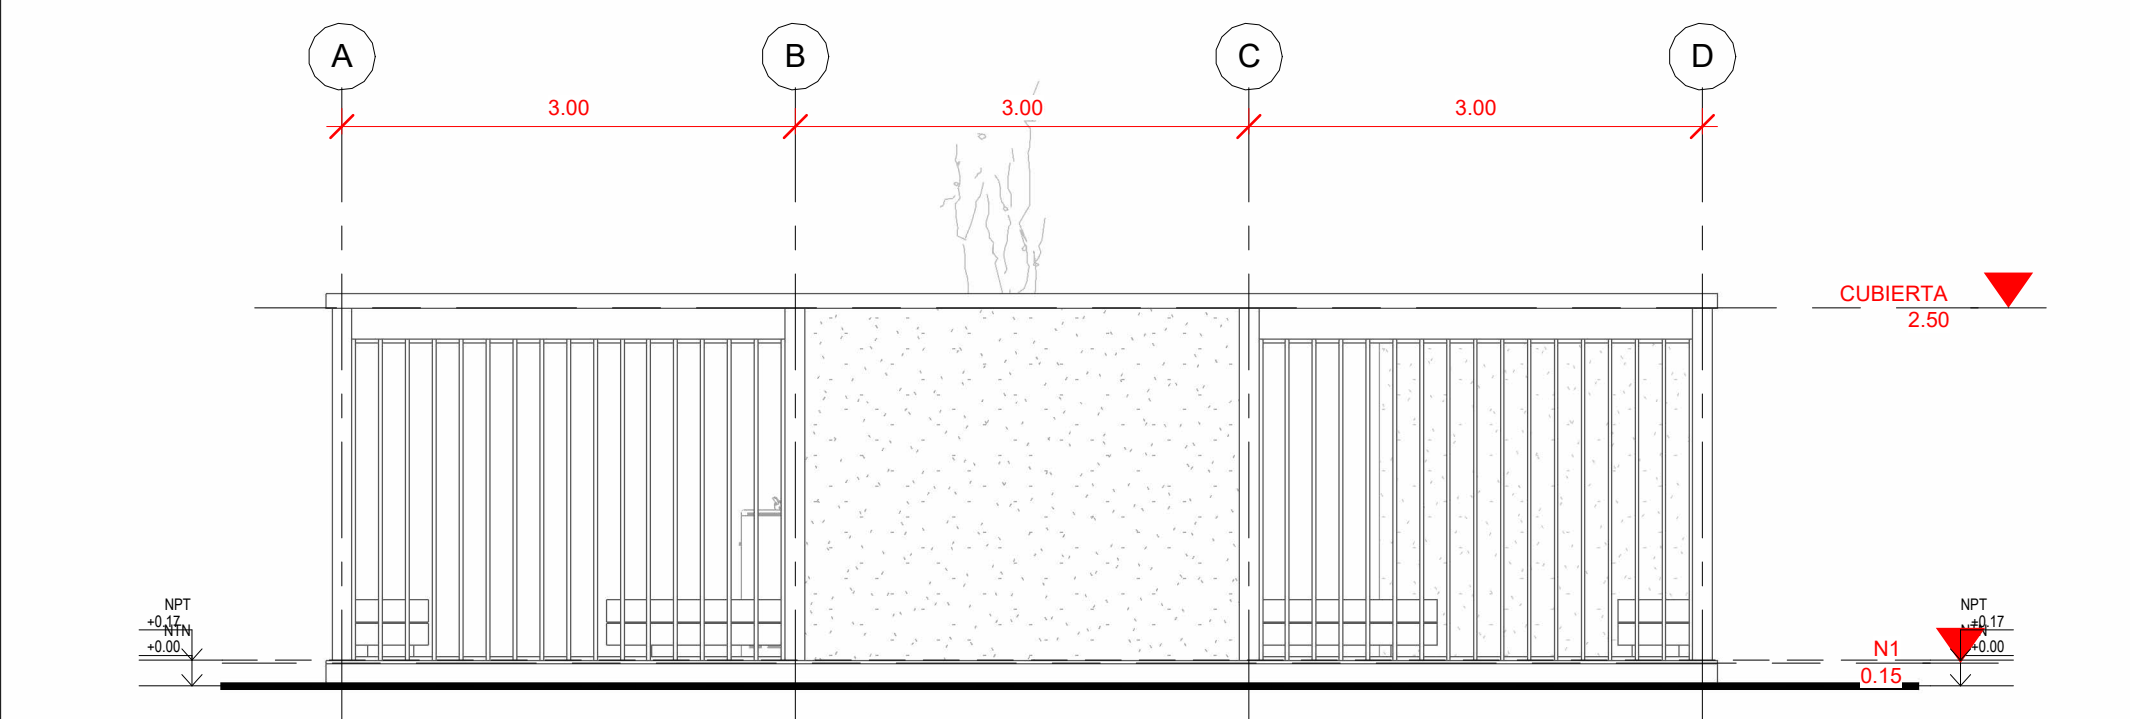


2 ELEVACIÓN 1
1 : 50

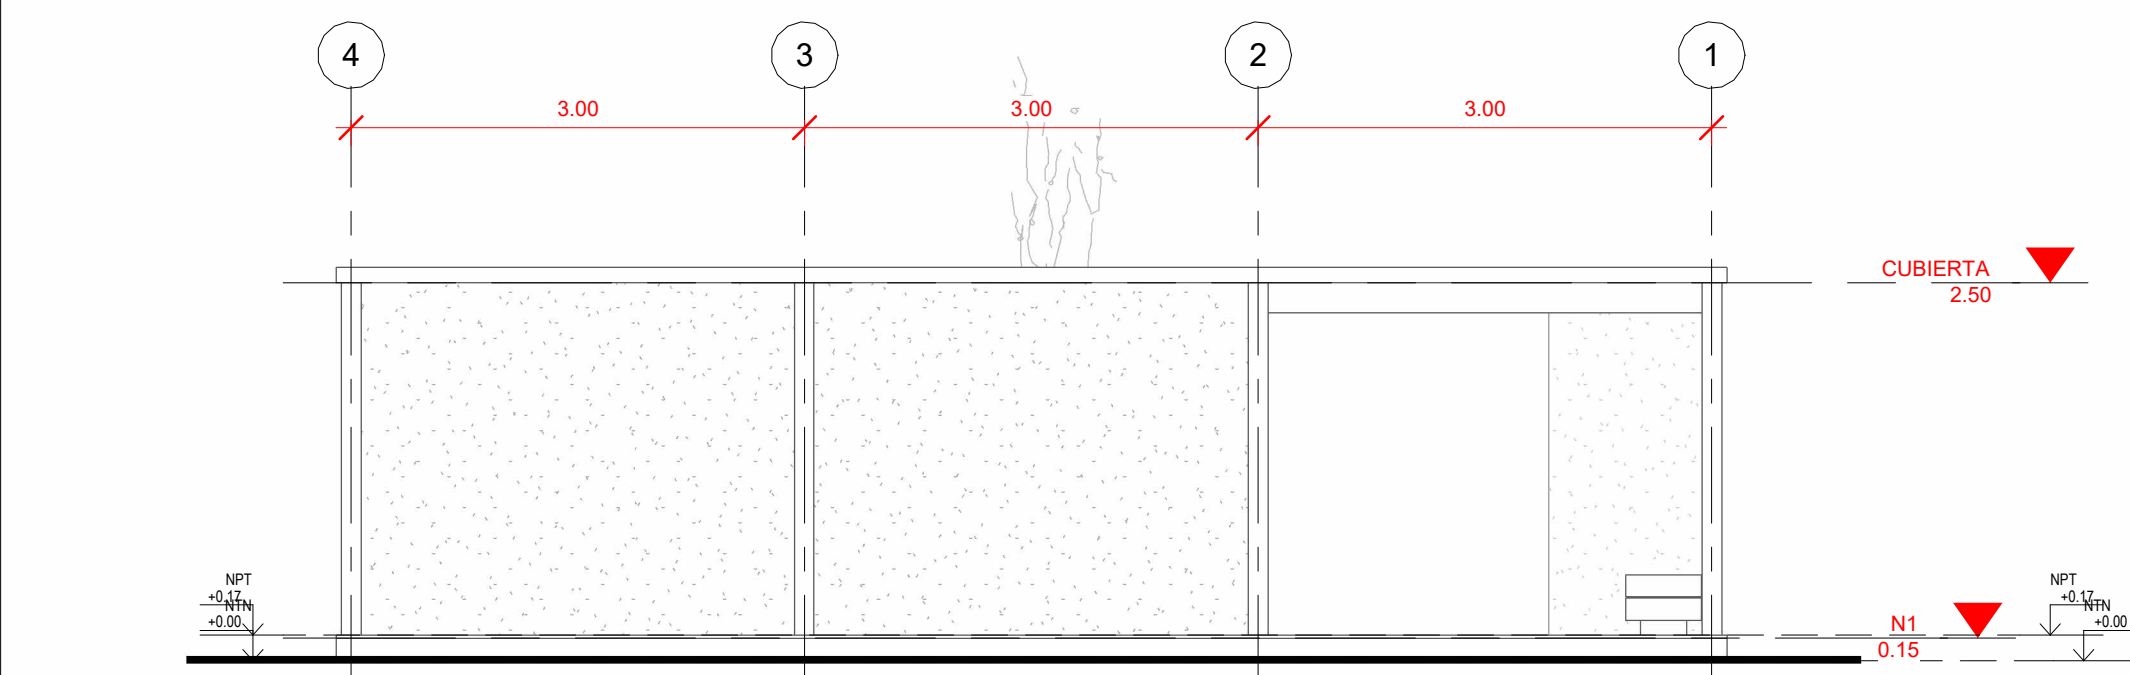


3 ELEVACIÓN 2
1 : 50

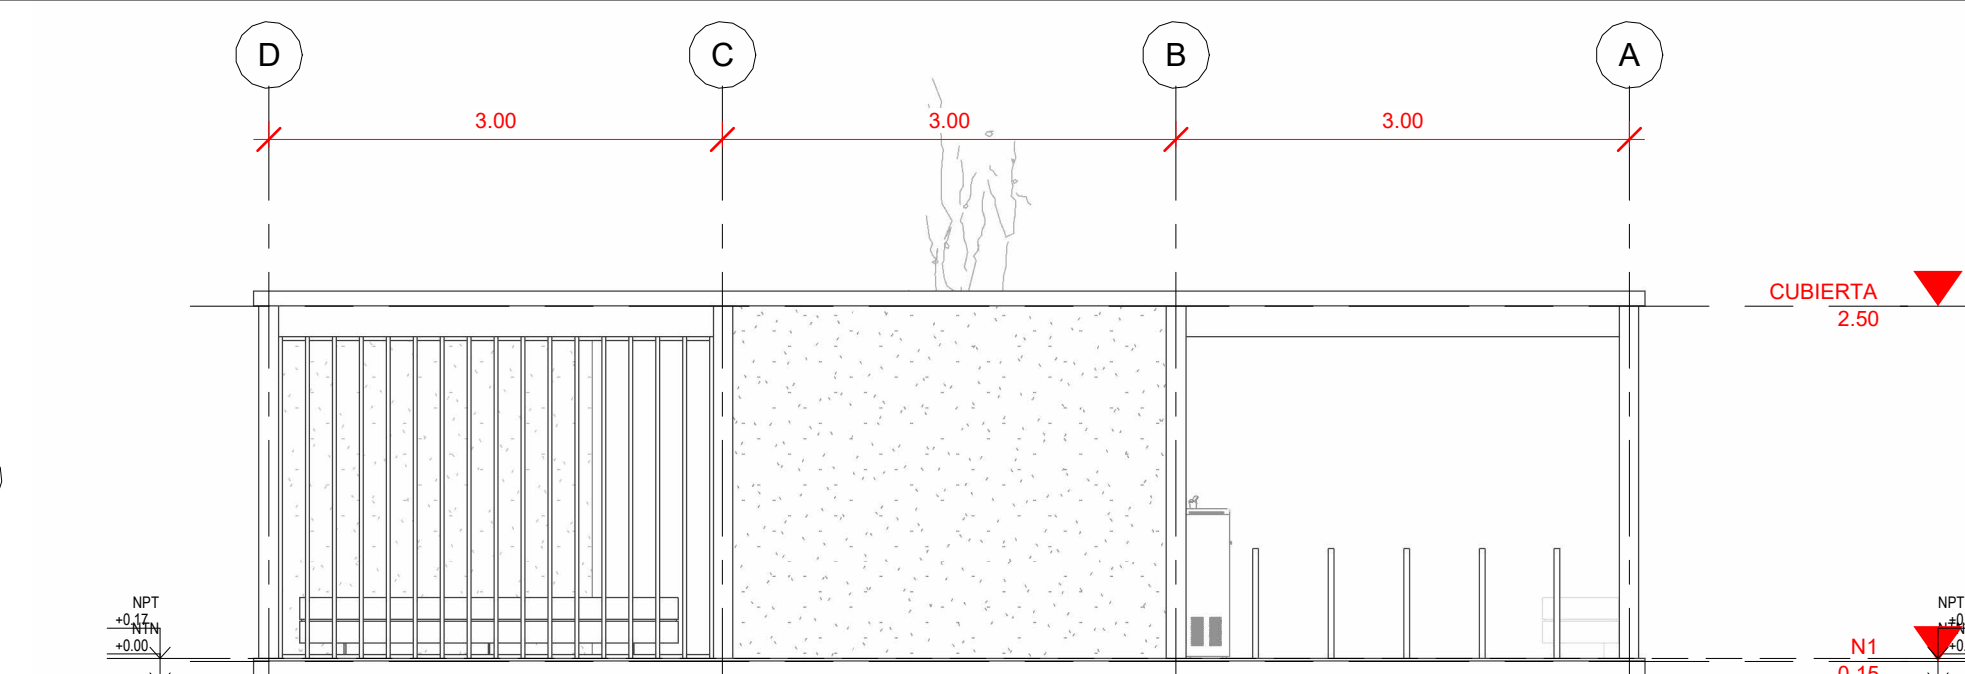


4 ELEVACIÓN 3
1 : 50

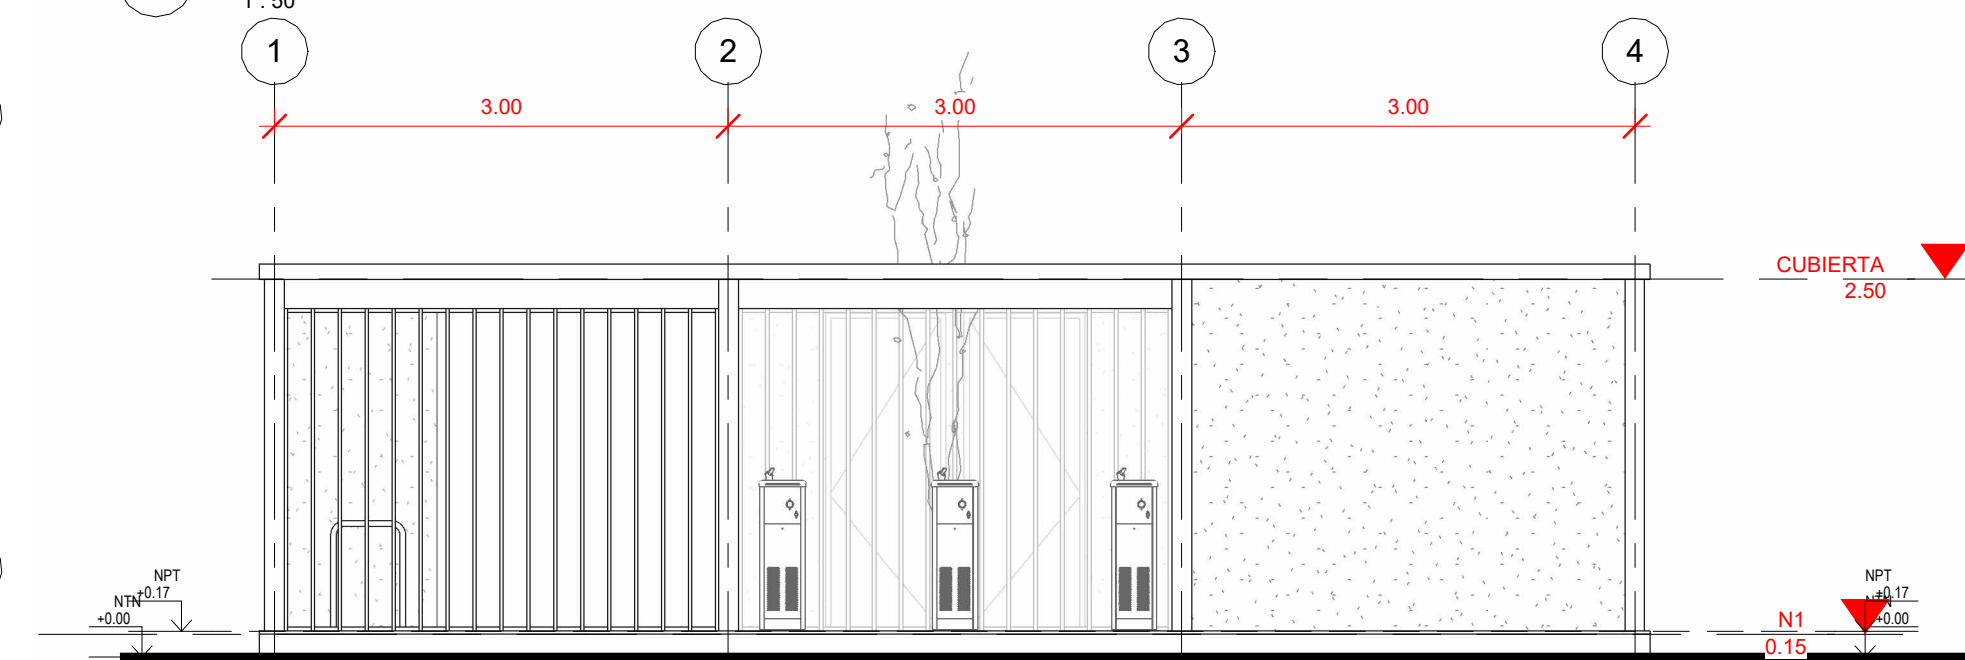


5 ELEVACIÓN 4
1 : 50

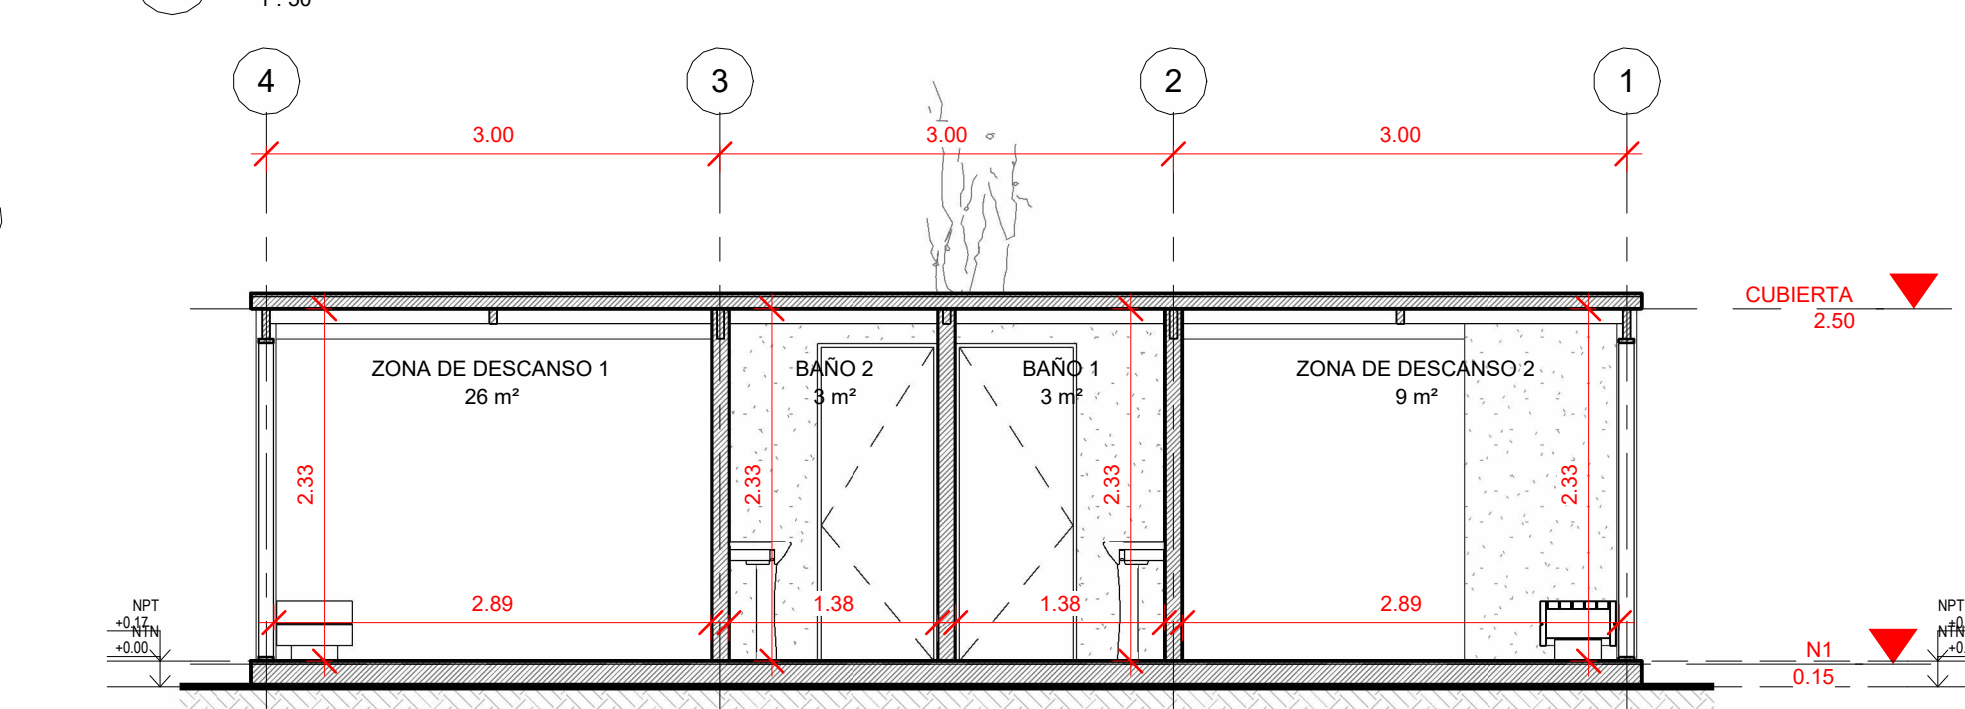


6 CORTE A
1 : 50

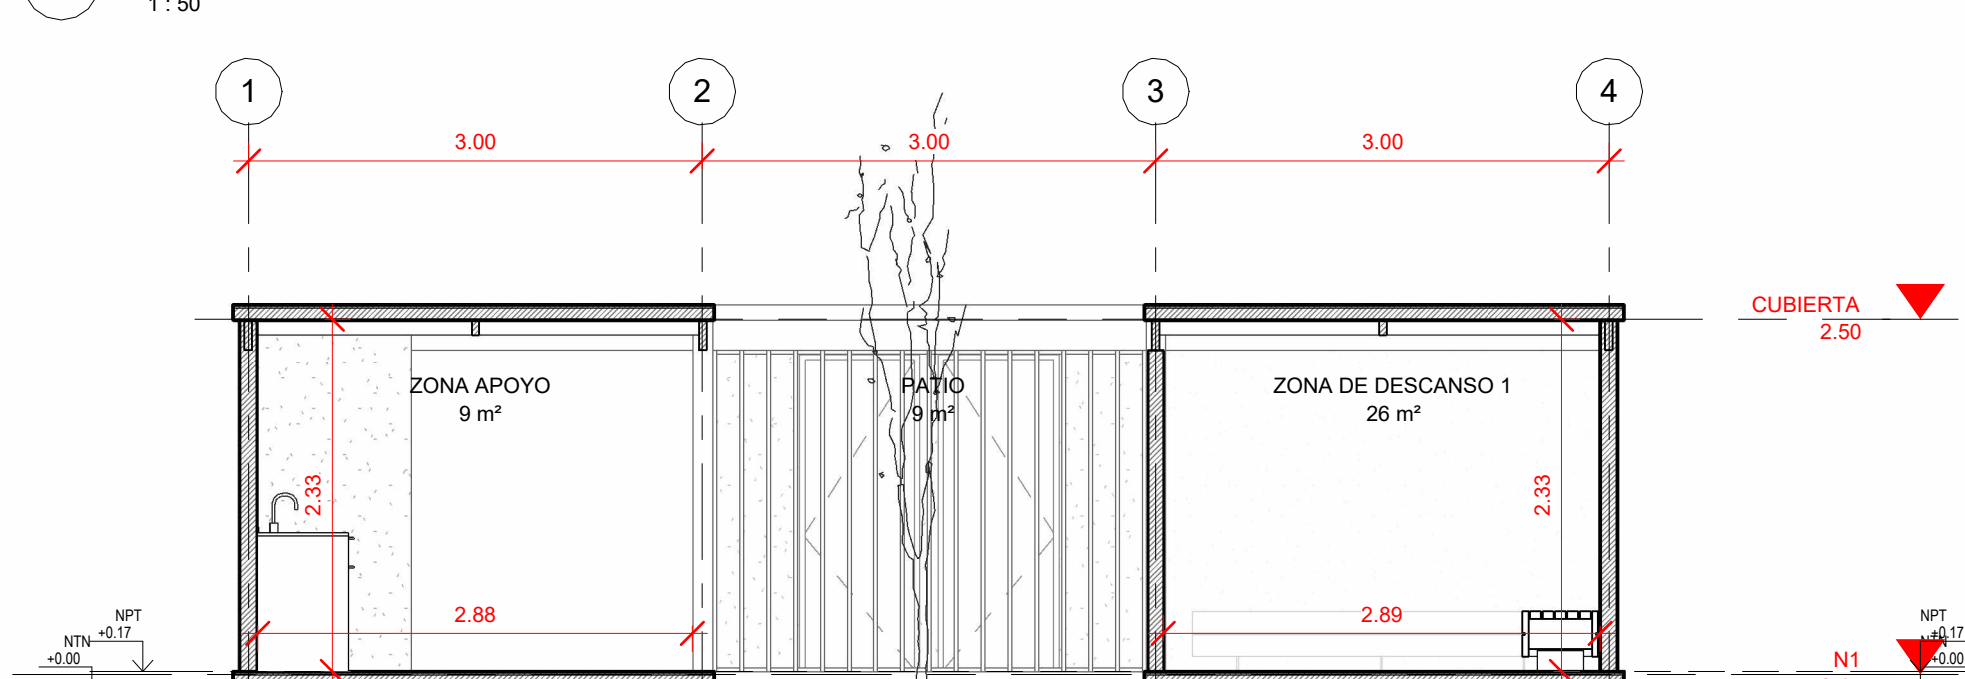


9 CORTE B
1 : 50

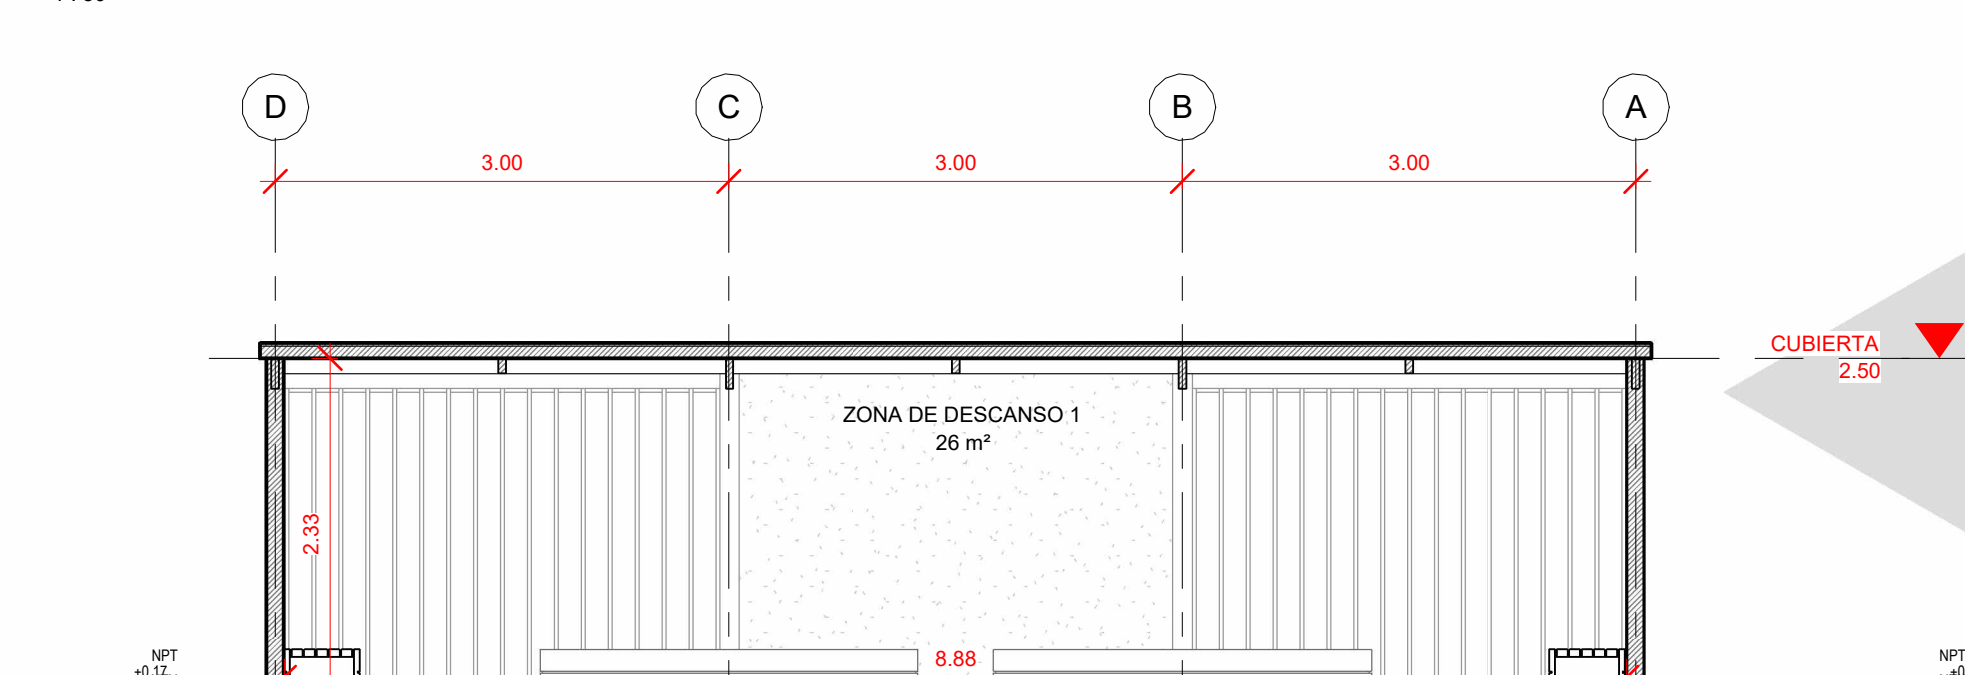

8 CORTE C
1 : 50

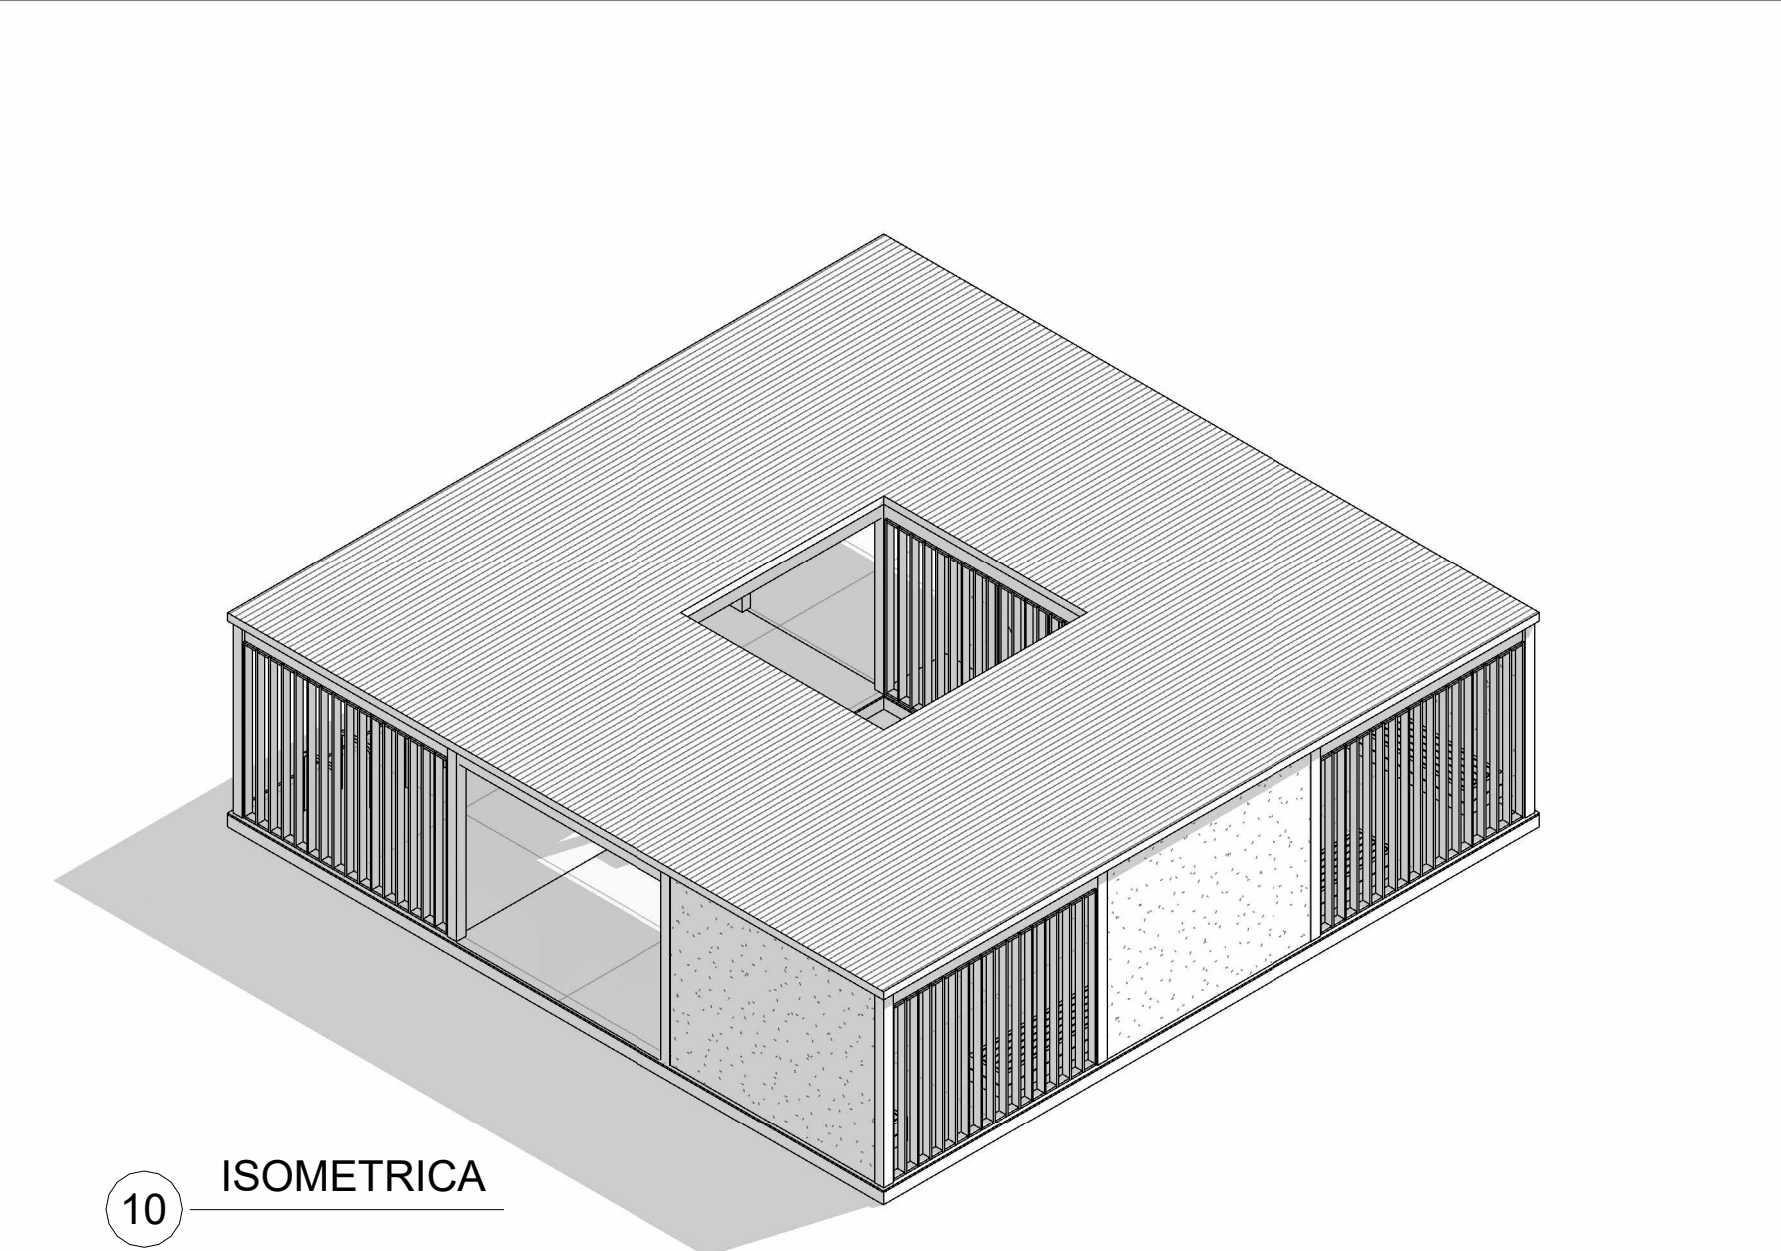

10 ISOMETRICA

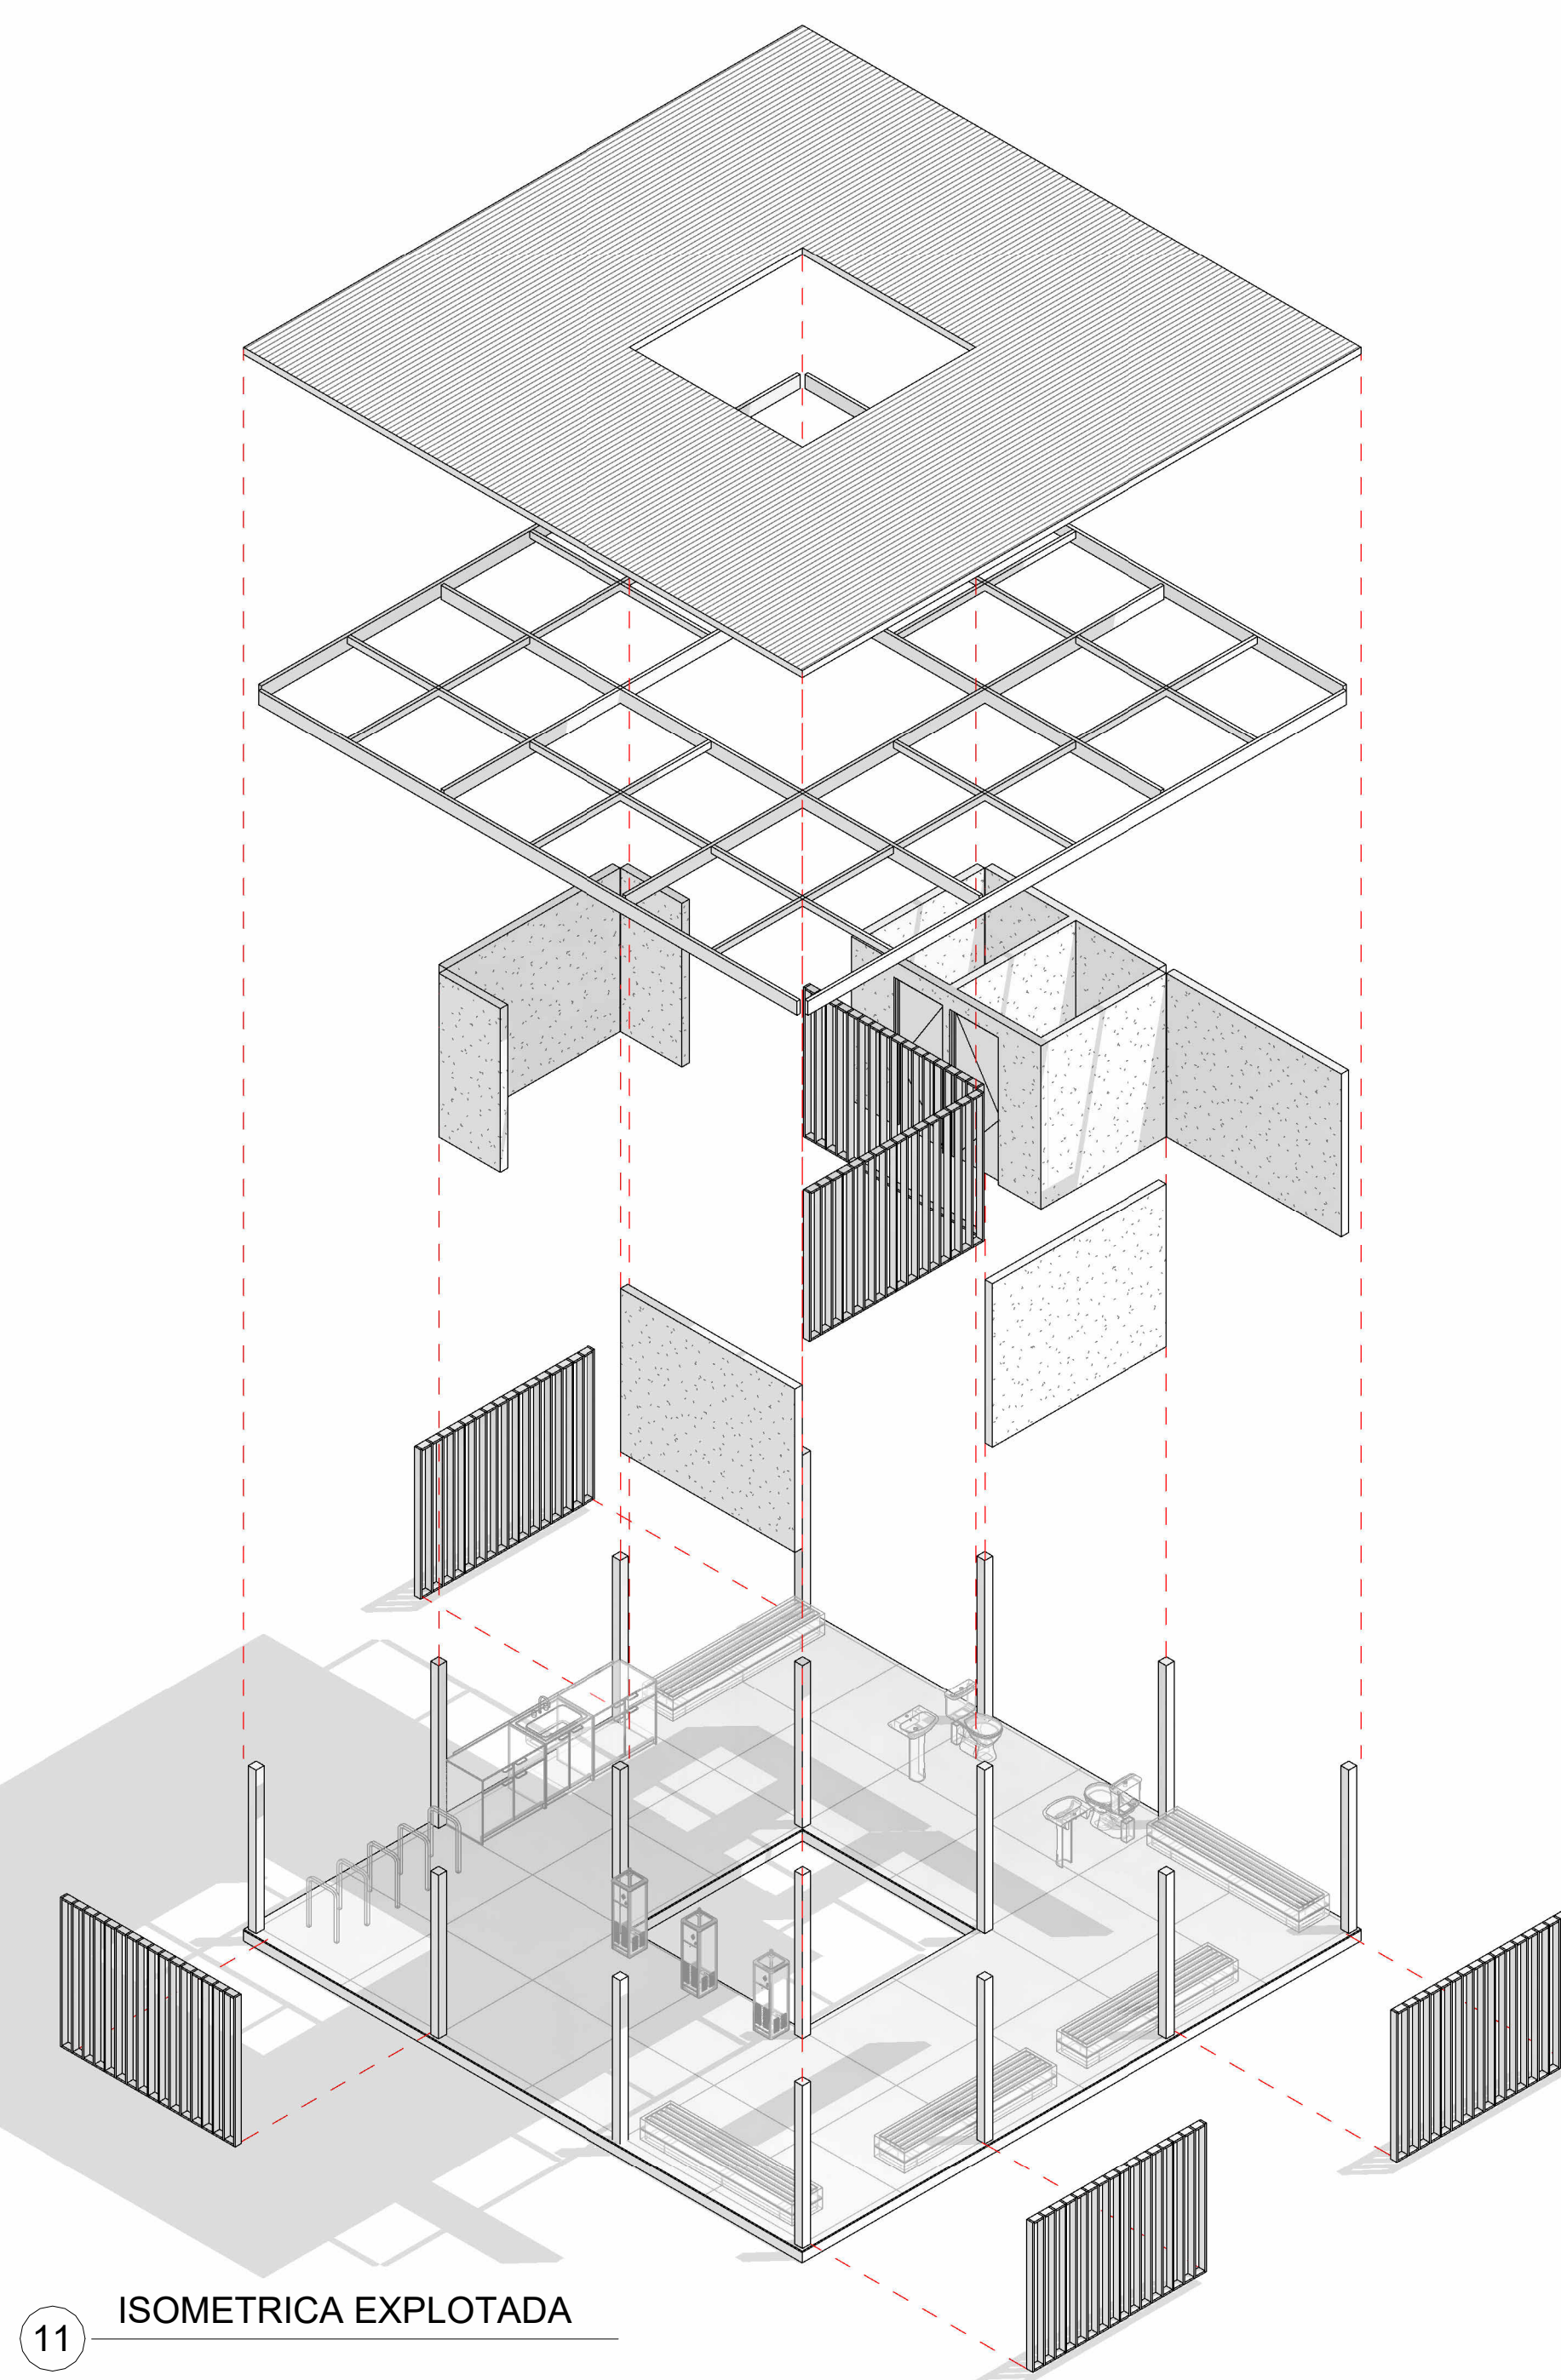

11 ISOMETRICA EXPLOTADA