PM
PAUSA MAULE

PARTIDO REFERENTES IMÁGENES LÁMINAS MATERIALIDAD DOCUMENTOS PROVEEDORES MODELO



HABITÁCULO PARA CICLISTAS · WORKSHOP BIM + IA · MÉTODO TBC
EXTERIOR — EL HABITÁCULO ENTRE EL VALLE Y CORDILLERA DE LA COSTA

VER IMÁGENES ↗

HABITÁCULO PARA CICLISTAS

UN PUNTO DE DESCANSO EN EL CORREDOR VITIVINÍCOLA DE TALCA.

Pausa Maule es un punto de descanso para ciclistas de ruta en el corredor vitivinícola de Talca, Región del Maule. Un vacío central bajo una retícula de nueve cuadrantes ordena masa, umbral y paisaje.

AUTOR	Matías Alvarez C.
REDES	Instagram @matias_arq_ ↗ · LinkedIn ↗
CURSO	Workshop BIM + IA · creado por The BIM Cowork ↗
PROYECTO	Habitáculo Pausa Maule
UBICACIÓN	Talca, Región del Maule
PROGRAMA	9 recintos, 79.45 m^2 totales
MODELO	HAB_ARQ_MODELO_R01.rvt

3×3
RETÍCULA NINE-SQUARE

9
RECINTOS MODELADOS


79.45
M^2 ÁREA TOTAL

16
PROVEEDORES VERIFICADOS

01

EL PARTIDO

CONCEPTO SOBRE LA GRILLA 3×3

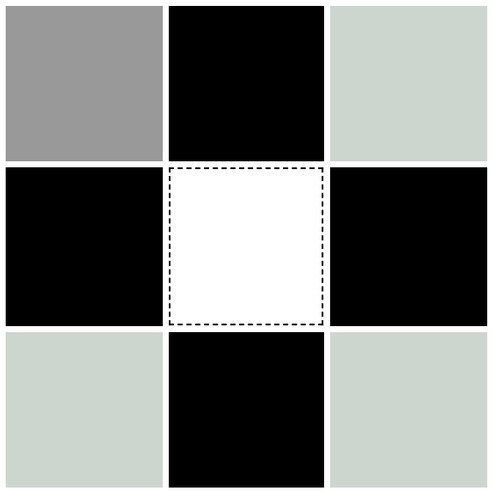

El partido organiza el programa sobre una retícula de nueve cuadrantes: cuatro llenos estructurales (madera + quincha) sostienen un vacío central, el patio, donde crece un árbol a través de la cubierta.

- **Acceso principal** resuelto en el cuadrante superior izquierdo, sin cruzar muros cortina.
- Los **muros cortina** perimetrales quedaron libres de accesos tras la corrección del partido: los recorridos pasan entre los llenos, no a través de los paños vidriados.
- El **patio central** es el umbral entre paisaje y recinto — ahí ocurre la pausa.

LÁMINA DEL PARTIDO (PDF) ↗

llenos, vacíos, accesos y volumen principal

02

REFERENTES

5 PRECEDENTES DE AIRES MATEUS

01 **MASA**

02 **VACÍO**

03 **UMBRAL**

04 **PAISAJE**

05 **RECORRIDO**

Referentes Aires Mateus — contraste nine-square · 5 precedentes contrastados contra el partido de Pausa Maule · selección de 4 láminas, PDF completo de 9 páginas

PAUSA MAULE · HABITÁCULO 3×3

AIRES MATEUS

Referentes existentes

Masa, vacío, umbral, luz y paisaje como herramientas para proyectar una pausa ciclista.



Cabanas no Rio · Comporta, 2013 · Fot. Nelson Garrido

ARQUITECTURA · SELECCIÓN CONCEPTUAL

01

05 **EL MURO TAMBIÉN CONSTRUYE EL UMBRAL**



Pa.te.os · Melides, 2020 · Fot. João Guimarães

03 · PA.TE.OS

Muros continuos delimitan recintos y, al ser atravesados, producen negativos profundos que encuadran el paisaje.

LÍMITE

El muro define una habitación incluso cuando no completa un volumen.

UMBRAL

La abertura tiene profundidad suficiente para convertirse en estancia.

PAISAJE

El vacío dirige la mirada y relaciona arquitectura con vegetación.

APLICACIÓN

Convertir la celda de acceso en una pausa cubierta, no en un simple paso.

02

DESAPARECER PARA CONSTRUIR UN CENTRO PROTEGIDO





Casa en Monsaraz · Alentejo, 2018 · Fot. João Guimarães

04 · CASA EN MONSARAZ

El terreno oculta la casa; patios circulares y una abertura superior revelan su organización.

APLICACIÓN

Proteger el centro sin aislarlo del horizonte.

03

EL RECORRIDO ARTICULA INTIMIDAD, ENCUENTRO Y PAISAJE





Nursing Home · Alcácer do Sal, 2010 · Fot. Fernando Guerra / FG+SG

05 · NURSING HOME

Unidades independientes forman un cuerpo continuo; los retranqueos median entre intimidad y vida colectiva.

APLICACIÓN

Hacer del acceso y el patio una secuencia breve de sombra, pausa y encuentro.

04

ABRIR PDF COMPLETO ↗

03

IMÁGENES DEL PROYECTO

RENDERS E ISOMÉTRICAS



VISTA AÉREA – EL PATIO Y EL ÁRBOL ATRAVESANDO LA CUBIERTA




INTERIOR – BEBEDEROS Y DESCANSO




INTERIOR – UMBRAL HACIA EL VALLE


VISTAS ISOMÉTRICAS

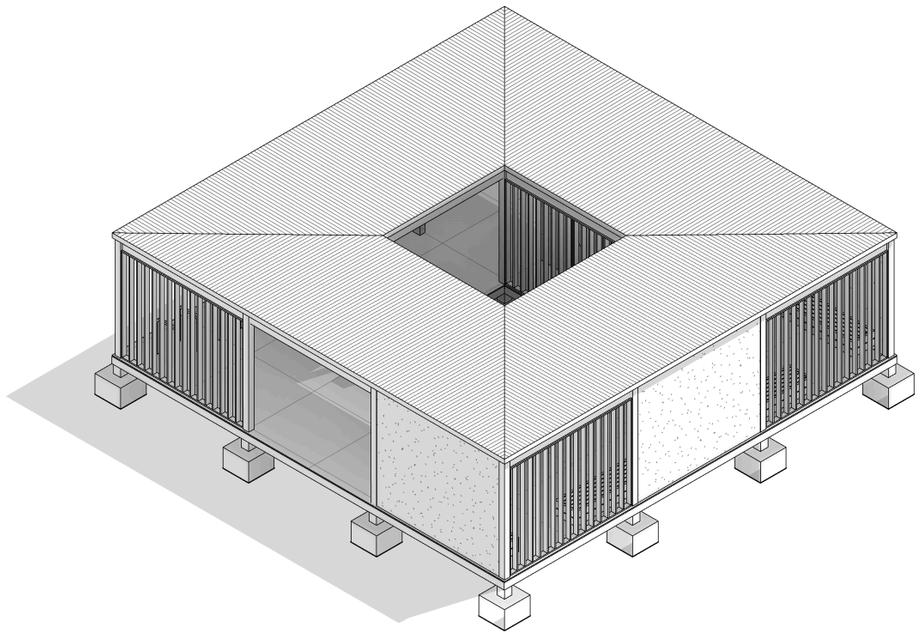

Volumen, cubierta y patio

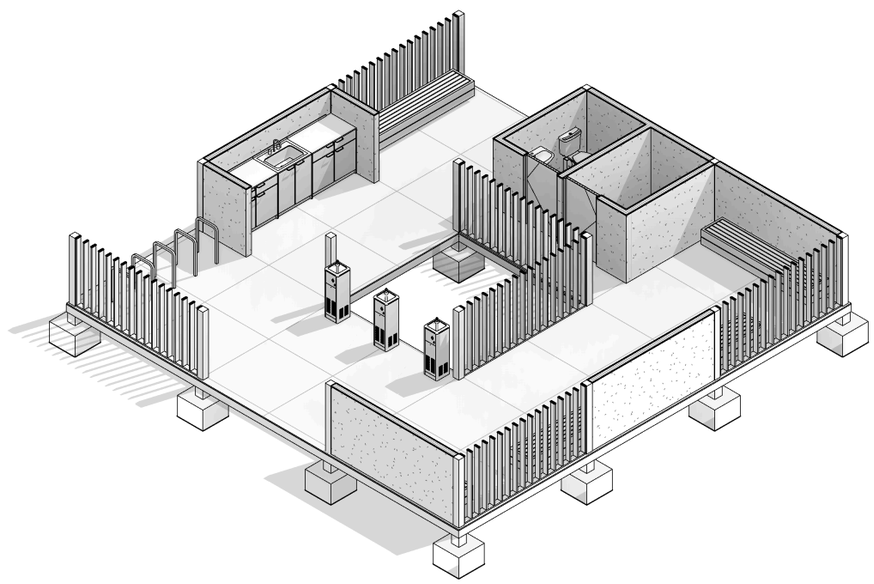

Sin cubierta — bebederos, baño, apoyo y bicicletas

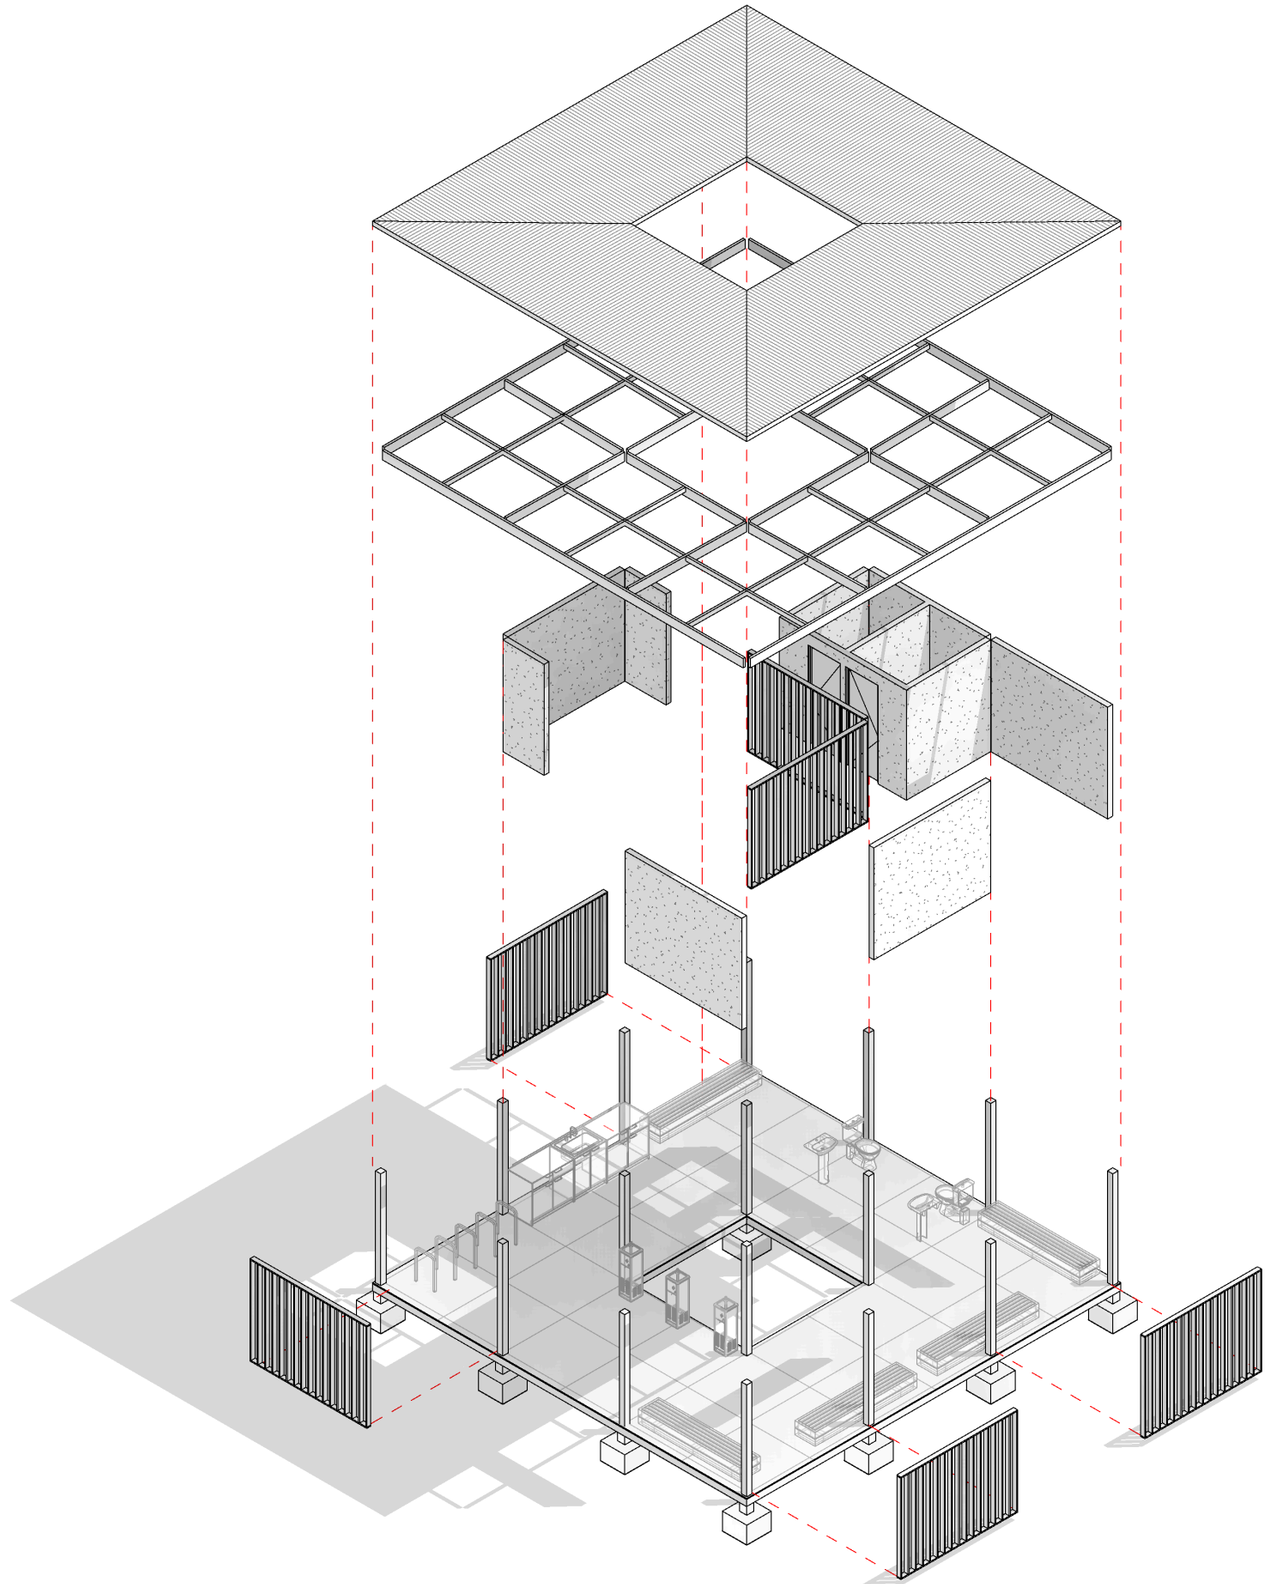

Isométrica explotada — capas constructivas: cubierta, armazón, paramentos y mobiliario

VIDEOS



Interior — bebederos y descanso



Exterior — el habitáculo entre viñedos

04

LÁMINAS

PLANIMETRÍA TÉCNICA

Lámina A101 — Planimetría general · planta, 4 elevaciones, 3 cortes, cubierta, superficies, isométricas y tablas · 1:50

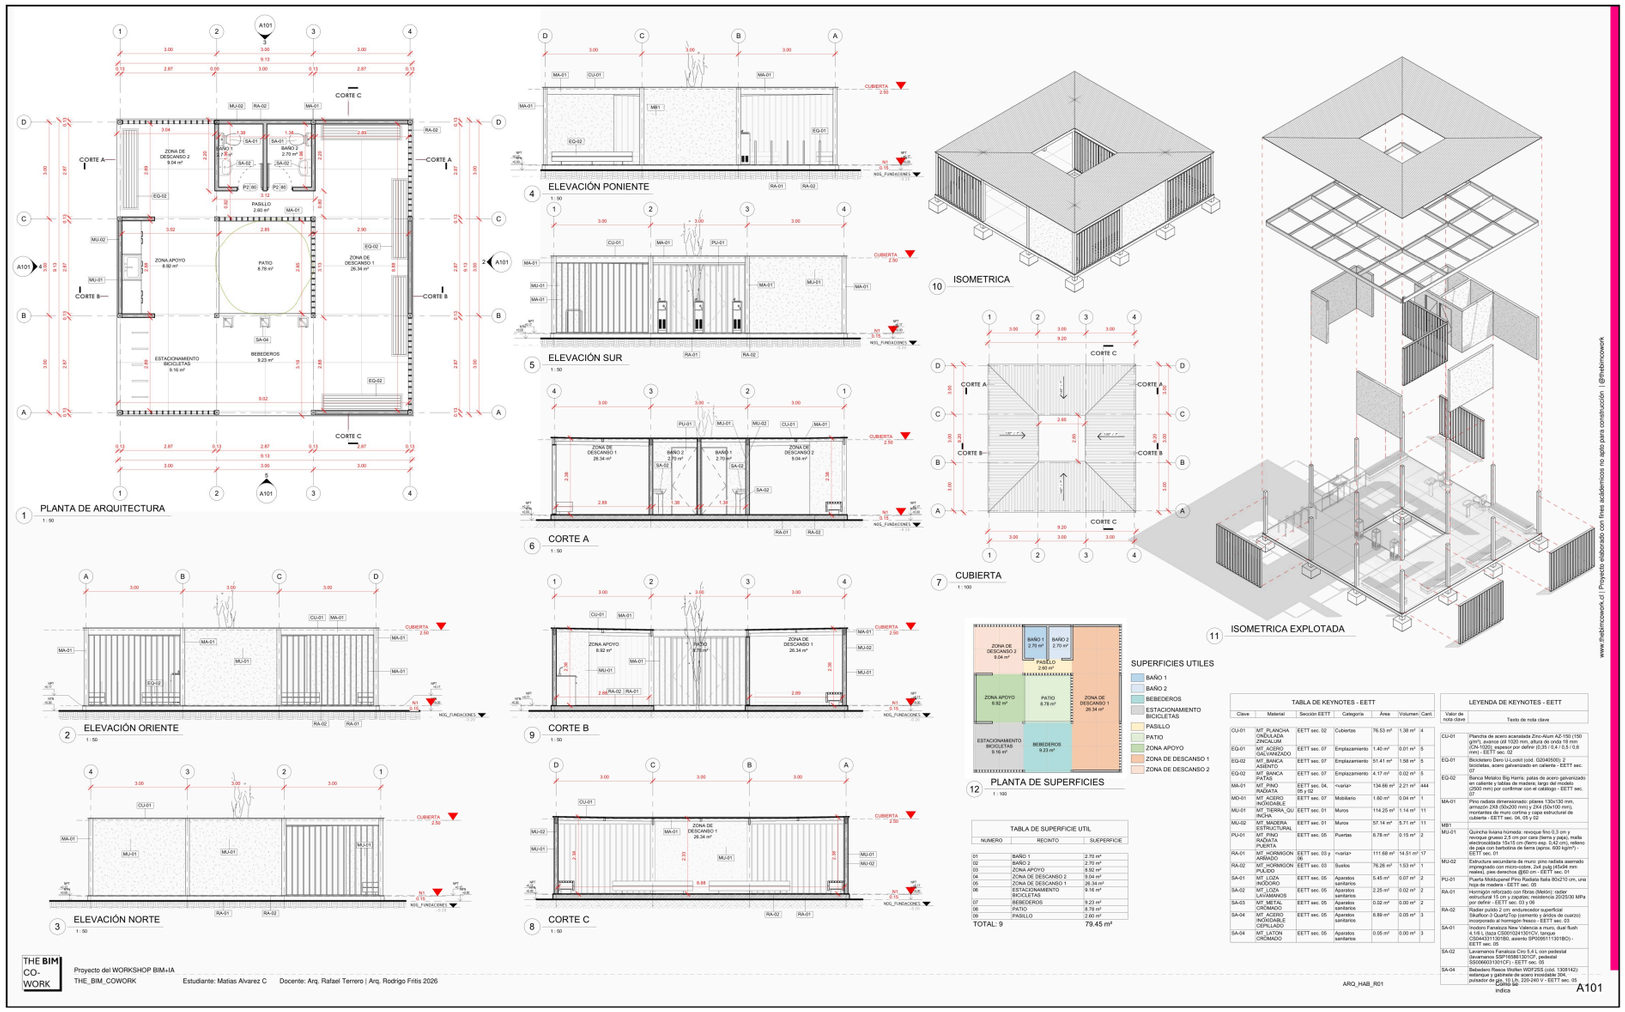


TABLA DE SUPERFICIE UTIL

NUMERO	RECINTO	SUPERFICIE
01	BAÑO 1	2.70 m²
02	BAÑO 2	2.70 m²
03	ZONA APOYO	8.92 m²
04	ZONA DE DESCANSO 2	9.04 m²
05	ZONA DE DESCANSO 1	26.34 m²
06	ESTACIONAMIENTO BICICLETAS	9.16 m²
07	BEBEDEROS	9.23 m²
08	PATIO	8.78 m²
09	PASILLO	2.60 m²
TOTAL: 9		79.45 m²

TABLA DE KEYNOTES - EETT

Clave	Material	Sección EETT	Categoría	Área	Volumen	Cant.
CU-01	MT_PLANCHA ONDULADA ZINCALUM	EETT sec. 02	Cubiertas	76.53 m²	1.38 m³	4
EQ-01	MT_ACERO GALVANIZADO	EETT sec. 07	Emplazamiento	1.40 m²	0.01 m³	5
EQ-02	MT_BANCA RADIATA	EETT sec. 07	Emplazamiento	51.41 m²	1.56 m³	5
EQ-02	MT_BANCA PATAS	EETT sec. 07	Emplazamiento	4.17 m²	0.02 m³	5
MA-01	MT_PINO RADIATA	EETT sec. 04, 05 y 02	<varia>	134.66 m²	2.21 m³	444
MO-01	MT_ACERO INOXIDABLE	EETT sec. 07	Mobiliario	1.60 m²	0.04 m³	1
MU-01	MT_TIERRA_QU INCHA	EETT sec. 01	Muros	114.25 m²	1.14 m³	11
MU-02	MT_MADERA ESTRUCTURAL	EETT sec. 01	Muros	57.14 m²	5.71 m³	11
PU-01	MT_PINO RADIATA PUERTA	EETT sec. 05	Puertas	6.78 m²	0.15 m³	2
RA-01	MT_HORMIGON ARMADO	EETT sec. 03 y <varia>	<varia>	111.68 m²	14.51 m³	17
RA-02	MT_HORMIGON PULIDO	EETT sec. 03	Suelos	76.26 m²	1.53 m³	1
SA-01	MT_LOZA INODORO	EETT sec. 05	Aparatos sanitarios	5.45 m²	0.07 m³	2
SA-02	MT_LOZA LAVAMANOS	EETT sec. 05	Aparatos sanitarios	2.25 m²	0.02 m³	2
SA-03	MT_METAL CROMADO	EETT sec. 05	Aparatos sanitarios	0.02 m²	0.00 m³	2
SA-04	MT_ACERO INOXIDABLE PULIDO	EETT sec. 05	Aparatos sanitarios	6.89 m²	0.05 m³	3
SA-04	MT_LATON CROMADO	EETT sec. 05	Aparatos sanitarios	0.05 m²	0.00 m³	3

LEYENDA DE KEYNOTES - EETT

Valor de nota clave	Texto de nota clave
CU-01	Plancha de acero acanalada Zinc-Alum AZ-150 (150 g/m², aluinc) 28 1020 mm, altura de onda 19 mm (ZA 1020), espesor por definir (0.35 / 0.4 / 0.5 / 0.8 mm) - EETT sec. 02
EQ-01	Bicicletero Dero U-Loc6rl (cod. GS040500) 2 unidades, acero galvanizado en caliente - EETT sec. 07
EQ-02	Banca Metalco Big Harris: patas de acero galvanizado en caliente y tablas de madera; largo del modelo (2500 mm) por confirmar con el catálogo - EETT sec. 07
MA-01	Pino radiata deterenzostado: pilares 130x130 mm; armazón 2X6 (90x200 mm) y 2X4 (50x100 mm), montantes de muro cortina y capa estructural de cubierta - EETT sec. 04, 05 y 02
MB1	
MU-01	Quincha liviana húmeda: revoque fino 0,3 cm y revoque grueso 2,5 cm con malla de fibra de vidrio y malla electrosoldada 15x15 cm (ferro eq. 5-6,2 cm), relleno de paja con barbotina de tierra (aprox. 600 kg/m³) - EETT sec. 01
MU-02	Estructura secundaria de muro: pino radiata aserrado impregnado con micro-sobre, 2x4 pulg (45x94 mm reales), pies derechos @40 cm - EETT sec. 01
PU-01	Puerta de madera: Modelo Tala 80x210 cm, una hoja de madera - EETT sec. 05
RA-01	Hormigon reforzado con fibras (Metrix): radier estructural 15 cm y zapatas; resistencia 20/25/30 MPa por definir - EETT sec. 03 y 06
RA-02	Radier pulido 2 cm: endurecedor superficial Sikafloor-3 QuartzTop (cemento y áridos de cuarzo) aplicado en capa de terminación - EETT sec. 03
SA-01	Inodoro Fanaloza New Valencia 4 Hydr.dual flush 4.1/6 L (tipo CS0010241SH)Cv: tanque (CS0443311SI190), asiento SP0050111SI190) - EETT sec. 05
SA-02	Lavamanos Fanaluza Cirro 5.4 L con pedestal (lavamanos SSP1935BE130YCP, pedestal SSP1935BE130YCP) - EETT sec. 05
SA-04	Bebedero Rheva Wotter WGF250L (cod. 139142): estanque y gabinete de acero inoxidable 304, potencia de gas 10 Lh, 220-240 V - EETT sec. 05

www.thebimcowork.cl | Proyecto elaborado con fines académicos no apto para construcción | @thebimcowork

05

MATERIALIDAD

VERIFICADA CONTRA FICHAS DE FABRICANTE



QUINCHA

`MURO_EXT_QUINCHA_12cm`

Sistema quincha liviana húmeda — Corporación Protierra Chile, red MINVU/DITEC.

VER ELEMENTO ↗



PINO RADIATA

`MT_PINO RADIATA · MLE 20c`

Pilares glulam Hilam MLE, armazón dimensionado y montantes Arauco. Los paneles del muro cortina quedan vacíos (celosía).

VER ELEMENTO ↗




ZINCALUM

`MT_PLANCHA ONDULADA ZINCALUM`

Plancha ondulada sobre estructura de madera — Cubiertas Nacionales CN-1020.

VER ELEMENTO ↗

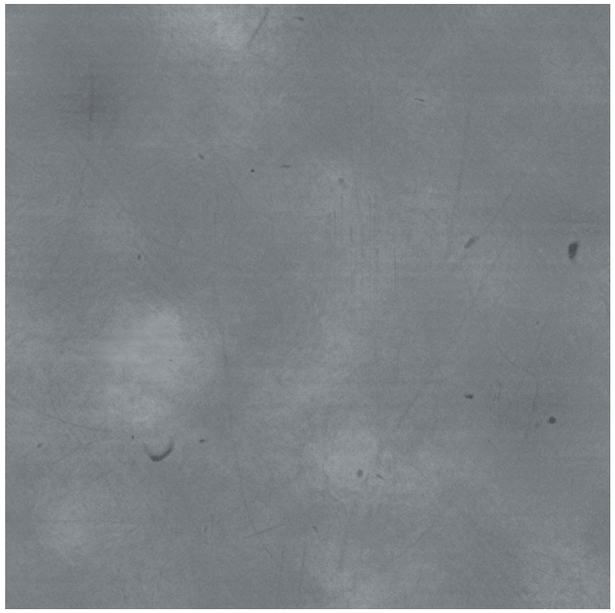

HORMIGÓN

`PAV_INT_HORMIGON PULIDO_2cm`

Radier con fibra Melón + endurecedor superficial Sikafloor-3 QuartzTop. El mismo hormigón armado forma las 16 zapatas aisladas bajo los pilares.

VER ELEMENTO ↗

06

DOCUMENTOS TÉCNICOS

REGLAS, PEB, NDI Y PARÁMETROS

REGLAS DE TRABAJO BIM

Resumen del Estándar PlanBIM Chile aplicado a Pausa Maule · Paso 01

PDF ↗

ESPECIFICACIÓN TÉCNICA

Materiales, fichas de fabricante, categorías cerradas

PDF ↗

PEB PRELIMINAR

Plan de Ejecución BIM — etapa preliminar

PDF ↗

PEB COMPLETADO

Tabla NDI por categoría y 9 recintos (nombre, número, nivel, área, perímetro)

XLSX ↓ PDF ↗

TABLA NDI

Niveles de Desarrollo de la Información

PDF ↗

PARÁMETROS COMPARTIDOS

Grupo NDI2 — parámetros compartidos del proyecto

TXT ↓ PDF ↗

07

PROVEEDORES

16 PROVEEDORES VERIFICADOS

FICHAS DE PROVEEDORES

16 proveedores verificados · contacto, sitio web, ficha técnica

XLSX ↓

ELEMENTO	EMPRESA	PRODUCTO	SITIO WEB	FICHA TÉCNICA
Muro / Quincha	Corporación Protierra Chile	Sistema Quincha Liviana Húmeda	redproterra.org	FICHA TÉCNICA ↗
Cubierta	Cubiertas Nacionales	Panel Ondulado CN-1020	cubiertasnacionales.cl	FICHA TÉCNICA ↗
Radier y zapatas	Melón	Hormigón con Fibra	melon.cl	FICHA TÉCNICA ↗
Radier pulido	Sika Chile	Sikafloor-3 QuartzTop	chl.sika.com	FICHA TÉCNICA ↗
Pilar estructural	Arauco — Hilam	Madera Laminada Encolada MLE 20c	arauco.com/hilam	FICHA TÉCNICA ↗
Armazón	Arauco — MSD	Construcción Premium MSD	arauco.com	FICHA TÉCNICA ↗
Muro cortina — montante	Arauco — MSD	Pino Radiata Cepillado	arauco.com	FICHA TÉCNICA ↗
Muro cortina — panel	Arauco	Panel vacío (celosía) — ficha de referencia: MSD Revestimiento Machihembrado	arauco.com/chile	FICHA TÉCNICA ↗
Puerta	Moldupanel (Puertas Chile)	Puerta Pino Radiata Italia 80×210	puertaschile.cl	—
Herrajes	Häfele (vía El Carpintero)	Bisagras y cerraduras	elcarpintero.cl	FICHA TÉCNICA ↗
Sanitarios	Fanaloza	New Valencia a Muro / Lavamanos Ciro	fanaloza.cl	FICHA TÉCNICA ↗
Bebedero	Reece	Wolfen Sensor Drinking Fountain WDF2SS	reece.com.au	FICHA TÉCNICA ↗
Lavaplatos	Fanaloza	Lavaplatos de sobreponer con escurridor 80×50	fanaloza.cl	FICHA TÉCNICA ↗
Bicicletero	Dero Bike Racks	U-Lockit	dero.com	FICHA TÉCNICA ↗
Banca	Metalco	Big Harris (ficha de terceros)	metalco.it	FICHA TÉCNICA ↗

Abastecimiento local	Sodimac / Easy / Construmart Talca	Distribución general	sodimac.cl easy.cl construmart.cl	—

DESCARGAR DOCUMENTOS E IMÁGENES

Referentes, proveedores, documentos técnicos, láminas e imágenes — no incluye el modelo Revit ni el IFC (ver punto 08).

↓ DESCARGAR (.ZIP, 35 MB)


08


MODELO REVIT

HAB_ARQ_MODELO_R01.RVT

7 533	944	194	76	53	3+2
ELEMENTOS TOTALES	TIPOS	FAMILIAS	CATEGORÍAS	VISTAS	NIVELES PRINCIPALES + SUBNIVELES

VISOR 3D

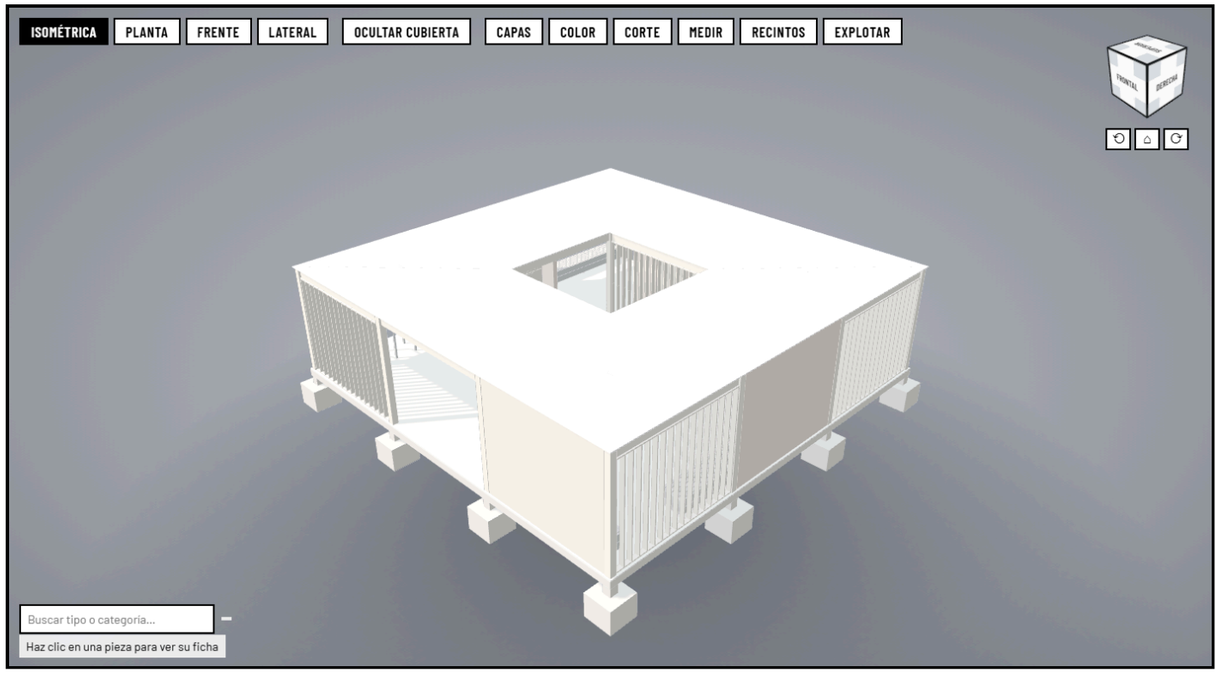

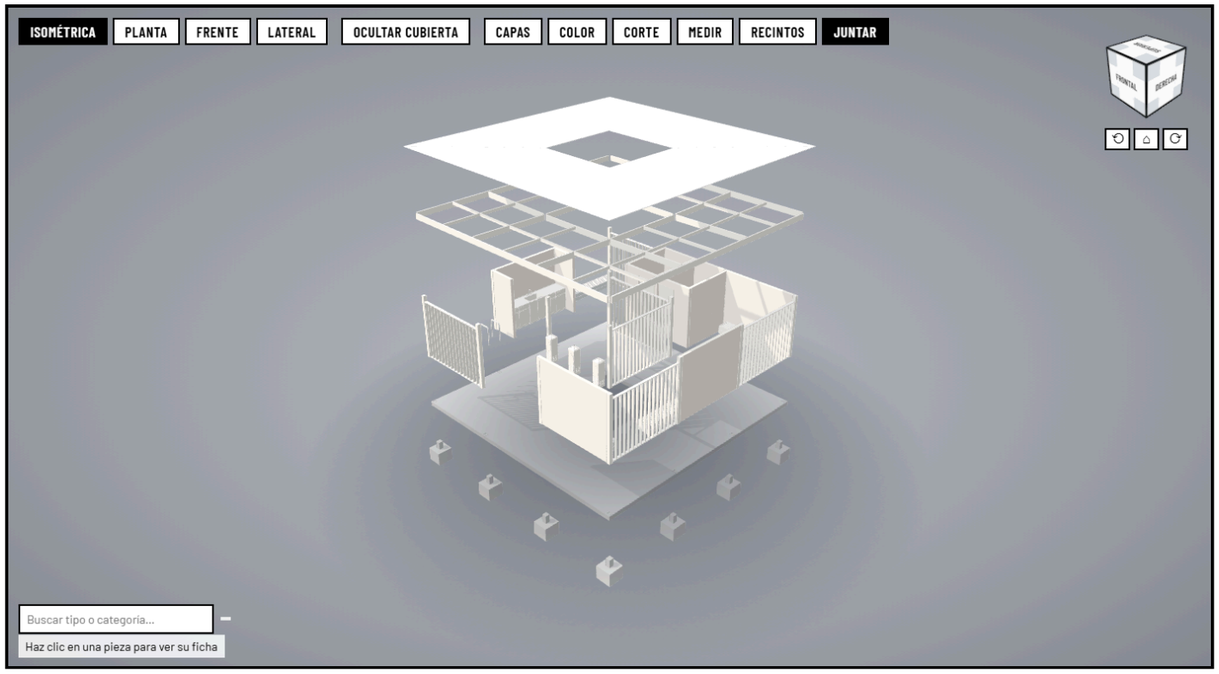

CANTIDADES DEL MODELO

CATEGORÍA	TIPO	CANT.	MEDIDA
Muros	MURO_EXT_QUINCHA_12cm	11	57,14 m^2 · 6,86 m^3
Muros cortina	M.CORTINA_EXT_CELOSIA_PINO RADIATA (FIX N)	6	37,29 m^2
Montantes de muro cortina	12.5x100mm_PINO RADIATA	396	250,2 m · 0,63 m^3
Paneles de muro cortina	Empty (celosía)	192	31,04 m^2
Puertas	80x210cm	2	—
Pilares estructurales	130X130	16	0,65 m^3
Armazón principal	2"X8" Sin cepillar	16	71,4 m · 0,70 m^3
Armazón secundario	2"X4" Cepillada	16	48,0 m · 0,24 m^3
Fundaciones aisladas	FUNDACIÓN AISLADA_HA_60x60x50cm	16	3,03 m^3
Radier estructural	RADIER_INT_HA_15cm	1	76,56 m^2 · 11,49 m^3
Pavimento pulido	PAV_INT_HORMIGON PULIDO_2cm	1	76,26 m^2 · 1,53 m^3
Cubierta (4 faldones)	CUBIERTA_ZINC ONDULADO_10cm	4	76,53 m^2 · 1,38 m^3
Inodoros	41x69cm	2	0,07 m^3
Lavamanos	53x41cm	2	0,02 m^3
Bebederos	31x32cm	3	0,05 m^3
Lavaplatos	80x60cm	1	0,04 m^3
Muebles base de cocina	104x64cm	2	0,09 m^3
Bancas	250x50cm	5	1,60 m^3
Bicicleteros	2 bicicletas	5	0,01 m^3
Recintos	9 recintos	9	79,45 m^2

DESCARGAR EXCEL (.XLSX) ↓ DESCARGAR CSV ↓

ARCHIVOS DEL MODELO

HAB_ARQ_MODELO_R01.RVT

Modelo BIM del habitáculo Pausa Maule · 233 MB

DESCARGAR ↗

HAB_ARQ_MODELO_R01_IFC4X3.IFC

Export IFC4X3_ADD2 · MVD CoordinationView · 4,5 MB

DESCARGAR ↗