

WORKSHOP BIM + IA • MÉTODO TBC • ENTREGABLE HITO 01

Habitáculo para ciclistas

Pausa Maule es un punto de descanso para ciclistas de ruta en el corredor vitivinícola de Talca, Región del Maule. Un vacío central bajo una retícula de nueve cuadrantes ordena masa, umbral y paisaje.

- Autor – Matías Álvarez C.
- Curso – Workshop BIM + IA
- Proyecto – Habitáculo Pausa Maule
- Ubicación – Talca, Región del Maule, Chile
- Programa – 9 recintos, 79.44 m² totales
- Modelo – HAB_ARQ_MODELO_R01.rvt

3×3

RETÍCULA NINE-SQUARE

9

RECINTOS MODELADOS

79.44


M² ÁREA TOTAL

12


PROVEEDORES VERIFICADOS

01 El partido

04_Laminas/Partido_Pausa_Maule.pdf

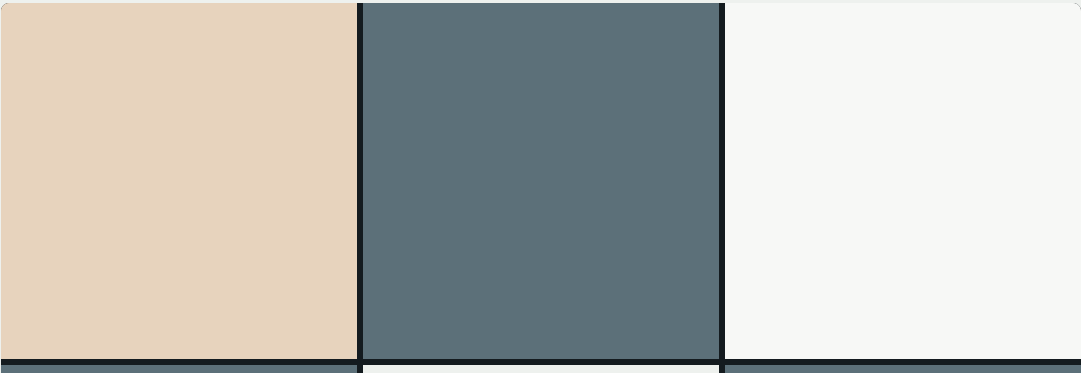

El partido organiza el programa sobre una retícula de nueve cuadrantes: cuatro llenos estructurales (madera + quinchá) sostienen un vacío central, el patio, donde crece un árbol a través de la cubierta.

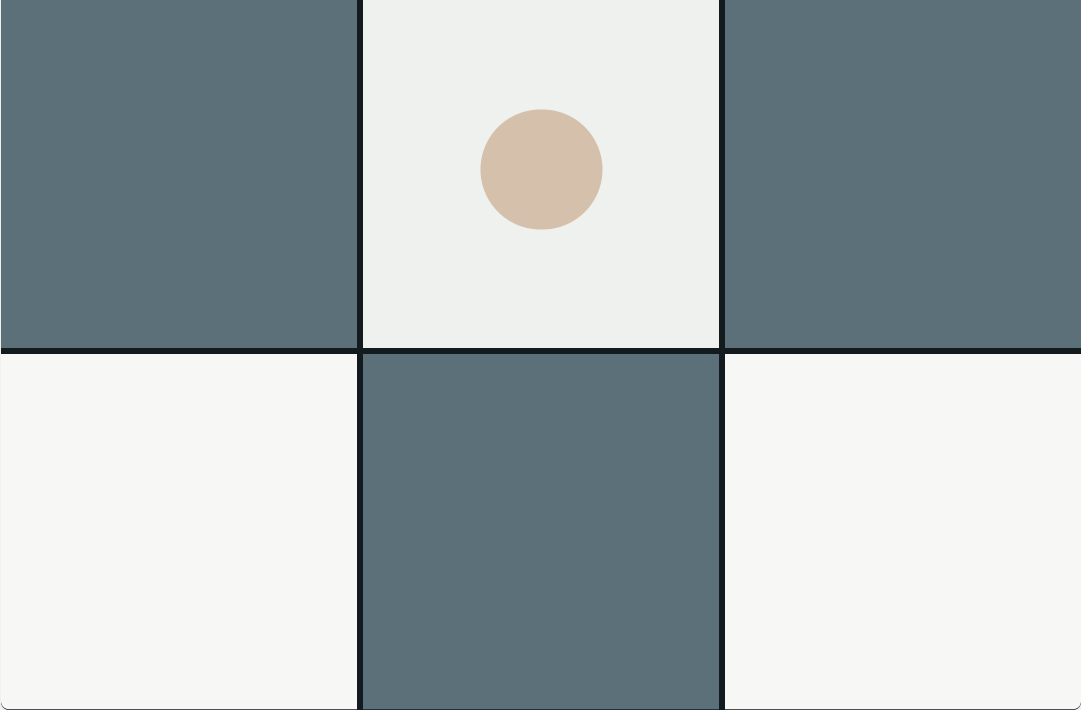

- **Acceso principal** resuelto en el cuadrante superior izquierdo, sin cruzar muros cortina.
- Los **muros cortina** perimetrales quedaron libres de accesos tras la corrección del partido: los recorridos pasan entre los llenos, no a través de los paños vidriados.
- El **patio central** es el umbral entre paisaje y recinto — ahí ocurre la pausa.

PDF

Lámina del Partido

04_Laminas · llenos, vacíos, accesos y volumen principal

ABRIR

02 Referentes

01_Referentes/Referentes_Aires_Mateus_Habitaculo_3x3.pdf

01

Masa

02

Vacío

03

Umbral

04

Paisaje

05

Recorrido

Referentes Aires Mateus — contraste nine-square

5 precedentes contrastados contra el partido de Pausa Maule · 9 páginas

AIRES MATEUS

Referentes existentes

Masa, vacío, umbral, luz y paisaje como herramientas para proyectar una pausa ciclista.

Arquitectura · Selección conceptual






Cabanas no Rio · Comporta, 2013 · Fot. Nelson Garrido

[Abrir en pestaña nueva ↗](#)

03 Imágenes del proyecto

06_Imagenes · renders









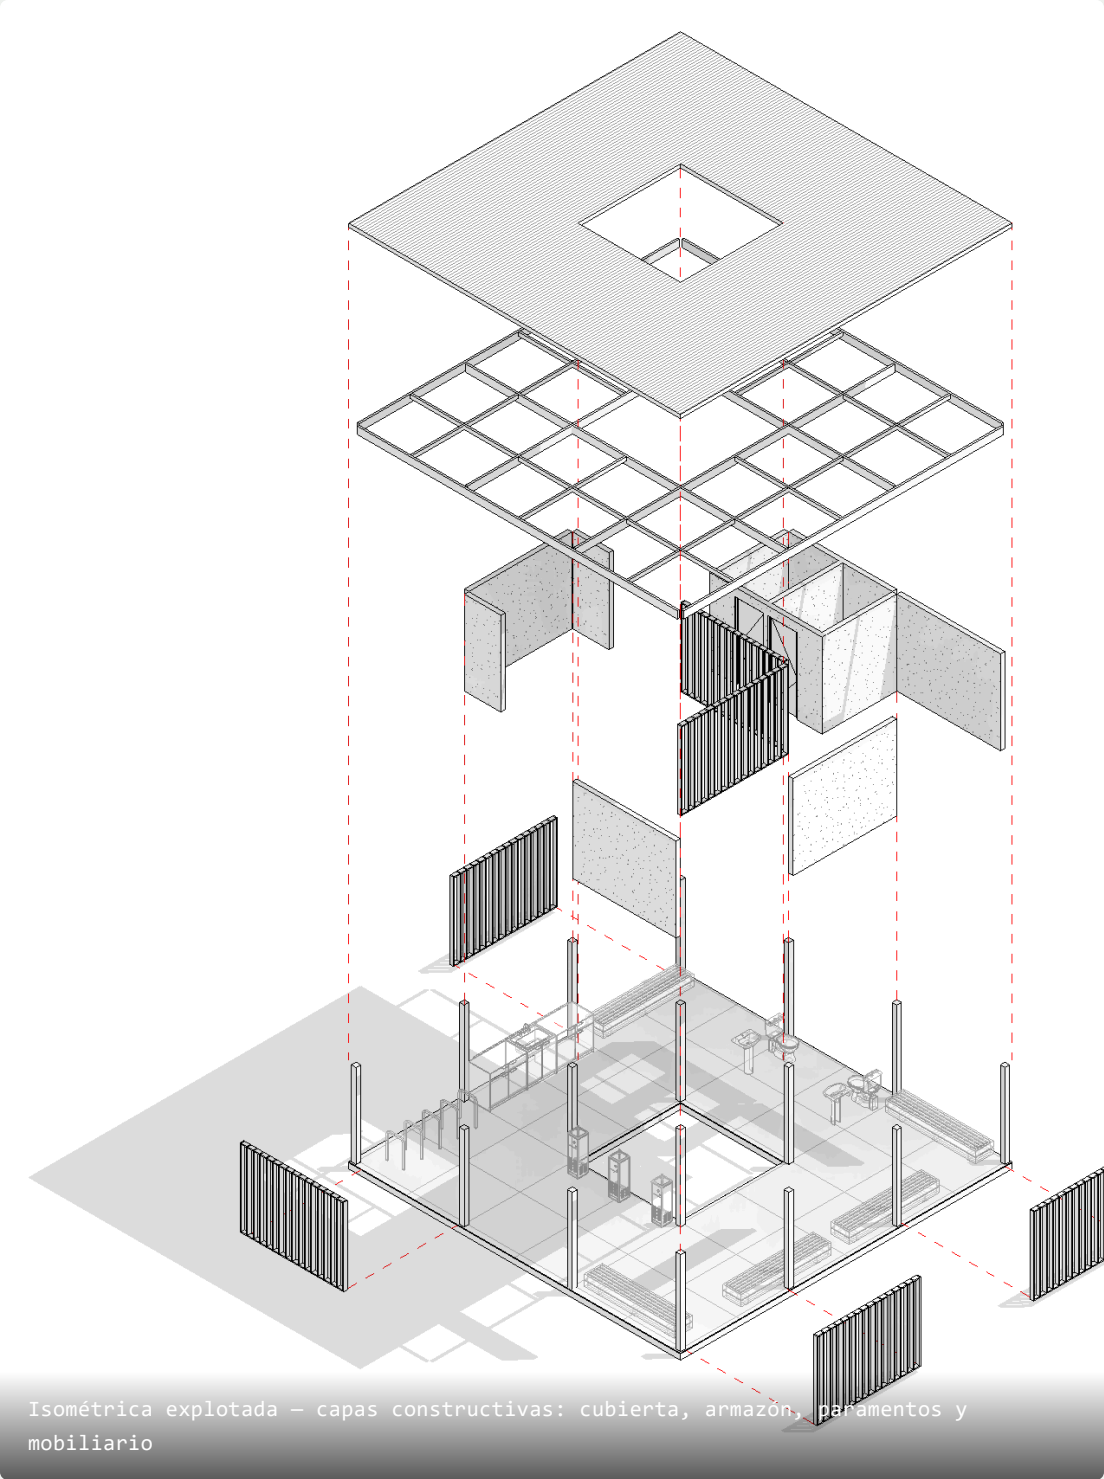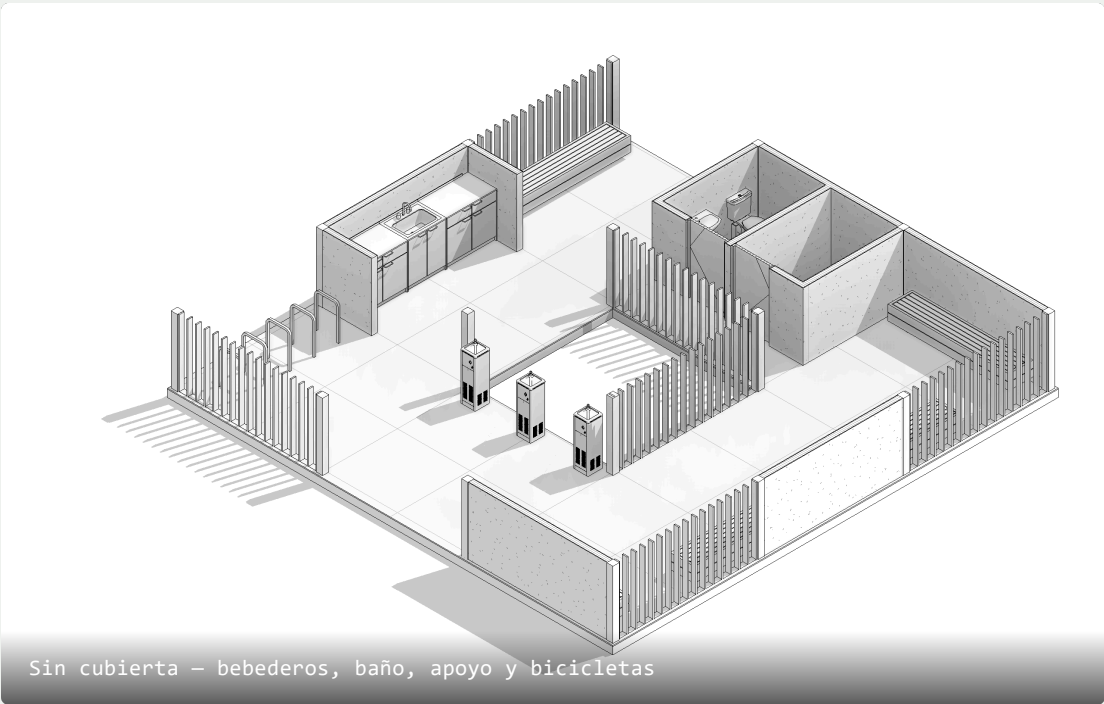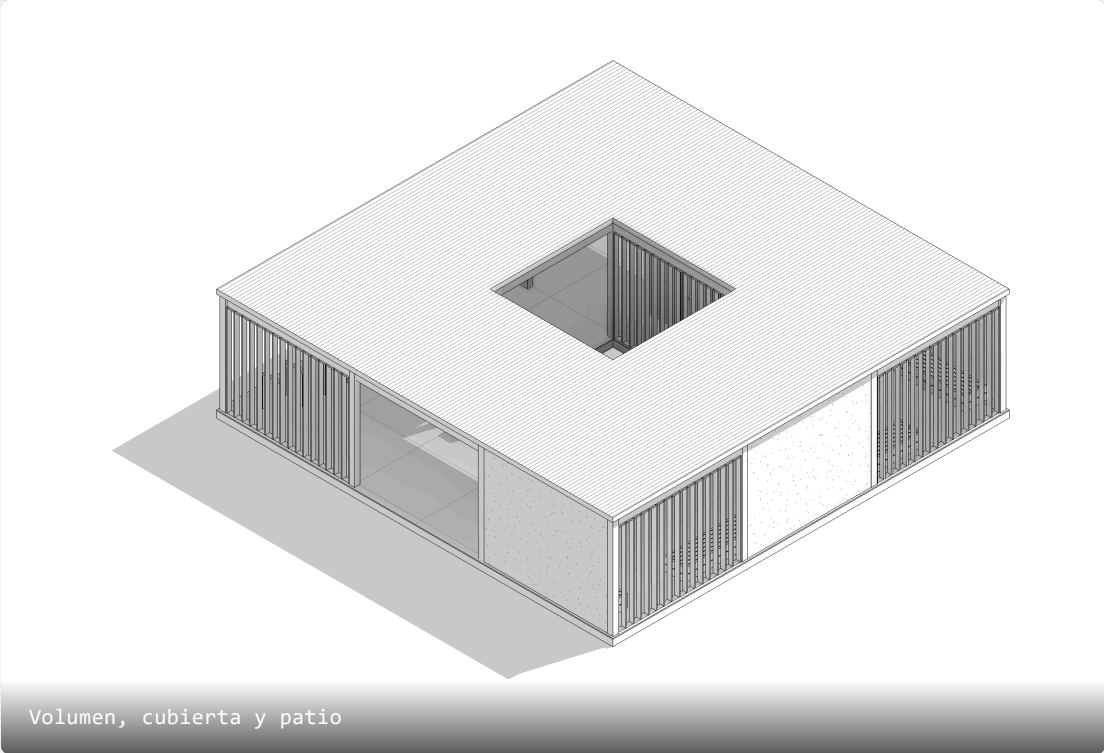

04 Láminas

Lámina A101 — Planimetría general

planta, 4 elevaciones, 3 cortes e isométricas · 1:50

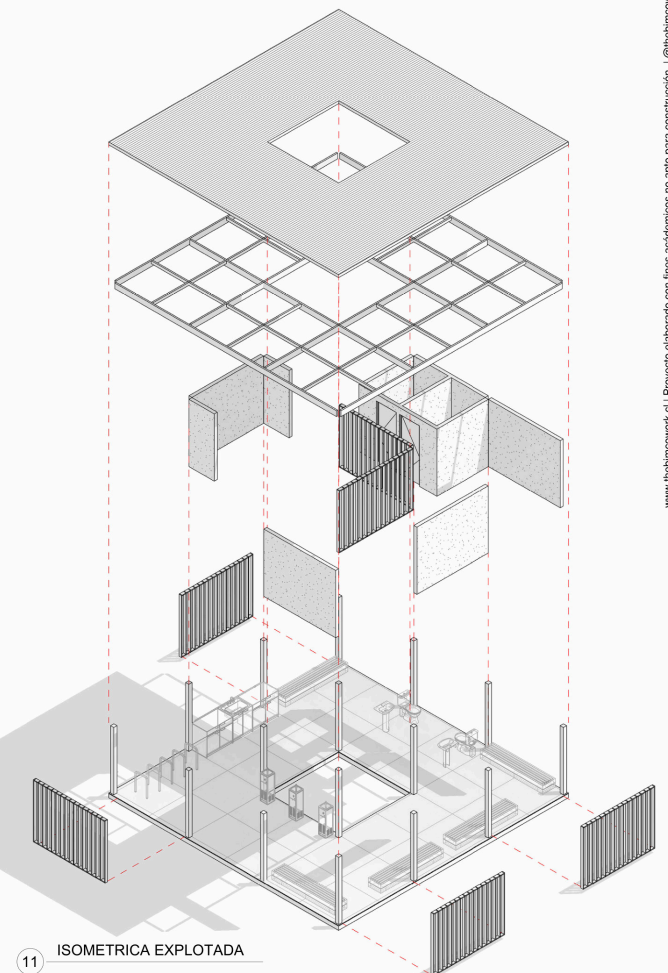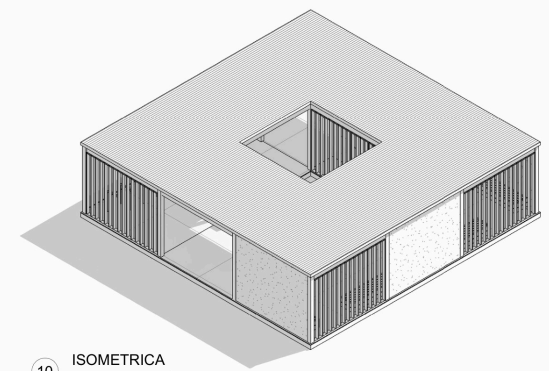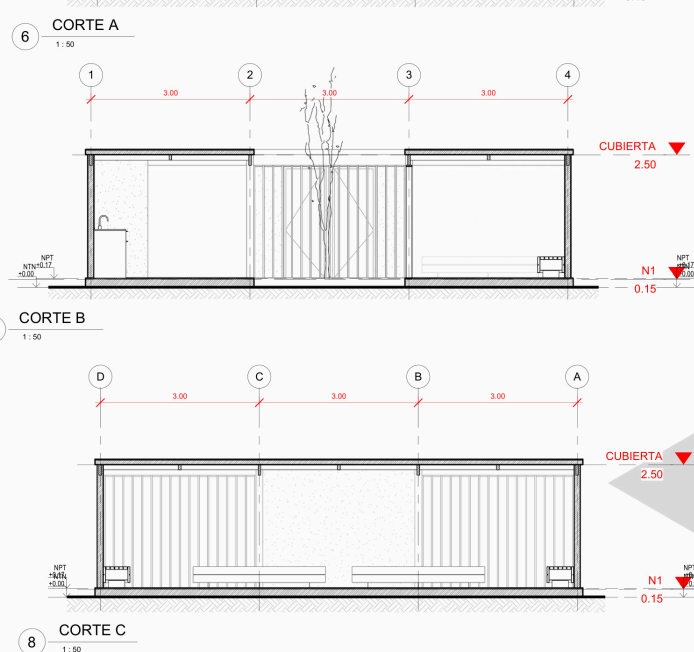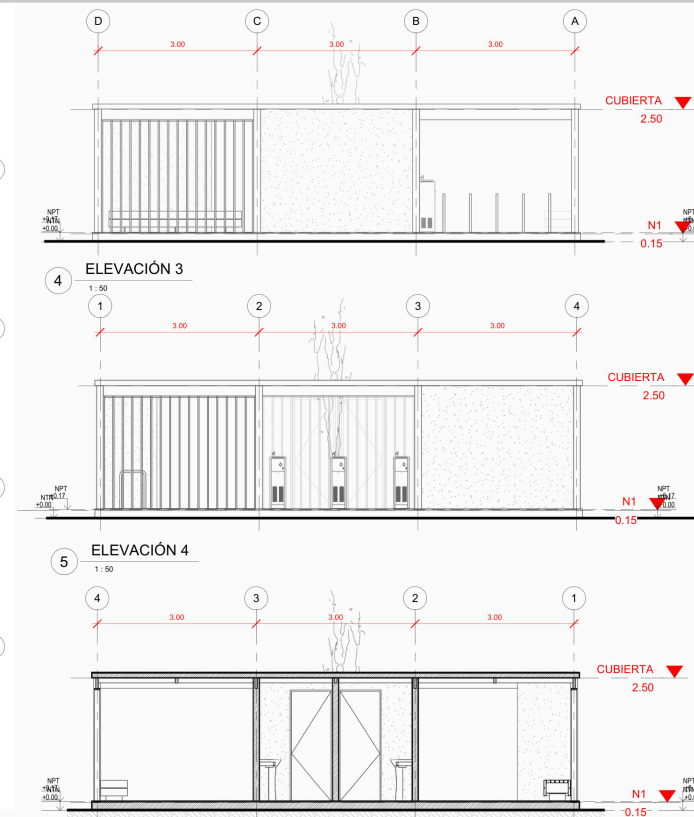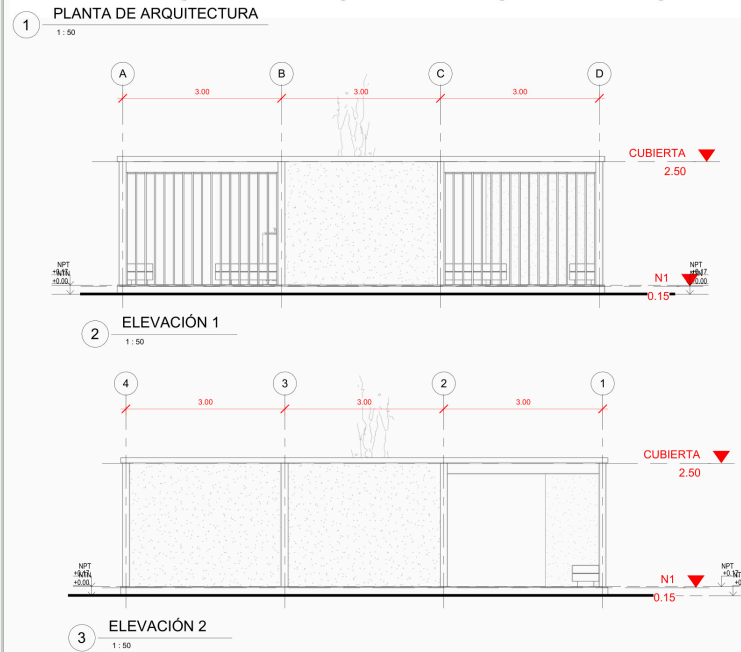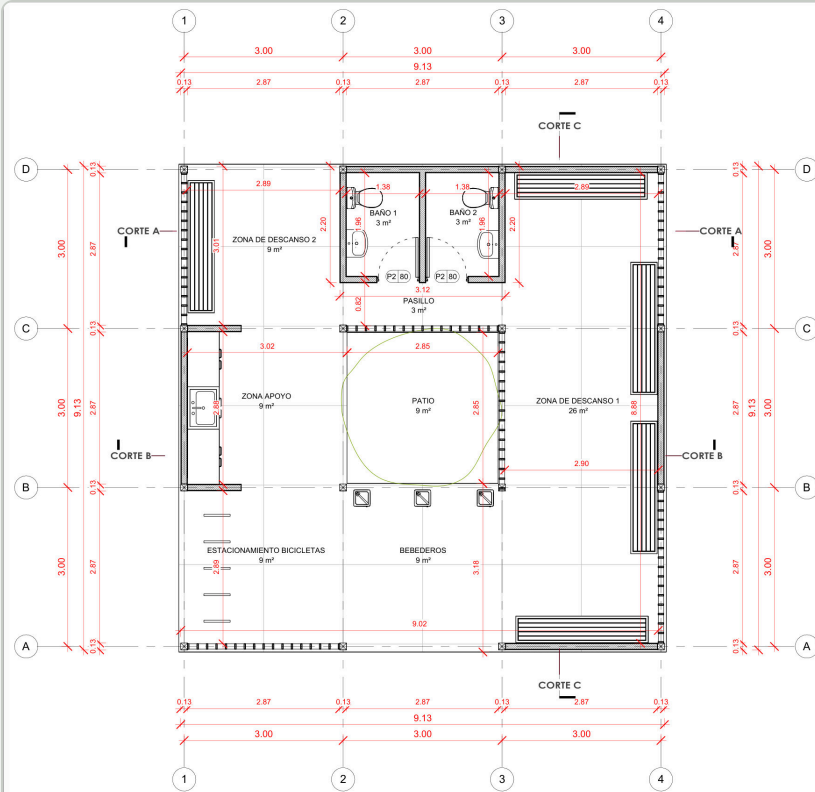

Quincha MURO_EXT_QUINCHA_12cm Sistema quincha liviana húmeda — Corporación Protierra Chile, red MINVU/DITEC.	Pino Radiata MT_PINO RADIATA · MLE 20c Pilares glulam Hilam MLE, almacén dimensionado y paneles Arauco Machihembrado.	Zincalum MT_PLANCHA ONDULADA ZINCALUM Plancha ondulada sobre estructura de madera — Cubiertas Nacionales CN-1020.
---	--	--

06 Documentos técnicos

03_Documentos_Tecnicos

PDF Reglas de Trabajo BIM Resumen del Estándar PlanBIM Chile aplicado a Pausa Maule · Paso 01 ABRIR	PDF Especificación Técnica Materiales, fichas de fabricante, categorías cerradas DOCX ABRIR
PDF PEB Preliminar Plan de Ejecución BIM — etapa preliminar DOCX ABRIR	XLS PEB Completado 9 recintos, nombre/número/nivel/área/perímetro XLSX ABRIR
PDF Tabla NDI Niveles de Desarrollo de la Información ABRIR	PDF Parámetros Compartidos Grupo NDI2 — parámetros compartidos del proyecto ABRIR

07 Proveedores

02_Proveedores/Fichas_Proveedores_Pausa_Maule.xlsx

XLS Fichas de Proveedores 12 proveedores verificados · contacto, sitio web, ficha técnica ABRIR

ELEMENTO	EMPRESA	PRODUCTO	SITIO WEB
----------	---------	----------	-----------

Muro / Quincha	Corporación Protierra Chile	Sistema Quincha Liviana Húmeda	redproterra.org
Cubierta	Cubiertas Nacionales	Panel Ondulado CN-1020	cubiertasnacionales.cl
Radier	Melón	Hormigón con Fibra	melon.cl
Radier pulido	Sika Chile	Sikafloor-3 QuartzTop	chl.sika.com
Pilar estructural	Arauco — Hílam	Madera Laminada Encolada MLE 20c	arauco.com/hilam
Armazón	Arauco — MSD	Construcción Premium MSD	arauco.com
Muro cortina — montante	Arauco — MSD	Pino Radiata Cepillado	arauco.com
Muro cortina — panel	Arauco	MSD Revestimiento Machihembrado	arauco.com/chile
Puerta	Moldupanel (Puertas Chile)	Puerta Pino Radiata Italia 80×210	puertaschile.cl
Herrajes	Häfele (vía El Carpintero)	Bisagras y cerraduras	elcarpintero.cl
Sanitarios	Fanaloza	New Valencia a Muro / Lavamanos Ciro	fanaloza.cl
Abastecimiento local	Sodimac / Construmart Talca	Distribución general	sodimac.cl

Descargar documentos e imágenes

Referentes, proveedores, documentos técnicos, láminas e imágenes — no incluye el modelo Revit (ver punto 08)

↓ DESCARGAR TODO (.RAR, 20 MB)

08 Modelo Revit

HAB_ARQ_MODELO_R01.RVT

7 199	939	55	70	46	5
ELEMENTOS TOTALES	TIPOS	FAMILIAS	CATEGORÍAS	VISTAS	NIVELES

RVT

HAB_ARQ_MODELO_R01.rvt

Modelo BIM del habitáculo Pausa Maule · 214 MB

DESCARGAR

