
PARTIDO — PAUSA MAULE

RETÍCULA 3×3 · 9,00 × 9,00 M · MÓDULO 3,00 M · HABITÁCULO CICLISTA · TALCA, REGIÓN DEL MAULE

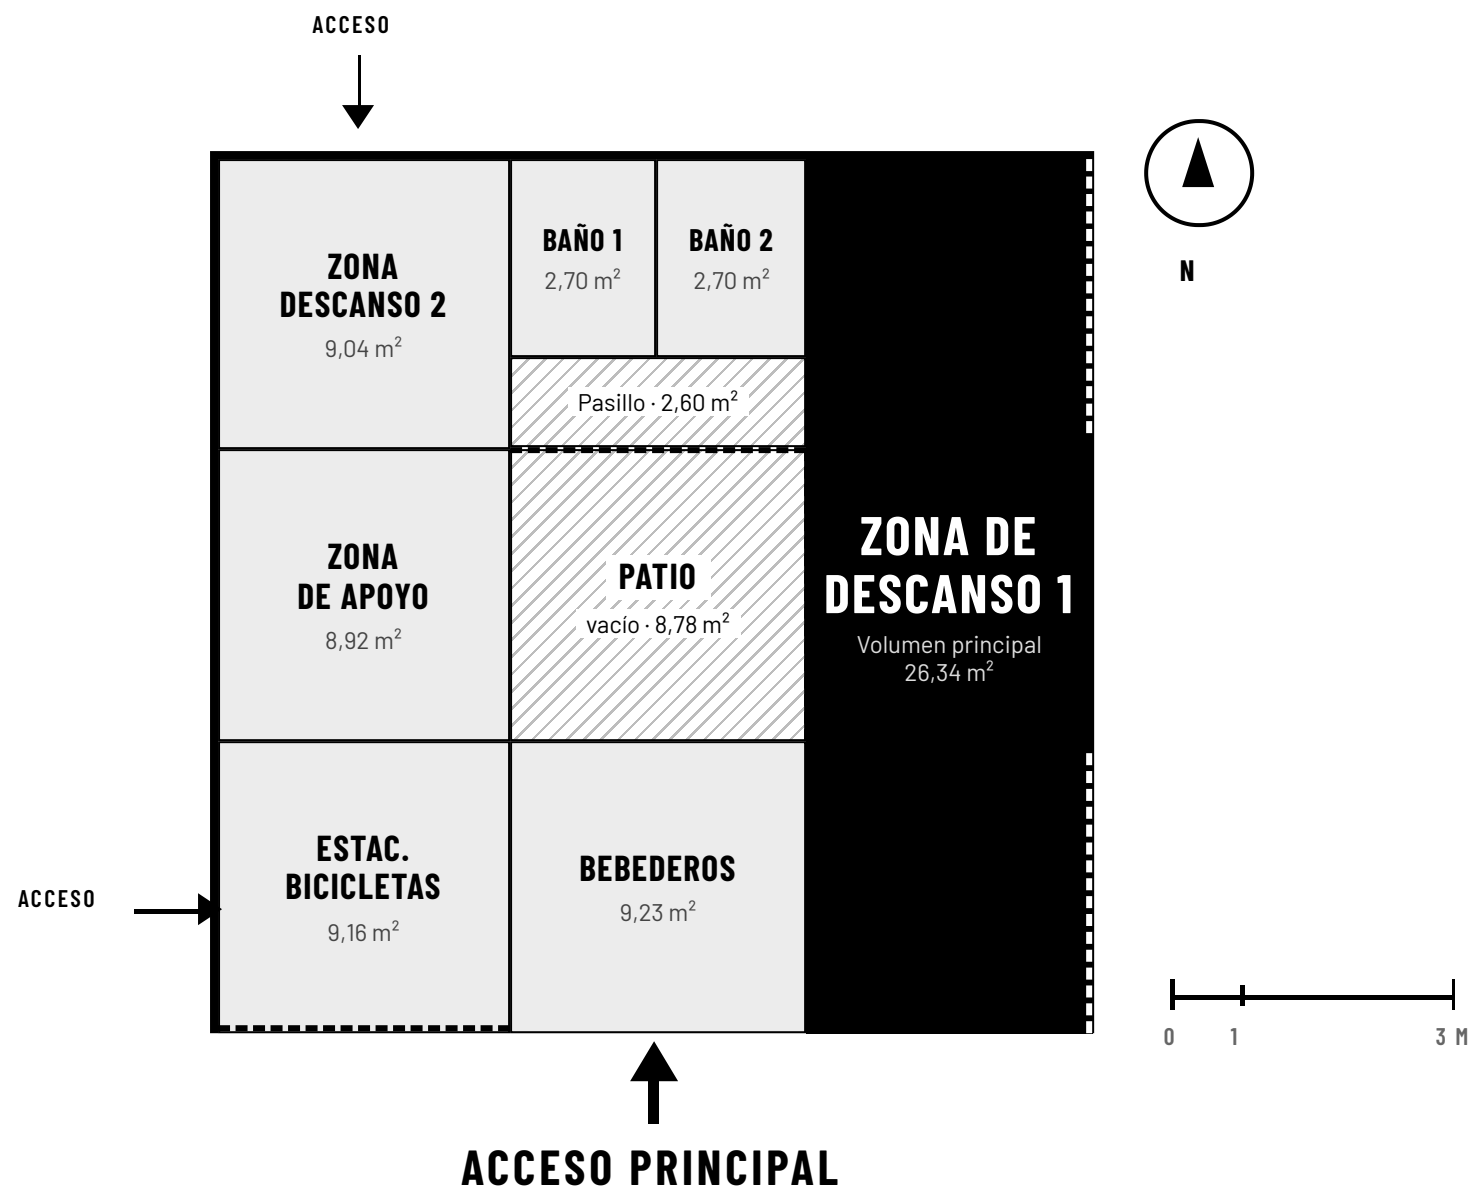

Planta esquemática del partido sobre la retícula 3×3 (módulo 3 m). Celda llena = recinto; trama diagonal = vacío (patio); línea discontinua = muro cortina de celosía de pino radiata (sin vidrio); flecha = acceso. Geometría abstraída a la grilla — no es el plano constructivo.

LEYENDA

- Recinto lleno
- Volumen principal
- Vacío (patio)
- Muro cortina de celosía de pino radiata
- → Acceso (principal y secundarios)

PROGRAMA · 9 RECINTOS

1	**Zona Descanso 2**	9,04 m²
2	**Zona de Apoyo**	8,92 m²
3	**Estac. Bicicletas**	9,16 m²
4	**Baño 1**	2,70 m²
5	**Baño 2**	2,70 m²
6	**Pasillo**	2,60 m²
7	**Bebederos**	9,23 m²
8	**Patio**	8,78 m²
9	**Zona Descanso 1**	26,34 m²
	Área total	**79,45 m²**

LECTURA DEL PARTIDO

El vacío se aloja en la celda central — el patio clásico del nine-square, abrazado por el paisaje de la Región del Maule. La columna derecha completa se funde en un solo volumen: **Zona Descanso 1**, la pieza dominante, y junto con las demás instancias conforma una única pausa continua. El acceso principal entra por Bebederos, en el centro de la fachada sur; dos accesos secundarios —por el lateral izquierdo de Estacionamiento Bicicletas y por arriba de Zona Descanso 2— permiten un recorrido no lineal, coherente con un ciclista que llega por distintos senderos. Los muros cortina (6 paños) son celosías de montantes de pino radiata, sin vidrio: filtran luz y aire, pero no son ingresos.

CONTRASTE CON REFERENTES · AIRES MATEUS

REFERENTE	OPERACIÓN	LECCIÓN	ESTADO EN PAUSA MAULE
01 · Cabanas no Rio	Masa	Pieza mínima, un solo material reúne estructura y cerramiento.	**Resuelto** — el conjunto se piensa como una pieza mínima que se constituye como un continuo: varias instancias (Descanso 1, Descanso 2, Apoyo, servicios) conforman una sola pausa, no piezas autónomas.
02 · Casa en Leiria	Vacío	Los recintos dependen del patio para luz y orientación.	**Resuelto** — la cubierta tiene una abertura sobre el patio central, donde crece un árbol, que entrega luz cenital directa. Además el cerramiento es muy permeable: los muros cortina de celosía de pino radiata (montantes de 19×90 mm, sin paneles) dejan entrar luz y aire desde varias direcciones, no solo desde el patio.
03 · Pa.te.os	Umbral	La apertura de acceso tiene profundidad: es una estancia, no un paso.	**Parcial** — se identificaron 3 accesos (principal en Bebederos, secundarios en Estacionamiento Bicicletas y Zona Descanso 2) en vez de uno solo. Falta darle profundidad habitable a cada umbral, no solo multiplicarlo.
04 · Casa en Monsaraz	Paisaje	El centro se protege sin aislarse del horizonte.	**Resuelto** — el proyecto se organiza en torno al patio, y este a su vez es abrazado por el paisaje de la Región del Maule: el centro protegido se relaciona con el horizonte a través del vacío.
05 · Nursing Home	Recorrido	Acceso y patio forman una secuencia breve de sombra, pausa y encuentro.	**Resuelto por otra vía** — no hay una secuencia lineal única, sino un recorrido no lineal con varios accesos posibles, coherente con un ciclista que llega desde direcciones distintas.

Diagrama nine-square del propio referente (pág. 8): propone Descanso en L (3 celdas: sup. izq., sup. centro, media izq.), Apoyo en columna derecha (2 celdas) y una fila inferior Acceso–Umbral–Bicicletas. Pausa Maule diverge en tres puntos: **Descanso se partió en dos piezas separadas** (Descanso 1 en columna completa + Descanso 2 aislado) en vez de una L continua; **Apoyo quedó en una sola celda** en vez de dos; y **Bicicletas se ubicó en la esquina suroeste** en vez de la sureste del referente — decisiones de sitio, no errores.