TALCA / REGIÓN DEL MAULE — CHILE

VISOR IFC ↗ ☾

# PM
# PAUSA MAULE

PARTIDO REFERENTES IMÁGENES LÁMINAS MATERIALIDAD DOCUMENTOS PROVEEDORES MODELO






HABITÁCULO PARA CICLISTAS

# UN PUNTO DE DESCANSO EN EL CORREDOR VITIVINÍCOLA DE TALCA.

Pausa Maule es un punto de descanso para ciclistas de ruta en el corredor vitivinícola de Talca, Región del Maule. Un vacío central bajo una retícula de nueve cuadrantes ordena masa, umbral y paisaje.


| | |
|---|---|
| **AUTOR** | Matías Alvarez C. |
| **REDES** | Instagram @matias_arq_ ↗ · LinkedIn ↗ |
| **CURSO** | Workshop BIM + IA · creado por The BIM Cowork ↗ |
| **PROYECTO** | Habitáculo Pausa Maule |
| **UBICACIÓN** | Talca, Región del Maule |

| | |
|---|---|
| **PROGRAMA** | 9 recintos, 79.45 m² totales |
| **MODELO** | HAB_ARQ_MODELO_R01.rvt |

**3×3**
RETÍCULA NINE-SQUARE

**9**
RECINTOS MODELADOS


**79.45**
M² ÁREA TOTAL

**16**
PROVEEDORES VERIFICADOS

01

# EL PARTIDO

CONCEPTO SOBRE LA GRILLA 3×3

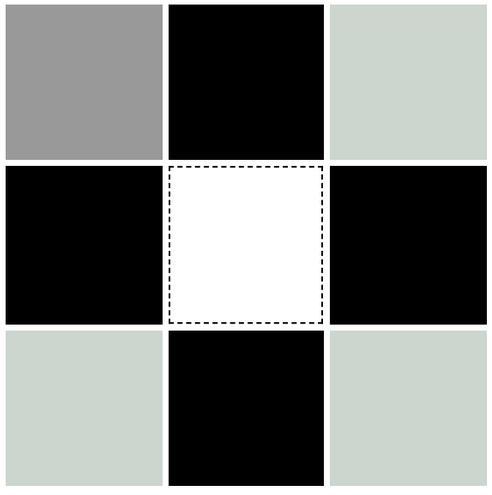

El partido organiza el programa sobre una retícula de nueve cuadrantes: cuatro llenos estructurales (madera + quincha) sostienen un vacío central, el patio, donde crece un árbol a través de la cubierta.

- **Acceso principal** resuelto en el cuadrante superior izquierdo, sin cruzar muros cortina.
- Los **muros cortina** perimetrales quedaron libres de accesos tras la corrección del partido: los recorridos pasan entre los llenos, no a través de los paños vidriados.
- El **patio central** es el umbral entre paisaje y recinto — ahí ocurre la pausa.

LÁMINA DEL PARTIDO (PDF) ↗

llenos, vacíos, accesos y volumen principal

02

# REFERENTES

5 PRECEDENTES DE AIRES MATEUS

01
## MASA

02
## VACÍO

03
## UMBRAL

04
## PAISAJE

05
## RECORRIDO

Referentes Aires Mateus — contraste nine-square · 5 precedentes contrastados contra el partido de Pausa Maule · selección de 4 láminas, PDF completo de 9 páginas

PAUSA MAULE · HABITÁCULO 3×3

# AIRES MATEUS

## Referentes existentes

Masa, vacío, umbral, luz y paisaje como herramientas para proyectar una pausa ciclista.



Cabanas no Rio · Comporta, 2013 · Fot. Nelson Garrido

ARQUITECTURA · SELECCIÓN CONCEPTUAL

01

05

## EL MURO TAMBIÉN CONSTRUYE EL UMBRAL



Pa.te.os · Melides, 2020 · Fot. João Guimarães

**03 · PA.TE.OS**

Muros continuos delimitan recintos y, al ser atravesados, producen negativos profundos que encuadran el paisaje.

**LÍMITE**

El muro define una habitación incluso cuando no completa un volumen.

**UMBRAL**

La abertura tiene profundidad suficiente para convertirse en estancia.

**PAISAJE**

El vacío dirige la mirada y relaciona arquitectura con vegetación.

**APLICACIÓN**

Convertir la celda de acceso en una pausa cubierta, no en un simple paso.

02



06

## DESAPARECER PARA CONSTRUIR UN CENTRO PROTEGIDO





Casa en Monsaraz · Alentejo, 2018 · Fot. João Guimarães

**04 · CASA EN MONSARAZ**

El terreno oculta la casa; patios circulares y una abertura superior revelan su organización.

**APLICACIÓN**

**Proteger el centro sin aislarlo del horizonte.**

03



07

## EL RECORRIDO ARTICULA INTIMIDAD, ENCUENTRO Y PAISAJE





Nursing Home · Alcácer do Sal, 2010 · Fot. Fernando Guerra / FG+SG

**05 · NURSING HOME**

Unidades independientes forman un cuerpo continuo; los retranqueos median entre intimidad y vida colectiva.

**APLICACIÓN**

**Hacer del acceso y el patio una secuencia breve de sombra, pausa y encuentro.**

04



ABRIR PDF COMPLETO ↗

# IMÁGENES DEL PROYECTO

RENDERS E ISOMÉTRICAS



VISTA AÉREA — EL PATIO Y EL ÁRBOL ATRAVESANDO LA CUBIERTA



INTERIOR — BEBEDEROS Y DESCANSO



INTERIOR — UMBRAL HACIA EL VALLE



EXTERIOR — EL HABITÁCULO ENTRE VIÑEDOS




DEL UMBRAL AL VIÑEDO — MURO DE QUINCHA Y BANCA





INTERIOR — BANCA DE DESCANSO Y CELOSÍA

## VISTAS ISOMÉTRICAS

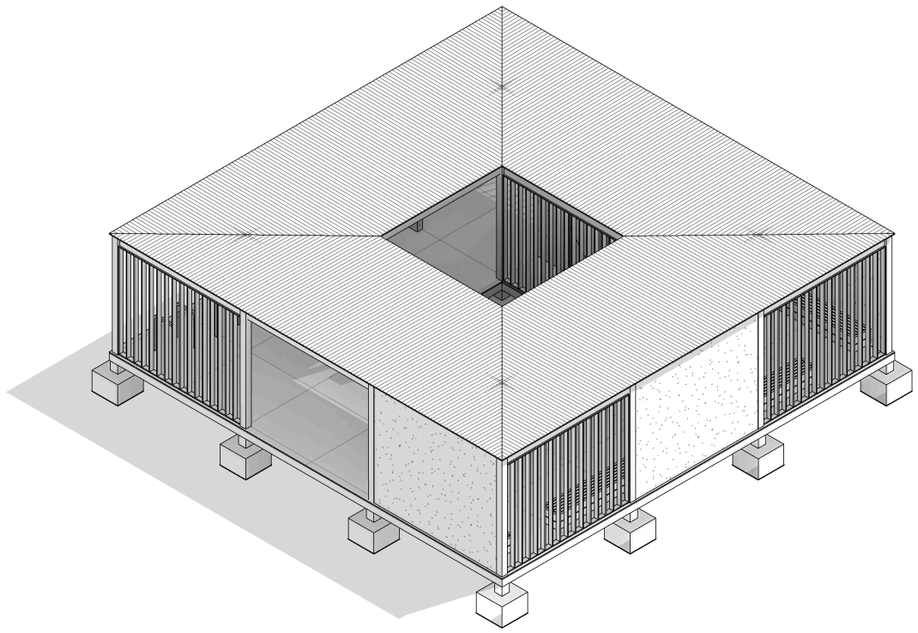

Volumen, cubierta y patio

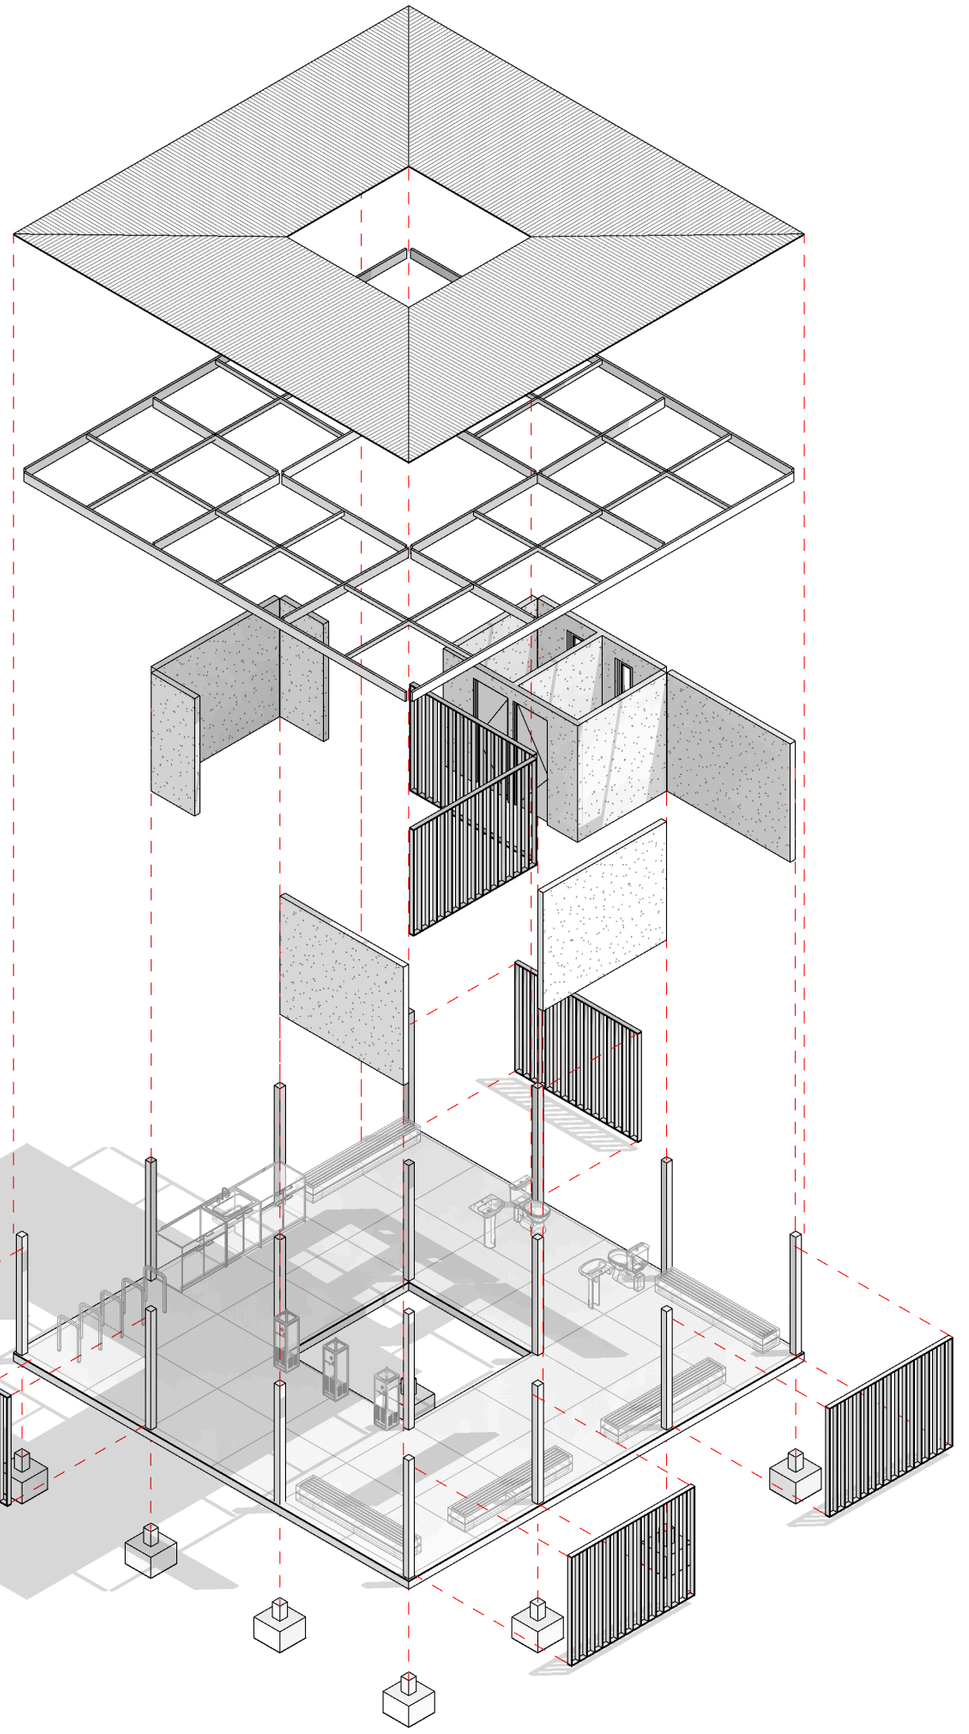

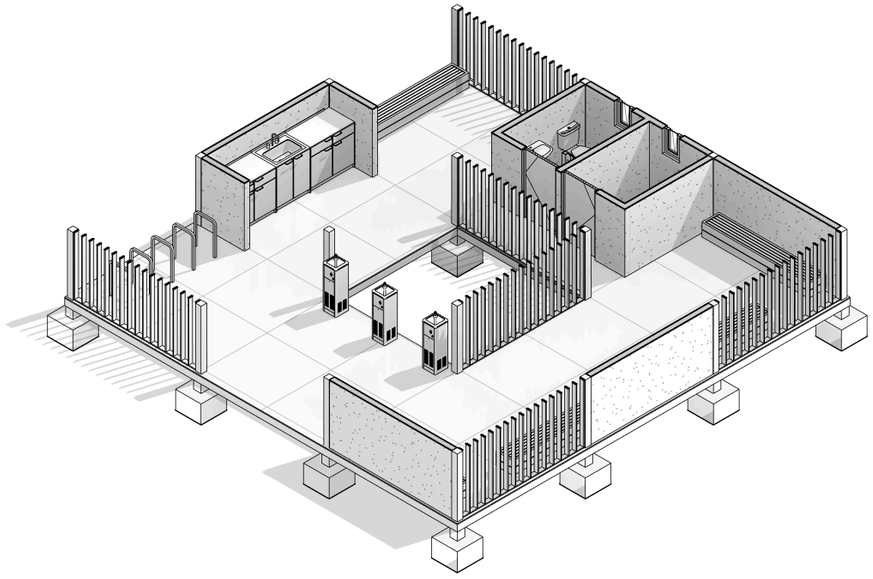

Sin cubierta — bebederos, baño, apoyo y bicicletas

Isométrica explotada — capas constructivas: cubierta, armazón, paramentos y mobiliario

## VIDEO




Exterior — el habitáculo entre viñedos


04

# LÁMINAS


PLANIMETRÍA TÉCNICA

Lámina A101 — Planimetría general · planta, 4 elevaciones, 3 cortes, cubierta, superficies, isométricas y tablas de superficie · 1:50


+ − AJUSTAR PANTALLA COMPLETA ABRIR PDF ↗

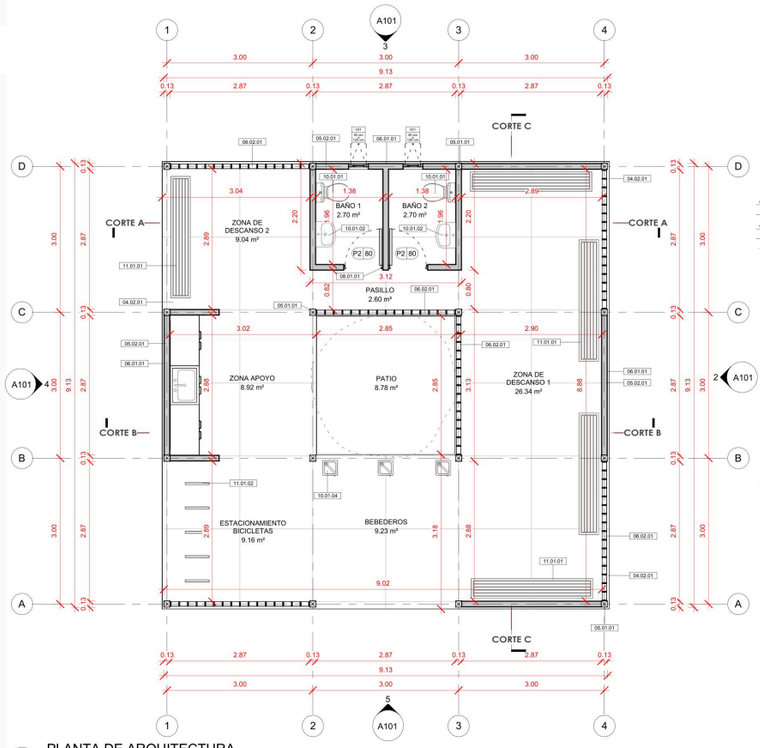



1 PLANTA DE ARQUITECTURA
1 : 50

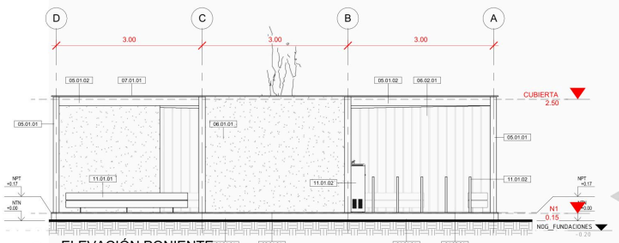



4 ELEVACIÓN PONIENTE
1 : 50

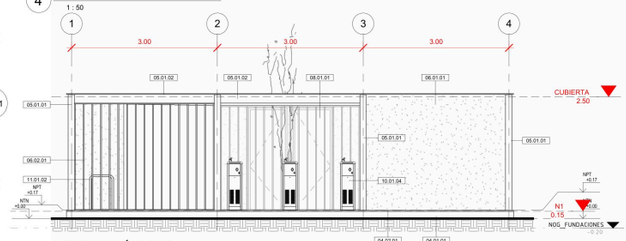



5 ELEVACIÓN SUR
1 : 50

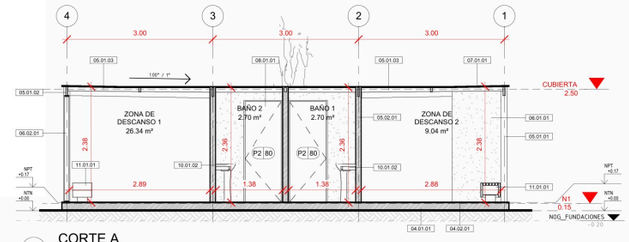



6 CORTE A
1 : 50

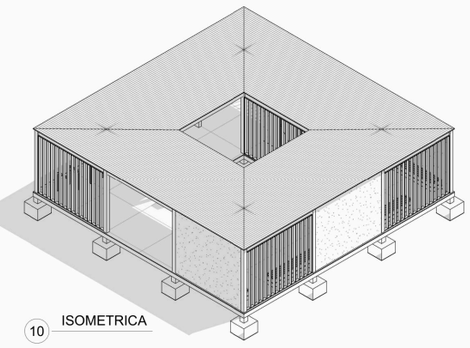


10 ISOMETRICA

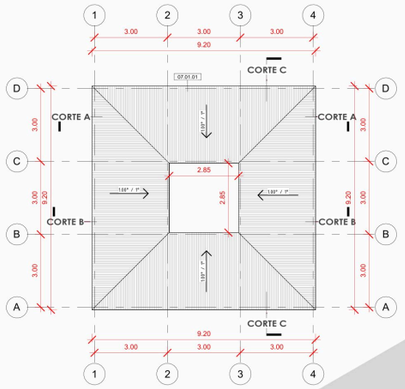



7 CUBIERTA
1 : 100

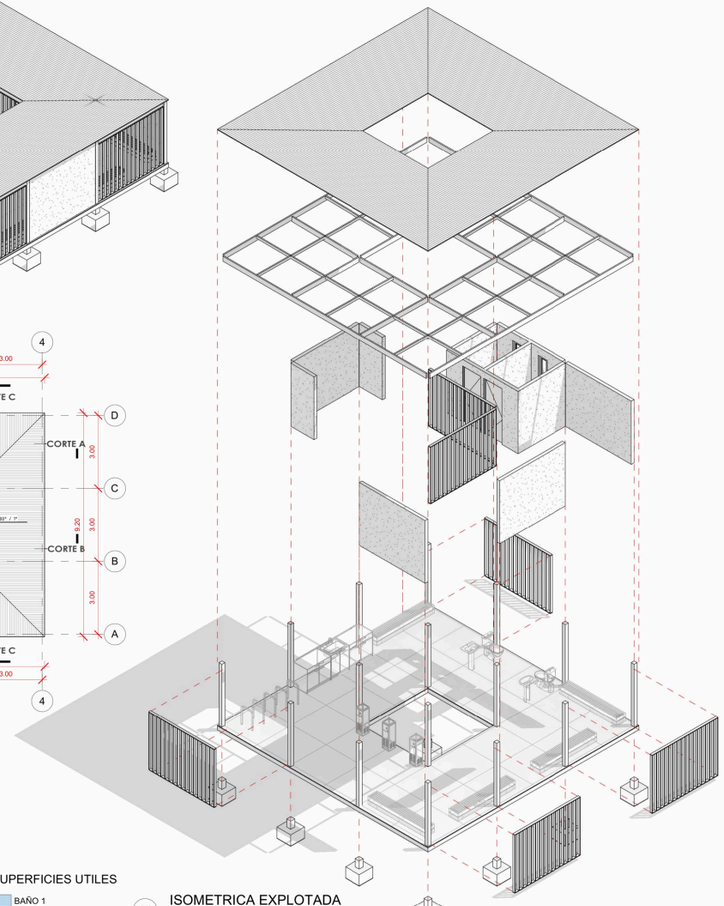


11 ISOMETRICA EXPLOTADA

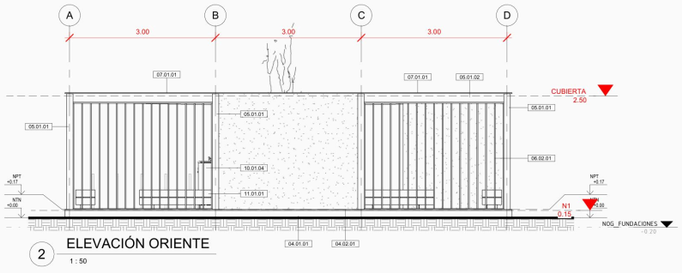


2 ELEVACIÓN ORIENTE
1 : 50

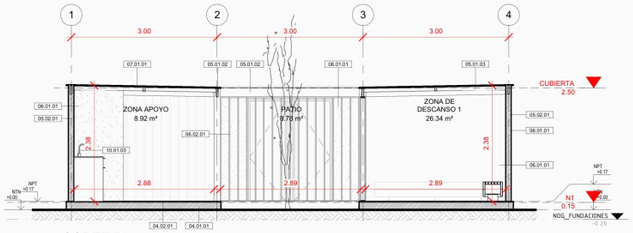


9 CORTE B
1 : 50

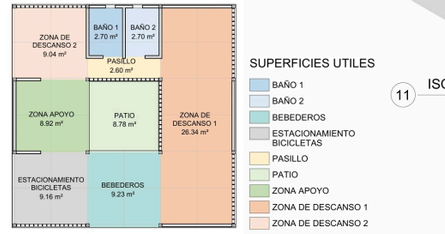


12 PLANTA DE SUPERFICIES
1 : 100

SUPERFICIES UTILES

- BAÑO 1
- BAÑO 2
- BEBEDEROS
- ESTACIONAMIENTO BICICLETAS
- PASILLO
- PATIO
- ZONA APOYO
- ZONA DE DESCANSO 1
- ZONA DE DESCANSO 2

DATA ESPACIAL POR RECINTO - EETT

| NUMERO | RECINTO | DEPARTAMENTO | NIVEL | SUPERFICIE | PERIMETRO | VOLUMEN |
|---|---|---|---|---|---|---|
| 01 | BAÑO 1 | Servicios Higiénicos | NPT | 2.70 m² | 6.67 | 6.29 m³ |
| 02 | BAÑO 2 | Servicios Higiénicos | NPT | 2.70 m² | 6.67 | 6.29 m³ |


Arrastra para mover · haz clic y usa la rueda para acercar · doble clic para ampliar

www.thebimcowork.cl | Proyecto elaborado con fines académicos no apto para construcción | @thebimcowork


05


# MATERIALIDAD


VERIFICADA CONTRA FICHAS DE FABRICANTE

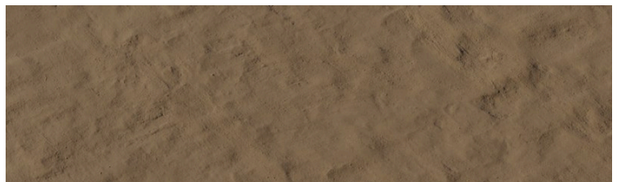



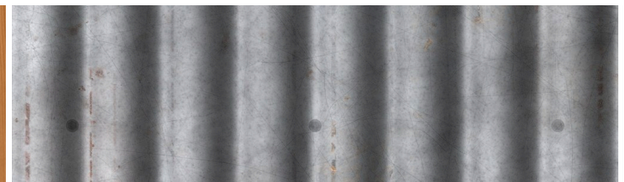

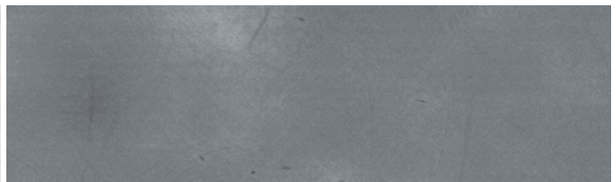

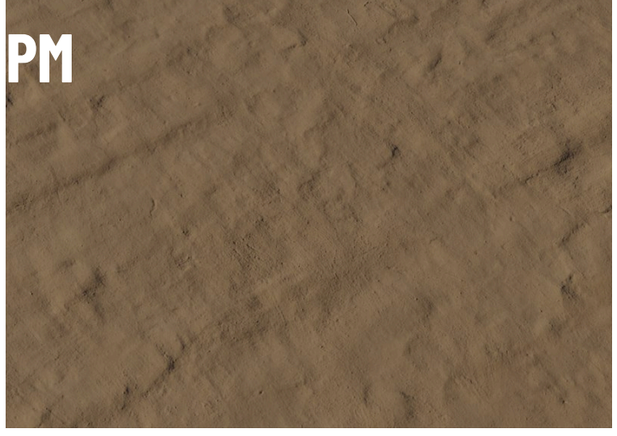


## QUINCHA

MURO_EXT_QUINCHA_12cm

Sistema quincha liviana húmeda — Corporación Protierra Chile, red MINVU/DITEC.

VER ELEMENTO ↗




## PINO RADIATA

MT_PINO RADIATA · MLE 20c

Pilares glulam Hilam MLE, armazón dimensionado y montantes Arauco. Los paneles del muro cortina quedan vacíos (celosía).

VER ELEMENTO ↗

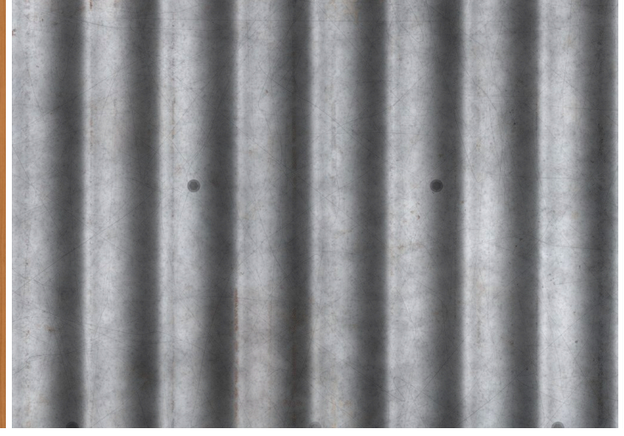


## ZINCALUM

MT_PLANCHA ONDULADA ZINCALUM

Plancha ondulada sobre estructura de madera — Cubiertas Nacionales CN-1020.

VER ELEMENTO ↗

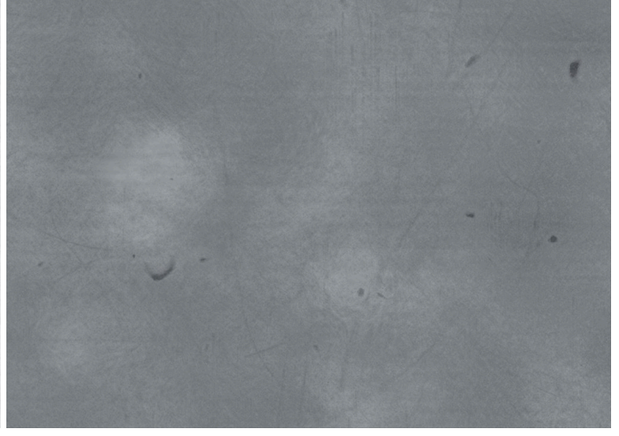

## HORMIGÓN

PAV_INT_HORMIGON PULIDO_2cm

Radier con fibra Melón + endurecedor superficial Sikafloor-3 QuartzTop. El mismo hormigón armado forma las 16 zapatas aisladas bajo los pilares.

VER ELEMENTO ↗

06

# DOCUMENTOS TÉCNICOS

REGLAS, PEB, NDI Y PARÁMETROS

## REGLAS DE TRABAJO BIM

Resumen del Estándar PlanBIM Chile aplicado a Pausa Maule · Paso 01

PDF ↗

## ESPECIFICACIÓN TÉCNICA

Materiales, fichas de fabricante, categorías cerradas

PDF ↗

## PEB PRELIMINAR

Plan de Ejecución BIM — etapa preliminar

PDF ↗

## PEB COMPLETADO

Tabla NDI por categoría y 9 recintos (nombre, número, nivel, área, perímetro)

PDF ↗

## TABLA NDI

Niveles de Desarrollo de la Información

PDF ↗

## PARÁMETROS COMPARTIDOS

Grupo NDI2 — parámetros compartidos del proyecto

PDF ↗

## NOMENCLATURA IFC

Nombre en la vida real, clase IFC y nombre en Revit de cada entidad del modelo

PDF ↗

## TABLAS DEL MODELO

Tablas de planificación exportadas desde Revit (20 hojas)

PDF ↗

## REPORTE DE CUMPLIMIENTO BEP

Verificación del modelo contra el Plan de Ejecución BIM

PDF ↗

07

# PROVEEDORES

16 PROVEEDORES VERIFICADOS

## FICHAS DE PROVEEDORES

16 proveedores verificados · contacto, sitio web, ficha técnica

XLSX ↓

| ELEMENTO | EMPRESA | PRODUCTO | SITIO WEB | FICHA TÉCNICA |
|---|---|---|---|---|
| Muro / Quincha | Corporación Protierra Chile | Sistema Quincha Liviana Húmeda | redproterra.org | FICHA TÉCNICA ↗ |

| | | | | |
|---|---|---|---|---|
| Cubierta | Cubiertas Nacionales | Panel Ondulado CN-1020 | cubiertasnacionales.cl | FICHA TÉCNICA ↗ |
| Radier y zapatas | Melón | Hormigón con Fibra | melon.cl | FICHA TÉCNICA ↗ |
| Radier pulido | Sika Chile | Sikafloor-3 QuartzTop | chl.sika.com | FICHA TÉCNICA ↗ |
| Pilar estructural | Arauco — Hilam | Madera Laminada Encolada MLE 20c | arauco.com/hilam | FICHA TÉCNICA ↗ |
| Armazón | Arauco — MSD | Construcción Premium MSD | arauco.com | FICHA TÉCNICA ↗ |
| Muro cortina — montante | Arauco — MSD | Pino Radiata Cepillado | arauco.com | FICHA TÉCNICA ↗ |
| Muro cortina — panel | Arauco | Panel vacío (celosía) — ficha de referencia: MSD Revestimiento Machihembrado | arauco.com/chile | FICHA TÉCNICA ↗ |
| Puerta | Moldupanel (Puertas Chile) | Puerta Pino Radiata Italia 80×210 | puertaschile.cl | FICHA TÉCNICA ↗ |
| Herrajes | Häfele (vía El Carpintero) | Bisagras y cerraduras | elcarpintero.cl | FICHA TÉCNICA ↗ |
| Ventana | DMC Ventanas de Aluminio | Ventana proyectante de aluminio negro, a medida | construex.cl/dmc_ventanas_de_aluminio | FICHA TÉCNICA ↗ |
| Lavaplatos | Fanaloza | Lavaplatos de sobreponer 80×50 | fanaloza.cl | FICHA TÉCNICA ↗ |
| Lavamanos | Fanaloza | Lavamanos Ciro con pedestal | fanaloza.cl | FICHA TÉCNICA ↗ |
| WC | Fanaloza | Inodoro New Valencia a muro | fanaloza.cl | FICHA TÉCNICA ↗ |
| Bebedero | FAMAVA | Bebedero BAG-40 | famava.cl | FICHA TÉCNICA ↗ |
| Bicicletero | Rabke | Bicicletero U invertida TB170 | rabke.cl | FICHA TÉCNICA ↗ |
| Mobiliario — banca | Fabricación local a pedido | Banca de acero galvanizado y madera, 2500 × 400 × 450 mm | — | — |
| Abastecimiento local | Sodimac / Construmart Talca | Distribución general | sodimac.cl<br>construmart.cl | — |

PM

# DESCARGAR DOCUMENTOS E IMÁGENES

Referentes, proveedores, documentos técnicos, láminas e imágenes — no incluye el modelo Revit ni el IFC (ver punto 08).

↓ DESCARGAR (.ZIP, 30 MB)

08

## MODELO REVIT


HAB_ARQ_MODELO_R01.RVT

| 7 725 | 956 | 196 | 76 | 68 | 3+2 |
|---|---|---|---|---|---|
| ELEMENTOS TOTALES | TIPOS | FAMILIAS | CATEGORÍAS | VISTAS | NIVELES PRINCIPALES + SUBNIVELES |

### VISOR 3D

CARGAR VISOR 3D

Se descarga el IFC4x3 (4,5 MB) y se muestra en el navegador. Arrastra para girar, usa la rueda para acercar y mantén presionada la rueda (botón central) para desplazar la vista, como en Revit.

 


PRUEBA EL VISOR CON TUS PROPIOS ARCHIVOS IFC ↗

## CANTIDADES DEL MODELO

Cantidades obtenidas del modelo Revit.

Haz clic en una fila para verla en el visor 3D.

| ELEMENTO | TIPO | CANT. | MEDIDA |
|---|---|---|---|
| Muros de quincha | MURO_EXT_QUINCHA_12cm | 11 | 56,83 $m^2$ · 6,82 $m^3$ |
| Muros de celosía | M.CORTINA_EXT_CELOSIA_PINO RADIATA (FIX N) | 6 | 37,29 $m^2$ |
| Montantes de celosía | 19x90mm_PINO RADIATA | 396 | 251,5 m · 0,43 $m^3$ |
| Paneles de celosía (vacíos) | Empty (celosía) | 192 | 32,52 $m^2$ |
| Puertas | 80x210cm | 2 | — |
| Ventanas | 40x120cm PROYECTANTE | 2 | — |
| Pilares de madera | 130X130 | 16 | 0,65 $m^3$ |
| Vigas principales | 2"X8" Cepillada | 16 | 71,4 m · 0,53 $m^3$ |
| Vigas secundarias | 2"X4" Cepillada | 16 | 48,0 m · 0,17 $m^3$ |
| Fundaciones aisladas | FUNDACIÓN AISLADA_HA_60x60x50cm | 16 | 3,03 $m^3$ |

| | | | |
|---|---|---|---|
| Radier | RADIER_INT_HA_15cm | 1 | 76,52 $m^2$ · 11,48 $m^3$ |
| Pavimento de hormigón pulido | PAV_INT_HORMIGON PULIDO_2cm | 1 | 76,26 $m^2$ · 1,53 $m^3$ |
| Cubierta (4 faldones) | CUBIERTA_ZINC ONDULADO_CN-1020_0.50mm | 4 | 76,53 $m^2$ · 1,38 $m^3$ |
| Inodoros | 41x69cm | 2 | 0,07 $m^3$ |
| Lavamanos | 53x41cm | 2 | 0,02 $m^3$ |
| Bebederos | BAG-40_32x32x112cm | 3 | 0,05 $m^3$ |
| Lavaplatos con mueble base | 80x60cm | 1 | 0,04 $m^3$ |
| Muebles base de cocina | 104x64cm | 2 | 0,09 $m^3$ |
| Bancas | INSITU_250x40x45cm | 5 | 1,28 $m^3$ |
| Bicicleteros | TB170_1 bicicleta | 5 | 0,01 $m^3$ |
| Recintos | 9 recintos | 9 | 79,45 $m^2$ |

DESCARGAR EXCEL (.XLSX) ↓ DESCARGAR CSV ↓

## ARCHIVOS DEL MODELO

### HAB_ARQ_MODELO_R01.RVT
Modelo BIM del habitáculo Pausa Maule · 233 MB

DESCARGAR ↗

### HAB_ARQ_MODELO_R01_IFC4X3.IFC
Export IFC4X3_ADD2 · MVD CoordinationView · 4,5 MB

DESCARGAR ↗