PM
PAUSA MAULE

PARTIDO REFERENTES IMÁGENES LÁMINAS MATERIALIDAD DOCUMENTOS PROVEEDORES MODELO





HABITÁCULO PARA CICLISTAS

UN PUNTO DE DESCANSO EN EL CORREDOR VITIVINÍCOLA DE TALCA.

Pausa Maule es un punto de descanso para ciclistas de ruta en el corredor vitivinícola de Talca, Región del Maule. Un vacío central bajo una retícula de nueve cuadrantes ordena masa, umbral y paisaje.

AUTOR	Matías Alvarez C.
REDES	Instagram @matias_arq_ ↗ · LinkedIn ↗
CURSO	Workshop BIM + IA · creado por The BIM Cowork ↗
PROYECTO	Habitáculo Pausa Maule
UBICACIÓN	Talca, Región del Maule
PROGRAMA	9 recintos, 79.45 m^2 totales
MODELO	HAB_ARQ_MODELO_R01.rvt

3×3
RETÍCULA NINE-SQUARE

9
RECINTOS MODELADOS


79.45
M^2 ÁREA TOTAL

16
PROVEEDORES VERIFICADOS

01

EL PARTIDO

CONCEPTO SOBRE LA GRILLA 3×3

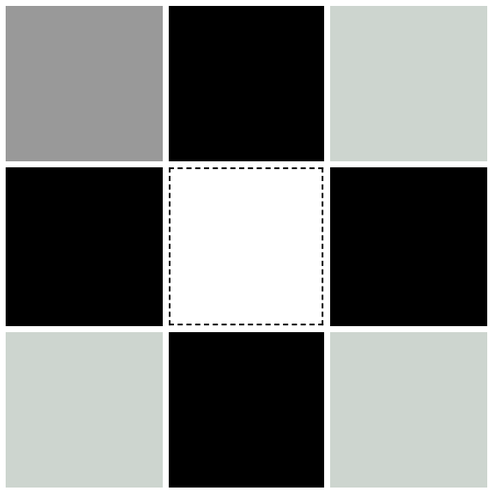

El partido organiza el programa sobre una retícula de nueve cuadrantes: cuatro llenos estructurales (madera + quincha) sostienen un vacío central, el patio, donde crece un árbol a través de la cubierta.

- **Acceso principal** resuelto en el cuadrante superior izquierdo, sin cruzar muros cortina.
- Los **muros cortina** perimetrales quedaron libres de accesos tras la corrección del partido: los recorridos pasan entre los llenos, no a través de los paños vidriados.
- El **patio central** es el umbral entre paisaje y recinto — ahí ocurre la pausa.

LÁMINA DEL PARTIDO (PDF) ↗

llenos, vacíos, accesos y volumen principal

02

REFERENTES

5 PRECEDENTES DE AIRES MATEUS

01 **MASA**

02 **VACÍO**

03 **UMBRAL**

04 **PAISAJE**

05 **RECORRIDO**

Referentes Aires Mateus — contraste nine-square · 5 precedentes contrastados contra el partido de Pausa Maule · selección de 4 láminas, PDF completo de 9 páginas

PAUSA MAULE · HABITÁCULO 3×3

AIRES MATEUS

Referentes existentes

Masa, vacío, umbral, luz y paisaje como herramientas para proyectar una pausa ciclista.



Cabanas no Rio · Comporta, 2013 · Fot. Nelson Garrido

ARQUITECTURA · SELECCIÓN CONCEPTUAL

01

05 **EL MURO TAMBIÉN CONSTRUYE EL UMBRAL**



Pa.te.os · Melides, 2020 · Fot. João Guimarães

03 · PA.TE.OS

Muros continuos delimitan recintos y, al ser atravesados, producen negativos profundos que encuadran el paisaje.

LÍMITE

El muro define una habitación incluso cuando no completa un volumen.

UMBRAL

La abertura tiene profundidad suficiente para convertirse en estancia.

PAISAJE

El vacío dirige la mirada y relaciona arquitectura con vegetación.

APLICACIÓN

Convertir la celda de acceso en una pausa cubierta, no en un simple paso.

02

DESAPARECER PARA CONSTRUIR UN CENTRO PROTEGIDO





Casa en Monsaraz · Alentejo, 2018 · Fot. João Guimarães

04 · CASA EN MONSARAZ

El terreno oculta la casa; patios circulares y una abertura superior revelan su organización.

APLICACIÓN

Proteger el centro sin aislarlo del horizonte.

03

EL RECORRIDO ARTICULA INTIMIDAD, ENCUENTRO Y PAISAJE





Nursing Home · Alcácer do Sal, 2010 · Fot. Fernando Guerra / FG+SG

05 · NURSING HOME

Unidades independientes forman un cuerpo continuo; los retranqueos median entre intimidad y vida colectiva.

APLICACIÓN

Hacer del acceso y el patio una secuencia breve de sombra, pausa y encuentro.

04

ABRIR PDF COMPLETO ↗

03

IMÁGENES DEL PROYECTO

RENDERS E ISOMÉTRICAS



VISTA AÉREA — EL PATIO Y EL ÁRBOL ATRAVESANDO LA CUBIERTA




INTERIOR — BEBEDEROS Y DESCANSO




INTERIOR — UMBRAL HACIA EL VALLE


VISTAS ISOMÉTRICAS

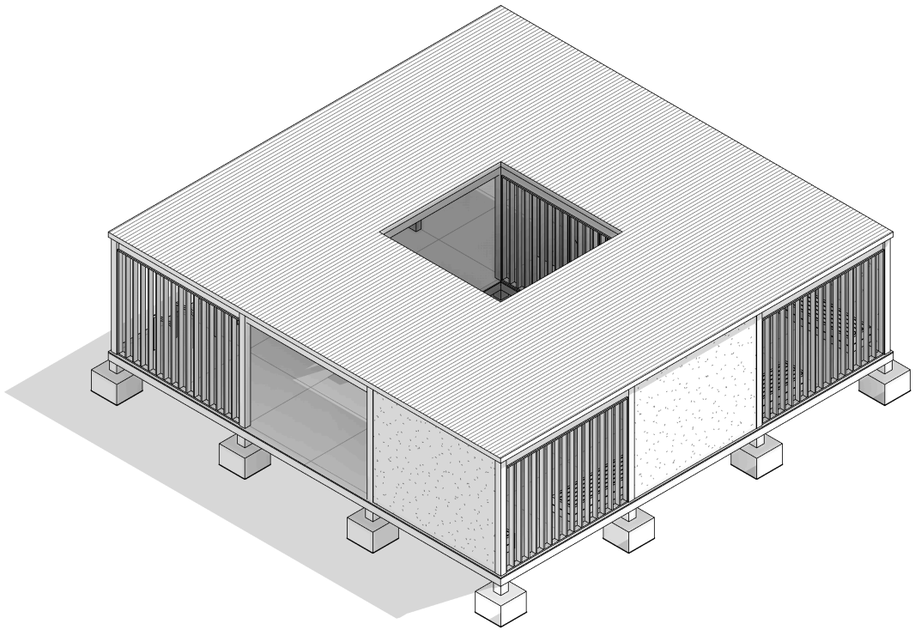

Volumen, cubierta y patio

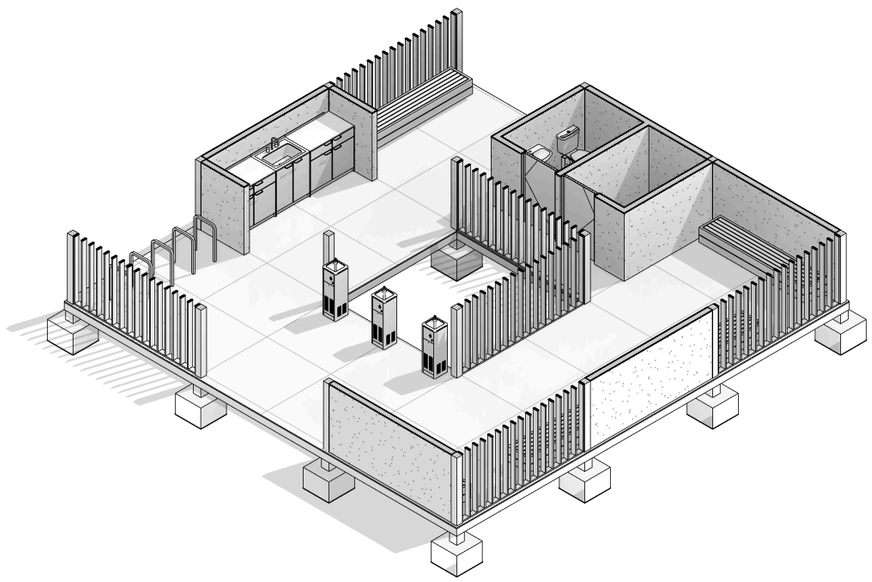

Sin cubierta — bebederos, baño, apoyo y bicicletas

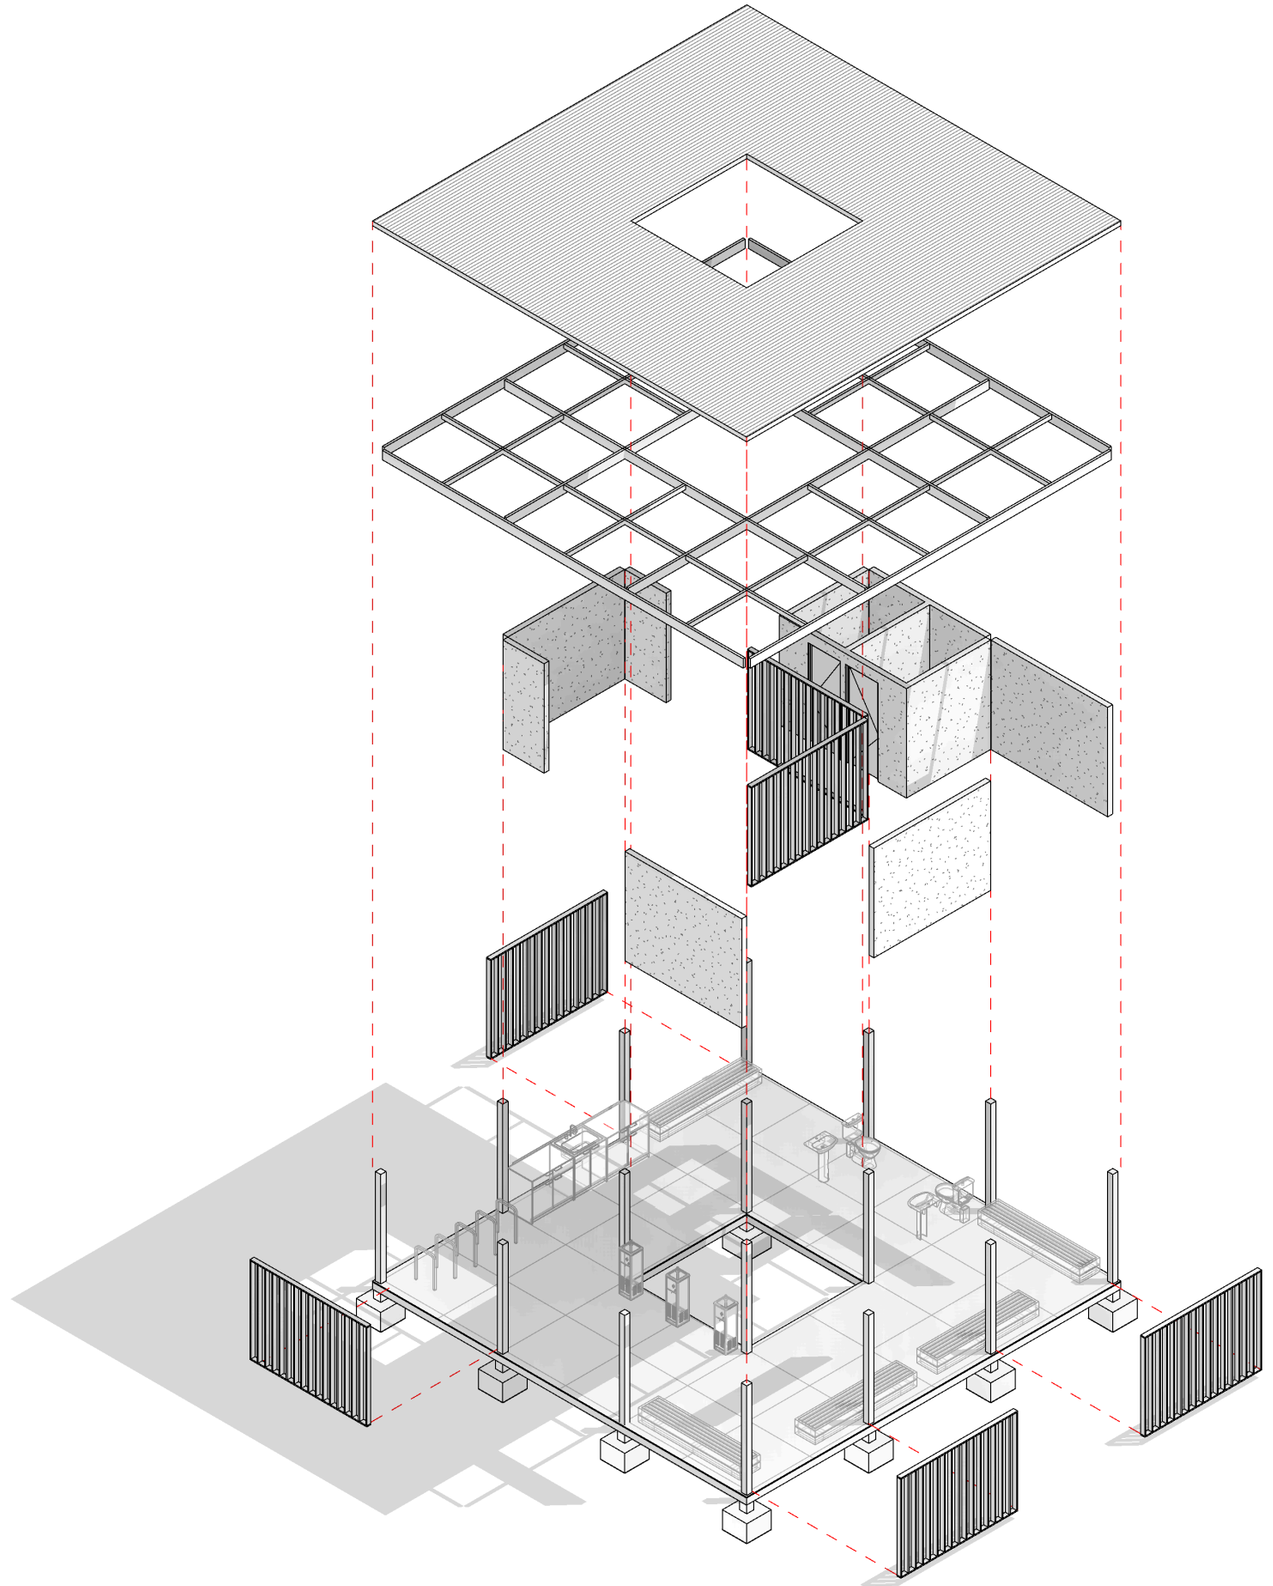

Isométrica explotada — capas constructivas: cubierta, armazón, paramentos y mobiliario

VIDEOS



Interior — bebederos y descanso



Exterior — el habitáculo entre viñedos


04

LÁMINAS

PLANIMETRÍA TÉCNICA

Lámina A101 — Planimetría general · planta, 4 elevaciones, 3 cortes e isométricas · 1:50

+ − AJUSTAR PANTALLA COMPLETA ABRIR PDF ↗

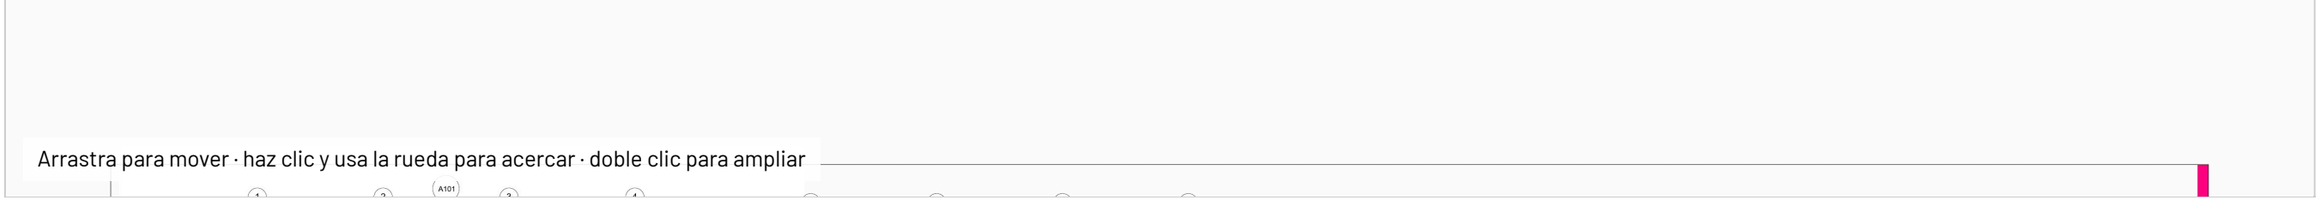
Arrastra para mover · haz clic y usa la rueda para acercar · doble clic para ampliar
A101

05

MATERIALIDAD

VERIFICADA CONTRA FICHAS DE FABRICANTE



QUINCHA

`MURO_EXT_QUINCHA_12cm`

Sistema quincha liviana húmeda — Corporación Protierra Chile, red MINVU/DITEC.

VER ELEMENTO ↗



PINO RADIATA

`MT_PINO RADIATA · MLE 20c`

Pilares glulam Hilam MLE, armazón dimensionado y montantes Arauco. Los paneles del muro cortina quedan vacíos (celosía).

VER ELEMENTO ↗




ZINCALUM

`MT_PLANCHA ONDULADA ZINCALUM`

Plancha ondulada sobre estructura de madera — Cubiertas Nacionales CN-1020.

VER ELEMENTO ↗

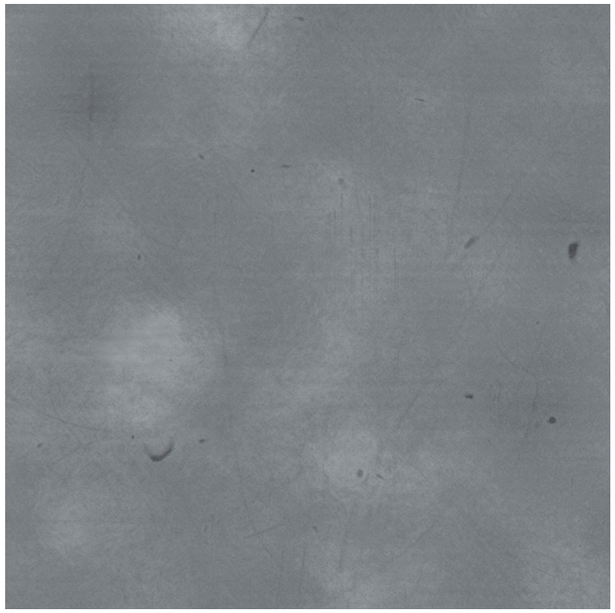

HORMIGÓN

`PAV_INT_HORMIGON PULIDO_2cm`

Radier con fibra Melón + endurecedor superficial Sikafloor-3 QuartzTop. El mismo hormigón armado forma las 16 zapatas aisladas bajo los pilares.

VER ELEMENTO ↗

06

DOCUMENTOS TÉCNICOS

REGLAS, PEB, NDI Y PARÁMETROS

REGLAS DE TRABAJO BIM

Resumen del Estándar PlanBIM Chile aplicado a Pausa Maule · Paso 01

PDF ↗

ESPECIFICACIÓN TÉCNICA

Materiales, fichas de fabricante, categorías cerradas

PDF ↗

PEB PRELIMINAR

Plan de Ejecución BIM — etapa preliminar

PDF ↗

PEB COMPLETADO

Tabla NDI por categoría y 9 recintos (nombre, número, nivel, área, perímetro)

XLSX ↓ PDF ↗

TABLA NDI

Niveles de Desarrollo de la Información

PDF ↗

PARÁMETROS COMPARTIDOS

Grupo NDI2 — parámetros compartidos del proyecto

TXT ↓ PDF ↗

07

PROVEEDORES

16 PROVEEDORES VERIFICADOS

FICHAS DE PROVEEDORES

16 proveedores verificados · contacto, sitio web, ficha técnica

XLSX ↓

ELEMENTO	EMPRESA	PRODUCTO	SITIO WEB
Muro / Quincha	Corporación Protierra Chile	Sistema Quincha Liviana Húmeda	redproterra.org
Cubierta	Cubiertas Nacionales	Panel Ondulado CN-1020	cubiertasnacionales.cl
Radier y zapatas	Melón	Hormigón con Fibra	melon.cl
Radier pulido	Sika Chile	Sikafloor-3 QuartzTop	chl.sika.com
Pilar estructural	Arauco — Hilam	Madera Laminada Encolada MLE 20c	arauco.com/hilam
Armazón	Arauco — MSD	Construcción Premium MSD	arauco.com
Muro cortina — montante	Arauco — MSD	Pino Radiata Cepillado	arauco.com
Muro cortina — panel	Arauco	Panel vacío (celosía) — ficha de referencia: MSD Revestimiento Machihembrado	arauco.com/chile
Puerta	Moldupanel (Puertas Chile)	Puerta Pino Radiata Italia 80×210	puertaschile.cl
Herrajes	Häfele (vía El Carpintero)	Bisagras y cerraduras	elcarpintero.cl
Sanitarios	Fanaloza	New Valencia a Muro / Lavamanos Ciro	fanaloza.cl
Bebedero	Reece	Wolfen Sensor Drinking Fountain WDF2SS	reece.com.au
Lavaplatos	Fanaloza	Lavaplatos de sobreponer con escurridor 80×50	fanaloza.cl
Bicicletero	Dero Bike Racks	U-Lockit	dero.com
Banca	Metalco	Big Harris (ficha de terceros)	metalco.it
Abastecimiento local	Sodimac / Construmart Talca	Distribución general	sodimac.cl

DESCARGAR DOCUMENTOS E IMÁGENES

Referentes, proveedores, documentos técnicos, láminas e imágenes — no incluye el modelo Revit ni el IFC (ver punto 08).

↓ DESCARGAR (.ZIP, 35 MB)

08

MODELO REVIT

HAB_ARQ_MODELO_R01.RVT

7 469
ELEMENTOS TOTALES

944
TIPOS

194
FAMILIAS

76
CATEGORÍAS

49
VISTAS

3+2
NIVELES PRINCIPALES + SUBNIVELES

VISOR 3D

CARGAR VISOR 3D

Se descarga el IFC4x3 (4,5 MB) y se muestra en el navegador. Arrastra para girar, usa la rueda para acercar y mantén presionada la rueda (botón central) para desplazar la vista, como en Revit.

CANTIDADES DEL MODELO

Cantidades obtenidas del modelo Revit.

Haz clic en una fila para verla en el visor 3D.

CATEGORÍA	TIPO	CANT.	MEDIDA
Muros	MURO_EXT_QUINCHA_12cm	11	56,83 m^2 · 6,82 m^3
Muros cortina	M.CORTINA_EXT_CELOSIA_PINO RADIATA (FIX N)	6	37,29 m^2
Montantes de muro cortina	12.5x100mm_PINO RADIATA	396	250,2 m · 0,63 m^3
Paneles de muro cortina	Empty (celosía)	192	31,04 m^2
Puertas	80x210cm	2	—
Pilares estructurales	130X130	16	0,65 m^3
Armazón principal	2"X8" Sin cepillar	16	71,4 m · 0,70 m^3
Armazón secundario	2"X4" Cepillada	16	48,0 m · 0,24 m^3
Fundaciones aisladas	FUNDACIÓN AISLADA_HA_60x60x50cm	16	3,03 m^3
Radier estructural	RADIER_INT_HA_15cm	1	76,56 m^2 · 11,49 m^3
Pavimento pulido	PAV_INT_HORMIGON PULIDO_2cm	1	76,26 m^2 · 1,53 m^3
Cubierta (4 faldones)	CUBIERTA_ZINC ONDULADO_10cm	4	76,53 m^2 · 7,65 m^3
Inodoros	41x69cm	2	0,07 m^3
Lavamanos	53x41cm	2	0,02 m^3
Bebederos	31x32cm	3	0,05 m^3
Lavaplatos	80x60cm	1	0,04 m^3
Muebles base de cocina	104x64cm	2	0,09 m^3
Bancas	250x50cm	5	1,60 m^3
Bicicleteros	2 bicicletas	5	0,01 m^3
Recintos	9 recintos	9	79,45 m^2

DESCARGAR EXCEL (.XLSX) ↓ DESCARGAR CSV ↓

ARCHIVOS DEL MODELO

HAB_ARQ_MODELO_R01.RVT

Modelo BIM del habitáculo Pausa Maule · 214 MB · descarga con aprobación del autor

SOLICITAR ACCESO ↗

HAB_ARQ_MODELO_R01_IFC4X3.IFC

Export IFC4X3_ADD2 · MVD CoordinationView · 4,5 MB · descarga con aprobación del autor

SOLICITAR ACCESO ↗