PM
PAUSA MAULE

PARTIDO REFERENTES IMÁGENES LÁMINAS MATERIALIDAD DOCUMENTOS PROVEEDORES MODELO





HABITÁCULO PARA CICLISTAS · WORKSHOP BIM + IA · MÉTODO TBC
EXTERIOR — EL HABITÁCULO ENTRE EL VALLE Y CORDILLERA DE LA COSTA

VER IMÁGENES ↗


HABITÁCULO PARA CICLISTAS

Pausa Maule es un punto de descanso para ciclistas de ruta en el corredor vitivinícola de Talca, Región del Maule. Un vacío central bajo una retícula de nueve cuadrantes ordena masa, umbral y paisaje.

AUTOR	Matías Alvarez C.
REDES	Instagram @matias_arq_ ↗ · LinkedIn ↗
CURSO	Workshop BIM + IA · creado por The BIM Cowork ↗
PROYECTO	Habitáculo Pausa Maule
UBICACIÓN	Talca, Región del Maule
PROGRAMA	9 recintos, 79.45 m^2 totales
MODELO	HAB_ARQ_MODELO_R01.rvt

RETÍCULA NINE-SQUARE | RECINTOS MODELADOS | M^2 ÁREA TOTAL | PROVEEDORES VERIFICADOS

CONCEPTO SOBRE LA GRILLA 3×3

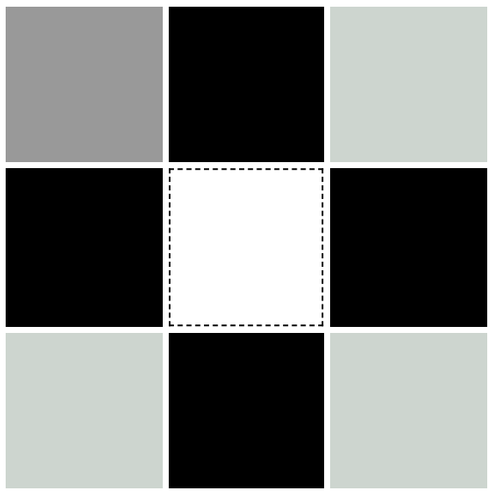

El partido organiza el programa sobre una retícula de nueve cuadrantes: cuatro llenos estructurales (madera + quincha) sostienen un vacío central, el patio, donde crece un árbol a través de la cubierta.

- **Acceso principal** resuelto en el cuadrante superior izquierdo, sin cruzar muros cortina.
- Los **muros cortina** perimetrales quedaron libres de accesos tras la corrección del partido: los recorridos pasan entre los llenos, no a través de los paños vidriados.
- El **patio central** es el umbral entre paisaje y recinto — ahí ocurre la pausa.

LÁMINA DEL PARTIDO (PDF) ↗

llenos, vacíos, accesos y volumen principal

01 02 03 04 05

Referentes Aires Mateus — contraste nine-square · 5 precedentes contrastados contra el partido de Pausa Maule · selección de 4 láminas, PDF completo de 9 páginas

PAUSA MAULE · HABITÁCULO 3×3

AIRES MATEUS

Referentes existentes

Masa, vacío, umbral, luz y paisaje como herramientas para proyectar una pausa ciclista.



Cabanas no Rio · Comporta, 2013 · Fot. Nelson Garrido

ARQUITECTURA · SELECCIÓN CONCEPTUAL

01

05

EL MURO TAMBIÉN CONSTRUYE EL UMBRAL



Pa.te.os · Melides, 2020 · Fot. João Guimarães

03 · PA.TE.OS

Muros continuos delimitan recintos y, al ser atravesados, producen negativos profundos que encuadran el paisaje.

LÍMITE

El muro define una habitación incluso cuando no completa un volumen.

UMBRAL

La abertura tiene profundidad suficiente para convertirse en estancia.

PAISAJE

El vacío dirige la mirada y relaciona arquitectura con vegetación.

APLICACIÓN

Convertir la celda de acceso en una pausa cubierta, no en un simple paso.

02

06

DESAPARECER PARA CONSTRUIR UN CENTRO PROTEGIDO





Casa en Monsaraz · Alentejo, 2018 · Fot. João Guimarães

04 · CASA EN MONSARAZ

El terreno oculta la casa; patios circulares y una abertura superior revelan su organización.

APLICACIÓN

Proteger el centro sin aislarlo del horizonte.

03

07

EL RECORRIDO ARTICULA INTIMIDAD, ENCUENTRO Y PAISAJE





Nursing Home · Alcácer do Sal, 2010 · Fot. Fernando Guerra / FG+SG

05 · NURSING HOME

Unidades independientes forman un cuerpo continuo; los retranqueos median entre intimidad y vida colectiva.

APLICACIÓN

Hacer del acceso y el patio una secuencia breve de sombra, pausa y encuentro.

04

ABRIR PDF COMPLETO ↗

–

RENDERS E ISOMÉTRICAS



VISTA AÉREA — EL PATIO Y EL ÁRBOL ATRAVESANDO LA CUBIERTA



INTERIOR — BEBEDEROS Y DESCANSO



INTERIOR — UMBRAL HACIA EL VALLE




EXTERIOR — EL HABITÁCULO ENTRE VIÑEDOS




DEL UMBRAL AL VIÑEDO — MURO DE QUINCHA Y BANCA




INTERIOR — BANCA DE DESCANSO Y CELOSÍA

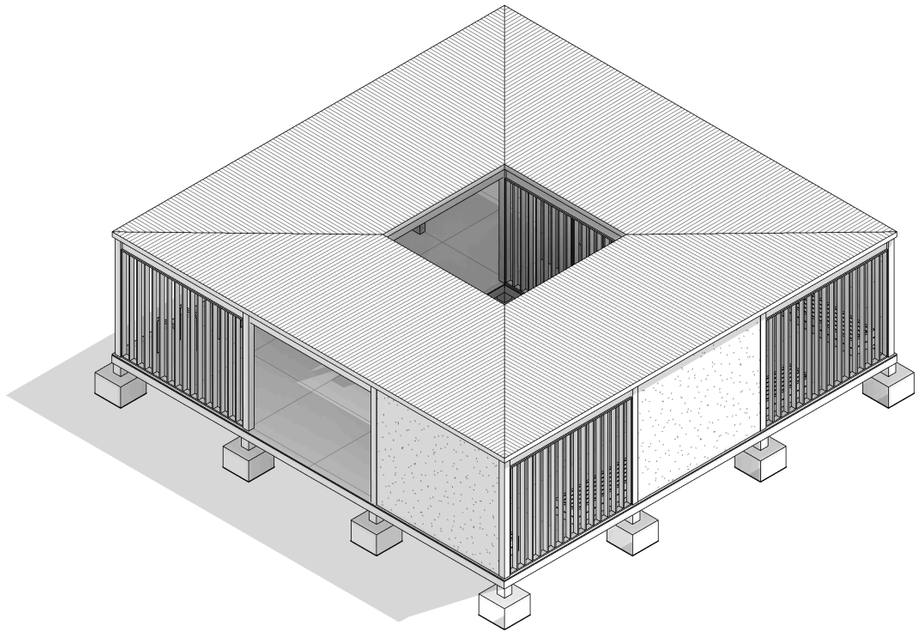

Volumen, cubierta y patio

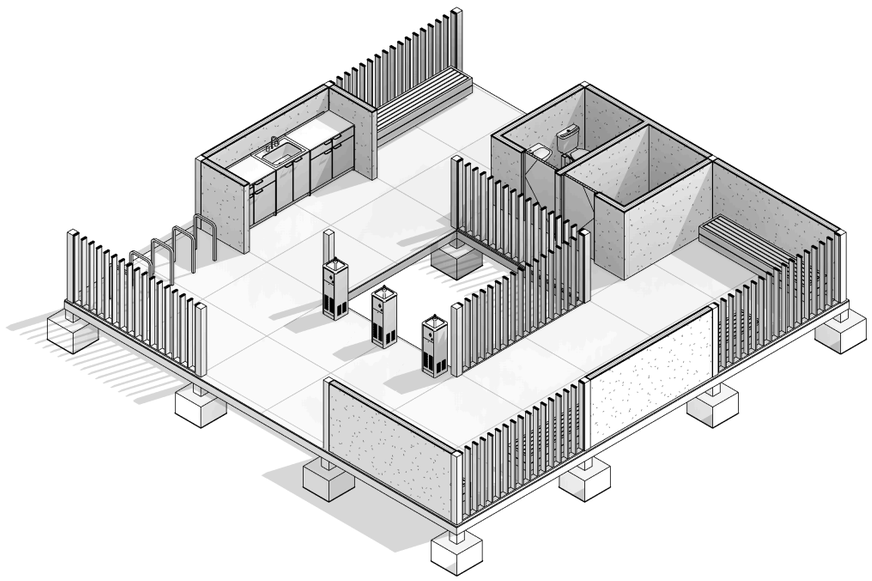

Sin cubierta — bebederos, baño, apoyo y bicicletas

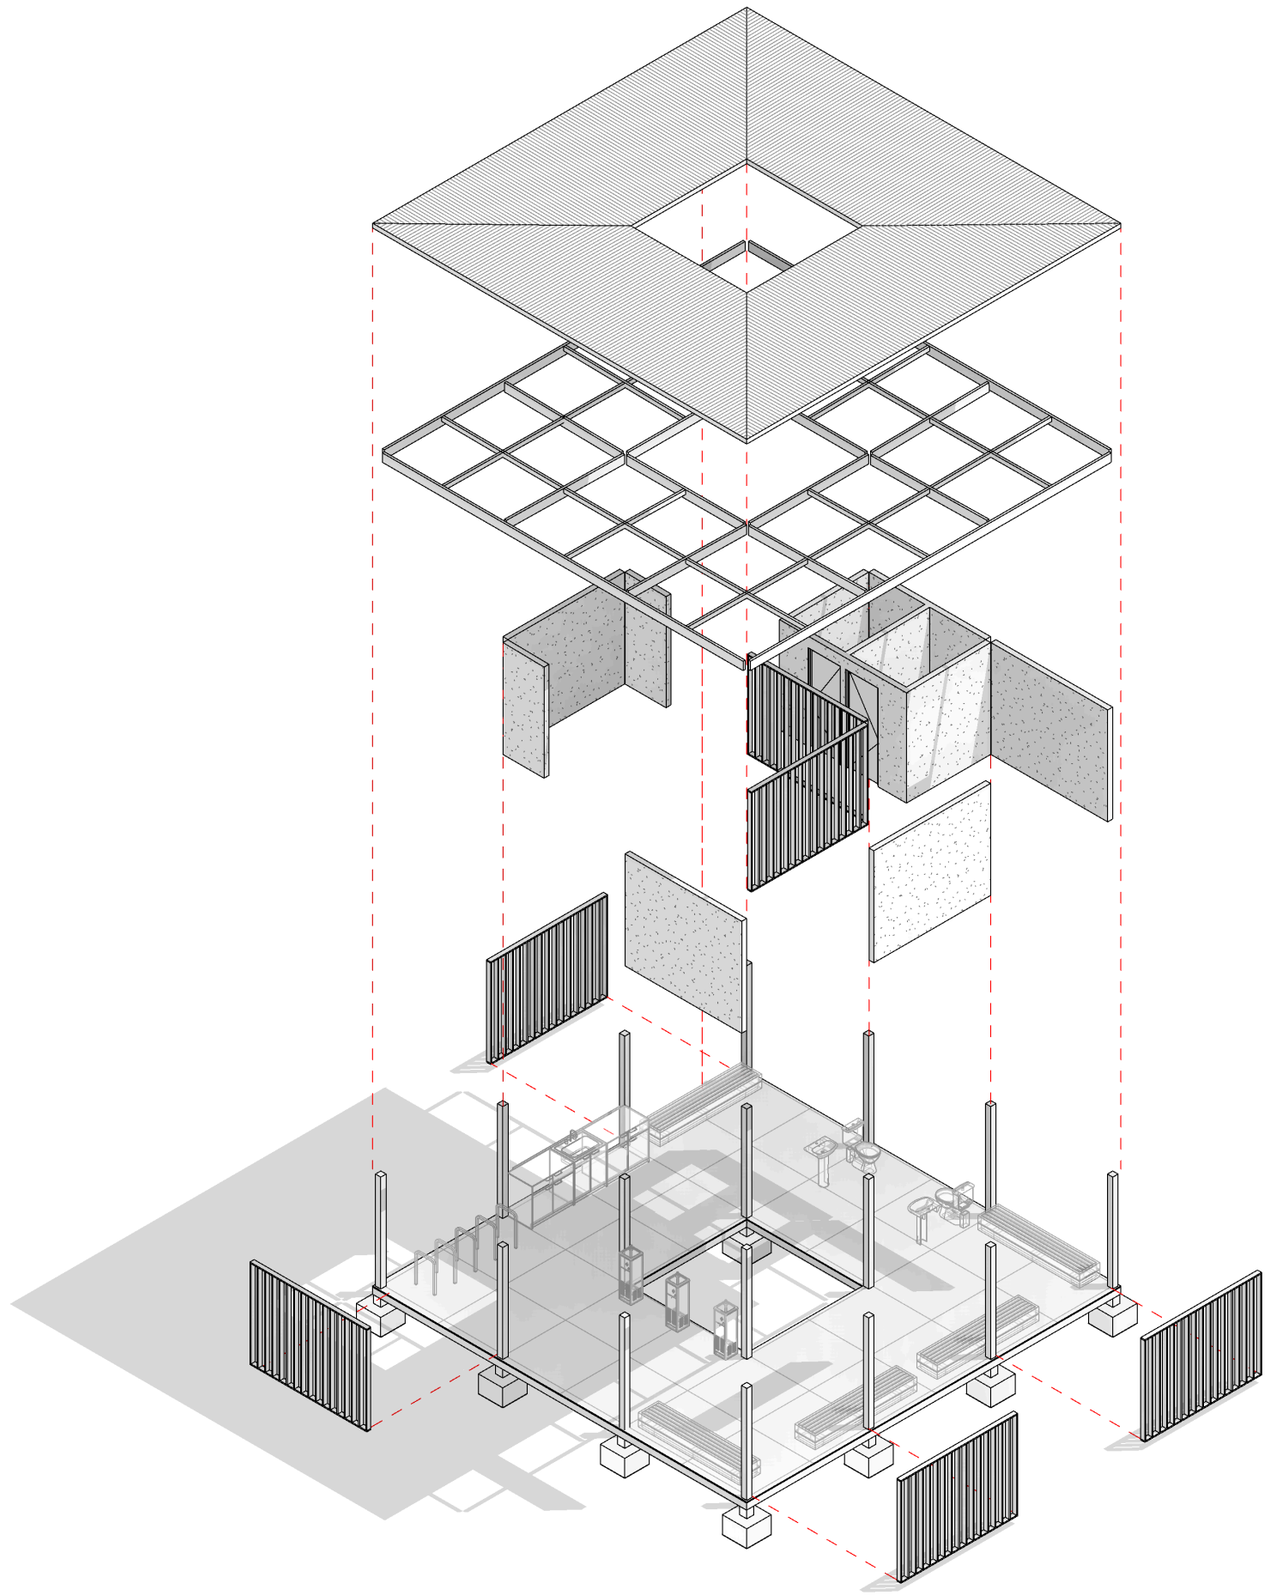

Isométrica explotada — capas constructivas: cubierta, armazón, paramentos y mobiliario




Exterior — el habitáculo entre viñedos


PLANIMETRÍA TÉCNICA

Lámina A101 — Planimetría general · planta, 4 elevaciones, 3 cortes, cubierta, superficies, isométricas y tablas de superficie · 1:50


+ − AJUSTAR PANTALLA COMPLETA ABRIR PDF ↗

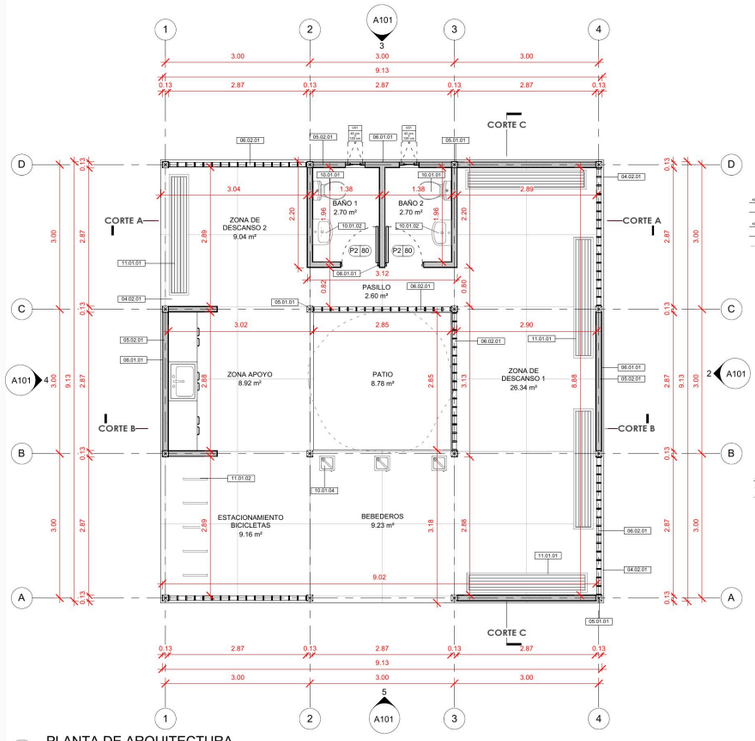


1 PLANTA DE ARQUITECTURA
1 : 50

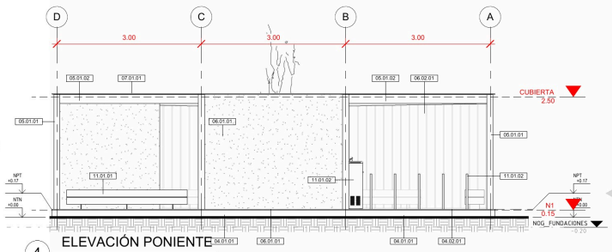


4 ELEVACIÓN PONIENTE
1 : 50

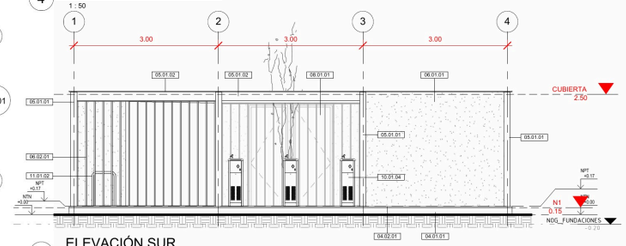


5 ELEVACIÓN SUR
1 : 50

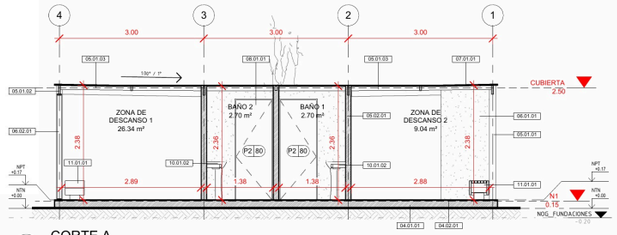


6 CORTE A
1 : 50

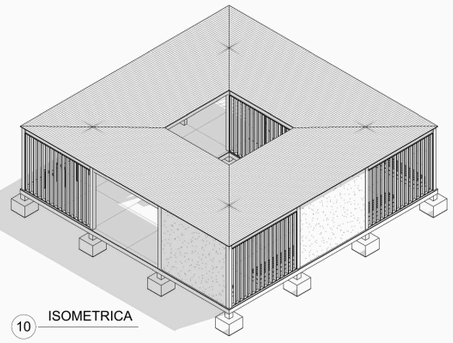


10 ISOMETRICA

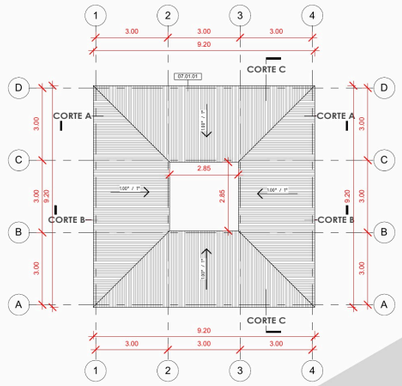


7 CUBIERTA
1 : 100

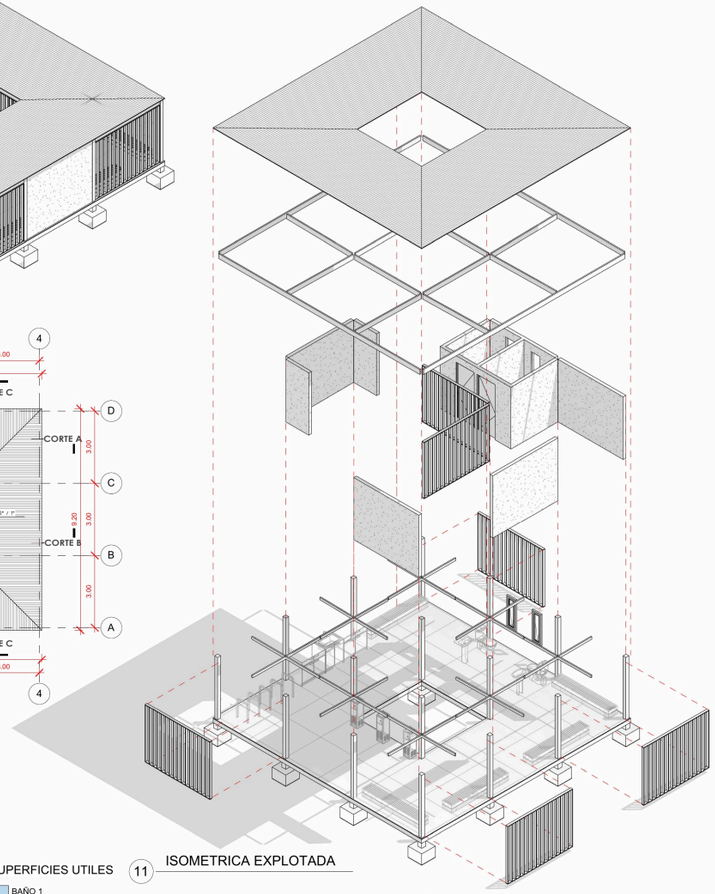


11 ISOMETRICA EXPLOTADA

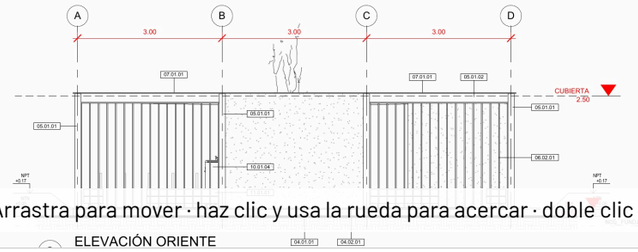

ELEVACIÓN ORIENTE

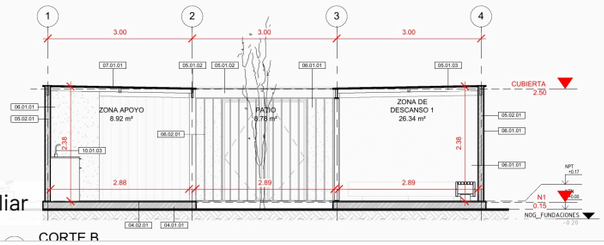

CORTE B

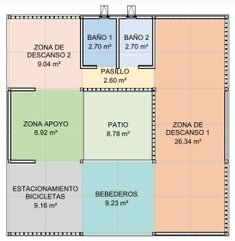

PLANTA DE SUPERFICIES

SUPERFICIES UTILES

- BAÑO 1
- BAÑO 2
- BEBEDEROS
- ESTACIONAMIENTO BICICLETAS
- PASILLO
- PATIO
- ZONA APOYO
- ZONA DE DESCANSO 1
- ZONA DE DESCANSO 2

www.thebimcowork.cl | Proyecto elaborado con fines académicos no apto para construcción | @thebimcowork

Arrastra para mover · haz clic y usa la rueda para acercar · doble clic para ampliar

Lámina A102 — Tablas de especificaciones · keynotes, fichas técnicas, armazón, vanos y planta de fundaciones

+ − AJUSTAR PANTALLA COMPLETA ABRIR PDF ↗

TABLA DE MUROS - EETT

Clave	Familia y tipo	Área	Volumen	Cant.
06.01.01	Muro básico: MURO_EXT_QUINCHA_12cm	55.87 m²	6.70 m³	11
06.02.01	Muro cortina: M.CORTINA_EXT_CELOSIA_PINO RADIATA (FIX N)	37.56 m²	0.00 m³	6

TABLA DE CUBIERTAS - EETT

Clave	Familia y tipo	Área	Volumen	Cant.
07.01.01	Cubierta básica: CUBIERTA_ZINC ONDULADO_CN-1020_0.50mm	76.53 m²	1.38 m³	4

TABLA DE SUELOS - EETT

Clave	Familia y tipo	Área	Volumen	Cant.
04.01.01	Suelo: RADIER_INT_HA_15cm	76.52 m²	11.48 m³	1
04.02.01	Suelo: PAV_INT_HORMIGON PULIDO_2cm	76.26 m²	1.53 m³	1

TABLA DE PUERTAS - EETT

Clave	Familia y tipo	Ancho	Alto	Cant.
08.01.01	PRT_Puerta_INT_Simple_1 Panel_PINO RADIATA: 80x210cm	0.75	2.08	2

TABLA DE VENTANAS - EETT

Clave	Familia y tipo	Ancho	Alto	Cant.
08.02.01	VNT_Ventana Simple_1 hoja_ALUMINIO NEGRO: 40x120cm PROYECTANTE	0.40	1.20	2

TABLA DE KEYNOTES - EETT

Clave	Material	Partida EETT	Categoría	Área	Volumen	Cant.
03.01.01	MT_HORMIGON ARMADO	03.01.01 Zapata aislada de hormigón armado	Cimentación estructural	35.11 m²	3.03 m³	16
04.01.01	MT_HORMIGON ARMADO_RADIER 15CM	04.01.01 Radier interior de hormigón armado 15 cm	Suelos	76.52 m²	11.48 m³	1
04.02.01	MT_HORMIGON PULIDO	04.02.01 Terminación superficial de hormigón pulido	Suelos	76.26 m²	1.53 m³	1
05.01.01	MT_PINO RADIATA_PILAR 130X130	05.01.01 Pilar estructural de madera laminada	Pilares estructurales	20.42 m²	0.65 m³	16
05.01.02	MT_PINO RADIATA_VIGA 2X8	05.01.02 Viga estructural cepillada de Pino Radiata 2 x 8	Armazón estructural	31.95 m²	0.53 m³	16
05.01.03	MT_PINO RADIATA_ELEMENTO 2X4	05.01.03 Elemento de Pino Radiata 2 x 4	Armazón estructural	12.53 m²	0.17 m³	16
05.02.01	MT_MADERA ESTRUCTURAL	05.02.01 Estructura secundaria de muro	Muros	55.87 m²	5.59 m³	11
06.01.01	MT_TIERRA_QUINCHA	06.01.01 Muro exterior de quincha liviana húmeda	Muros	111.71 m²	1.12 m³	11
06.02.01	MT_PINO RADIATA_CELOSIA 19X90	06.02.01 Celosía exterior de madera	Montantes de muro cortina	56.52 m²	0.43 m³	396
07.01.01	MT_PLANCHA ONDULADA ZINCALUM	07.01.01 Cubierta metálica ondulada Zinc Alum	Cubiertas	76.53 m²	1.38 m³	4
08.01.01	MT_PINO RADIATA PUERTA	08.01.01 Puerta de Pino Radiata 80 x 210 cm	Puertas	8.78 m²	0.15 m³	2
10.01.01	MT_LOZA INODORO	10.01.01 Inodoro de loza vitrificada	Aparatos sanitarios	5.45 m²	0.07 m³	2
10.01.02	MT_LOZA LAVAMANOS	10.01.02 Lavamanos con pedestal	Aparatos sanitarios	2.25 m²	0.02 m³	2
10.01.03	MT_ACERO INOXIDABLE	10.01.03 Lavaplatos de acero inoxidable	Mobiliario	1.60 m²	0.04 m³	1
10.01.04	MT_ACERO INOXIDABLE	10.01.04 Bebedero de	Aparatos	8.89 m²	0.05 m³	3
11.01.02	MT_ACERO GALVANIZADO	11.01.02 Bicicletero	Emplazamiento	1.40 m²	0.01 m³	5

TABLA DE PILARES - EETT

Clave	Familia y tipo	Volumen	Cant.
05.01.01	PILAR_Pino Radiata_Rectangular: 130X130	0.65 m³	16

TABLA DE ARMAZON - EETT

Clave	Familia y tipo	Largo	Volumen	Cant.
05.01.02	VIGA_PINO RADIATA_Rectangular: 2"X8" Cepillada	70.15	0.53 m³	16
05.01.03	VIGA_PINO RADIATA_Rectangular: 2"X4" Cepillada	47.37	0.17 m³	16

TABLA DE FUNDACIONES - EETT

Clave	Familia y tipo	Volumen	Cant.
03.01.01	FUNDACIÓN AISLADA: FUNDACIÓN AISLADA_HA_60x60x50cm	3.03 m³	16

TABLA DE APARATOS SANITARIOS - EETT

Clave	Familia y tipo	Cant.
10.01.01	PLM_WC_ceramica_New Valencia a muro: 41x69cm	2
10.01.02	PLM_Lavamanos_ceramica_Ciro pedestal: 53x41cm	2
10.01.04	PLM_Bebedero_acero inoxidable_FAMAVA BAG-40: BAG-40_32x32x112cm	3

TABLA DE MOBILIARIO - EETT

Clave	Familia y tipo	Cant.
10.01.03	MBL_Mueble base cocina_Lavaplatos: 80x60cm	1
10.01.03	MBL_Mueble base cocina_Melamina: 104x64cm	2

TABLA DE EMPLAZAMIENTO - EETT

Clave	Familia y tipo	Cant.
11.01.01	SITIO_Banca_acero galvanizado y madera: INSITU_250x40x45cm	5
11.01.02	SITIO_Bicicletero_acero galvanizado_U invertida TB170: TB170_1 bicicleta	5

LEYENDA DE KEYNOTES - EETT

Valor de nota clave	Texto de nota clave
03.01.01	Zapata aislada de hormigón armado de 60 x 60 x 50 cm.
04.01.01	Radier interior de hormigón armado de 15 cm.
04.02.01	Terminación de hormigón pulido de 2 cm con endurecedor superficial.
05.01.01	Pilar estructural de Pino Radiata laminado encolado, sección 130 x 130 mm.
05.01.02	Viga estructural cepillada de Pino Radiata 2 x 8 pulgadas, dimensión real 41 x 185 mm, grado G2 o superior.
05.01.03	Elemento cepillado de Pino Radiata 2 x 4 pulgadas, dimensión real 41 x 90 mm.
05.02.01	Estructura secundaria de muro de Pino Radiata impregnado.
06.01.01	Muro exterior de quincha liviana húmeda, espesor nominal 12 cm.
06.02.01	Celosía exterior de Pino Radiata cepillado, montantes de 19 x 90 mm y separación libre de 45 mm.
07.01.01	Panel ondulado CN-1020 de acero con recubrimiento Zinc-Alum AZ-150, espesor 0,50 mm y altura de onda 18 mm.
08.01.01	Puerta interior de una hoja de Pino Radiata, línea Italia, dimensión nominal 80 x 210 cm.
10.01.01	Inodoro Fanaloza New Valencia, descarga dual.
10.01.02	Lavamanos Fanaloza Ciro con pedestal.
10.01.03	Lavaplatos Fanaloza de sobreponer con escurridor, 80 x 50 x 14,5 cm, modelo JHSM2614DE11CF.
	x 320 x 1120 mm.
	mes 2500 x 400 x 450 mm.

LISTA DE CORTE - ARMAZON - EETT

Clave	Familia y tipo	Largo (m)	Volumen	Cant.
05.01.02	VIGA_PINO RADIATA_Rectangular: 2"X8" Cepillada	2.87	0.13 m³	6
05.01.02	VIGA_PINO RADIATA_Rectangular: 2"X8" Cepillada	2.90	0.07 m³	3
05.01.02	VIGA_PINO RADIATA_Rectangular: 2"X8" Cepillada	2.91	0.04 m³	2
05.01.02	VIGA_PINO RADIATA_Rectangular: 2"X8" Cepillada	2.93	0.02 m³	1
05.01.02	VIGA_PINO RADIATA_Rectangular: 2"X8" Cepillada	8.87	0.27 m³	4
05.01.03	VIGA_PINO RADIATA_Rectangular: 2"X4" Cepillada	2.96	0.15 m³	14
05.01.03	VIGA_PINO RADIATA_Rectangular: 2"X4" Cepillada	2.98	0.02 m³	2

LISTA DE CORTE - PILARES - EETT

Clave	Familia y tipo	Nivel base	Nivel superior	Volumen	Cant.
05.01.01	PILAR_Pino Radiata_Rectangular: 130X130	N1	CUBIERTA	0.65 m³	16

CUADRO DE VANOS - PUERTAS - EETT


Clave	Familia y tipo	Ancho	Alto	Nivel	Ancho libre	Cant.
08.01.01	PRT_Puerta_INT_Simple_1 Panel_PINO RADIATA: 80x210cm	0.75	2.08	NPT		1
08.01.01	PRT_Puerta_INT_Simple_1 Panel_PINO RADIATA: 80x210cm	0.75	2.08	NPT		1

CUADRO DE VANOS - VENTANAS - EETT

Clave	Familia y tipo	Ancho	Alto	Nivel	Cant.
08.02.01	VNT_Ventana Simple_1 hoja_ALUMINIO NEGRO: 40x120cm PROYECTANTE	0.40	1.20	N1	1
08.02.01	VNT_Ventana Simple_1 hoja_ALUMINIO NEGRO: 40x120cm PROYECTANTE	0.40	1.20	N1	1

RESUMEN POR MATERIAL - EETT

Material	Área	Volumen
MT_ACERO GALVANIZADO	1.40 m²	0.01 m³
MT_ACERO INOXIDABLE	1.60 m²	0.04 m³
MT_ACERO INOXIDABLE CEPILLADO	8.89 m²	0.05 m³
MT_ALUMINIO GRAFITO	0.11 m²	0.00 m³
MT_ALUMINIO NEGRO	2.26 m²	0.03 m³
MT_BANCA ASIENTO	45.63 m²	1.26 m³
MT_BANCA PATAS	2.85 m²	0.01 m³
MT_GENERICO PUERTA	0.33 m²	0.00 m³
MT_GOMA NEGRA	0.00 m²	0.00 m³
MT_HORMIGON ARMADO	35.11 m²	3.03 m³
MT_HORMIGON ARMADO_RADIER 15CM	76.52 m²	11.48 m³
MT_HORMIGON PULIDO	76.26 m²	1.53 m³
MT_LATON CROMADO	0.05 m²	0.00 m³
MT_LOZA INODORO	5.45 m²	0.07 m³
MT_LOZA LAVAMANOS	2.25 m²	0.02 m³
MT_MADERA ESTRUCTURAL	55.87 m²	5.59 m³
MT_METAL CROMADO	0.02 m²	0.00 m³
MT_PINO RADIATA PUERTA	8.78 m²	0.15 m³
MT_PINO RADIATA_CELOSIA 19X90	56.52 m²	0.43 m³
MT_PINO RADIATA_ELEMENTO 2X4	12.53 m²	0.17 m³
MT_PINO RADIATA_PILAR 130X130	20.42 m²	0.65 m³
MT_PINO RADIATA_VIGA 2X8	31.95 m²	0.53 m³
MT_PLANCHA ONDULADA ZINCALUM	76.53 m²	1.38 m³
MT_TIERRA_QUINCHA	111.71 m²	1.12 m³
MT_VIDRIO	0.82 m²	0.00 m³


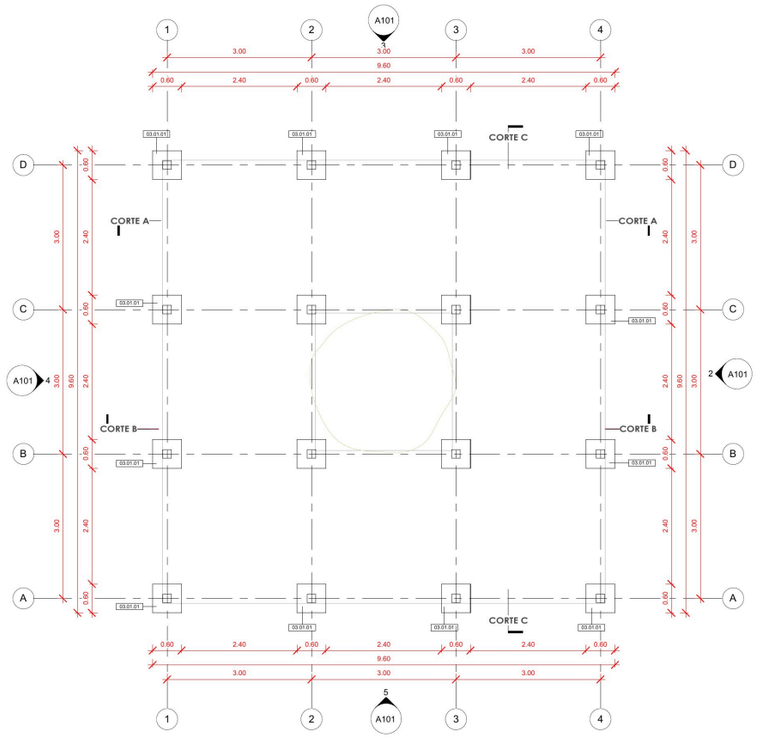



1 PLANTA DE FUNDACIONES
1 : 50

Arrastra para mover · haz clic y usa la rueda para acercar · doble clic para ampliar

ebimcowork.cl | Proyecto elaborado con fines académicos no apto para construcción | @thebimcowork

VERIFICADA CONTRA FICHAS DE FABRICANTE

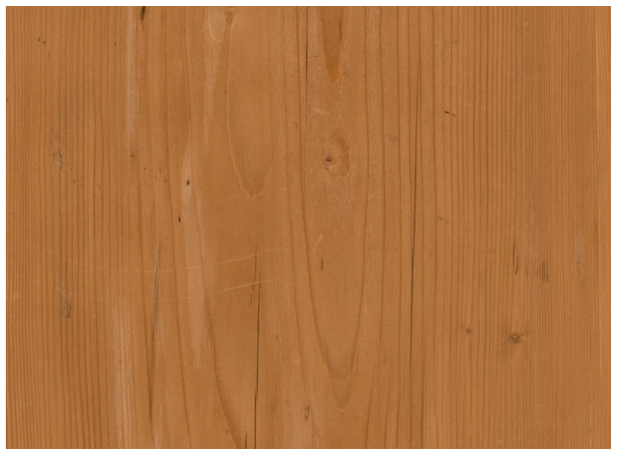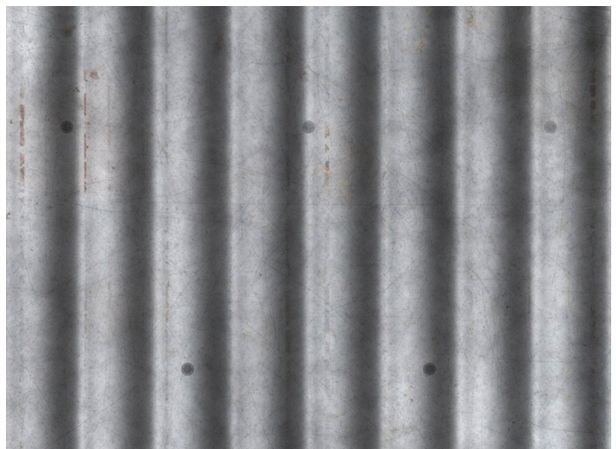QUINCHA

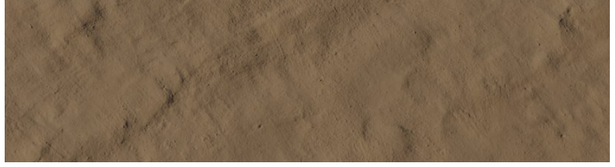MURO_EXT_QUINCHA_12cm

Sistema quincha liviana húmeda — Corporación Protierra Chile, red MINVU/DITEC.

VER ELEMENTO ↗



PINO RADIATA

MT_PINO RADIATA · MLE 20c

Pilares glulam Hilam MLE, armazón dimensionado y montantes Arauco. Los paneles del muro cortina quedan vacíos (celosía).

VER ELEMENTO ↗



ZINCALUM

MT_PLANCHA ONDULADA ZINCALUM

Plancha ondulada sobre estructura de madera — Cubiertas Nacionales CN-1020.

VER ELEMENTO ↗



HORMIGÓN

PAV_INT_HORMIGON PULIDO_2cm

Radier con fibra Melón + endurecedor superficial Sikafloor-3 QuartzTop. El mismo hormigón armado forma las 16 zapatas aisladas bajo los pilares.

VER ELEMENTO ↗

REGLAS, PEB, NDI Y PARÁMETROS

REGLAS DE TRABAJO BIM

Resumen del Estándar PlanBIM Chile aplicado a Pausa Maule · Paso 01

PDF ↗

ESPECIFICACIÓN TÉCNICA

Materiales, fichas de fabricante, categorías cerradas

PDF ↗

PEB PRELIMINAR

Plan de Ejecución BIM — etapa preliminar

PDF ↗

PEB COMPLETADO

Tabla NDI por categoría y 9 recintos (nombre, número, nivel, área, perímetro)

XLSX ↓ PDF ↗

TABLA NDI

Niveles de Desarrollo de la Información

PDF ↗

PARÁMETROS COMPARTIDOS

Grupo NDI2 — parámetros compartidos del proyecto

TXT ↓ PDF ↗

NOMENCLATURA IFC

Nombre en la vida real, clase IFC y nombre en Revit de cada entidad del modelo

XLSX ↓ PDF ↗

TABLAS DEL MODELO

Tablas de planificación exportadas desde Revit (20 hojas)

XLSX ↓

REPORTE DE CUMPLIMIENTO BEP

Verificación del modelo contra el Plan de Ejecución BIM

XLSX ↓

LÁMINAS DEL MODELO

Láminas A101 y A102 exportadas desde Revit

PDF ↗

16 PROVEEDORES VERIFICADOS

FICHAS DE PROVEEDORES

16 proveedores verificados · contacto, sitio web, ficha técnica

XLSX ↓

ELEMENTO	EMPRESA	PRODUCTO	SITIO WEB	FICHA TÉCNICA
Muro / Quincha	Corporación Protierra Chile	Sistema Quincha Liviana Húmeda	redproterra.org	FICHA TÉCNICA ↗
Cubierta	Cubiertas Nacionales	Panel Ondulado CN-1020	cubiertasnacionales.cl	FICHA TÉCNICA ↗

Radier y zapatas	Melón	Hormigón con Fibra	melon.cl	FICHA TÉCNICA ↗
Radier pulido	Sika Chile	Sikafloor-3 QuartzTop	chl.sika.com	FICHA TÉCNICA ↗
Pilar estructural	Arauco — Hilam	Madera Laminada Encolada MLE 20c	arauco.com/hilam	FICHA TÉCNICA ↗
Armazón	Arauco — MSD	Construcción Premium MSD	arauco.com	FICHA TÉCNICA ↗
Muro cortina — montante	Arauco — MSD	Pino Radiata Cepillado	arauco.com	FICHA TÉCNICA ↗
Muro cortina — panel	Arauco	Panel vacío (celosía) — ficha de referencia: MSD Revestimiento Machihembrado	arauco.com/chile	FICHA TÉCNICA ↗
Puerta	Moldupanel (Puertas Chile)	Puerta Pino Radiata Italia 80×210	puertaschile.cl	FICHA TÉCNICA ↗
Herrajes	Häfele (vía El Carpintero)	Bisagras y cerraduras	elcarpintero.cl	FICHA TÉCNICA ↗
Ventana	DMC Ventanas de Aluminio	Ventana proyectante de aluminio negro, a medida	construex.cl/dmc_ventanas_de_aluminio	FICHA TÉCNICA ↗
Sanitarios	Fanaloza	New Valencia a Muro / Lavamanos Ciro	fanaloza.cl	FICHA TÉCNICA ↗
Bebedero	FAMAVA	Bebedero de agua BAG-40 (acero inoxidable)	famava.cl	FICHA TÉCNICA ↗
Lavaplatos	Fanaloza	Lavaplatos de sobreponer con escurridor 80×50	fanaloza.cl	FICHA TÉCNICA ↗
Bicicletero	Rabke	Bicicletero U invertida TB170	rabke.cl	FICHA TÉCNICA ↗
Banca	Fabricación local a pedido	Banca de acero galvanizado y madera, 2500 × 400 × 450 mm	—	—
Abastecimiento local	Sodimac / Construmart Talca	Distribución general	sodimac.cl construmart.cl	—

Referentes, proveedores, documentos técnicos, láminas e imágenes — no incluye el modelo Revit ni el IFC (ver punto 08).

↓ DESCARGAR (.ZIP, 44 MB)

HAB_ARQ_MODELO_R01.RVT

ELEMENTOS TOTALES	TIPOS	FAMILIAS	CATEGORÍAS	VISTAS	NIVELES PRINCIPALES + SUBNIVELES

CARGAR VISOR 3D

Se descarga el IFC4x3 (4,5 MB) y se muestra en el navegador. Arrastra para girar, usa la rueda para acercar y mantén presionada la rueda (botón central) para desplazar la vista, como en Revit.

Cantidades obtenidas del modelo Revit.

Haz clic en una fila para verla en el visor 3D.

CATEGORÍA	TIPO	CANT.	MEDIDA
Muros	MURO_EXT_QUINCHA_12cm	11	57,14 m^2 · 6,86 m^3
Muros cortina	M.CORTINA_EXT_CELOSIA_PINO RADIATA (FIX N)	6	37,29 m^2
Montantes de muro cortina	12.5x100mm_PINO RADIATA	396	250,2 m · 0,63 m^3
Paneles de muro cortina	Empty (celosía)	192	31,04 m^2
Puertas	80x210cm	2	—
Pilares estructurales	130X130	16	0,65 m^3
Armazón principal	2"X8" Sin cepillar	16	71,4 m · 0,70 m^3
Armazón secundario	2"X4" Cepillada	16	48,0 m · 0,24 m^3
Fundaciones aisladas	FUNDACIÓN AISLADA_HA_60x60x50cm	16	3,03 m^3
Radier estructural	RADIER_INT_HA_15cm	1	76,56 m^2 · 11,49 m^3
Pavimento pulido	PAV_INT_HORMIGON PULIDO_2cm	1	76,26 m^2 · 1,53 m^3
Cubierta (4 faldones)	CUBIERTA_ZINC ONDULADO_18mm	4	76,53 m^2 · 1,38 m^3

Inodoros	41x69cm	2	0,07 m^3
Lavamanos	53x41cm	2	0,02 m^3
Bebederos	31x32cm	3	0,05 m^3
Lavaplatos	80x60cm	1	0,04 m^3
Muebles base de cocina	104x64cm	2	0,09 m^3
Bancas	250x50cm	5	1,60 m^3
Bicicleteros	2 bicicletas	5	0,01 m^3
Recintos	9 recintos	9	79,45 m^2

DESCARGAR EXCEL (.XLSX) ↓ DESCARGAR CSV ↓

HAB_ARQ_MODELO_R01.RVT

Modelo BIM del habitáculo Pausa Maule · 233 MB

DESCARGAR ↗

HAB_ARQ_MODELO_R01_IFC4X3.IFC

Export IFC4X3_ADD2 · MVD CoordinationView · 4,5 MB

DESCARGAR ↗