




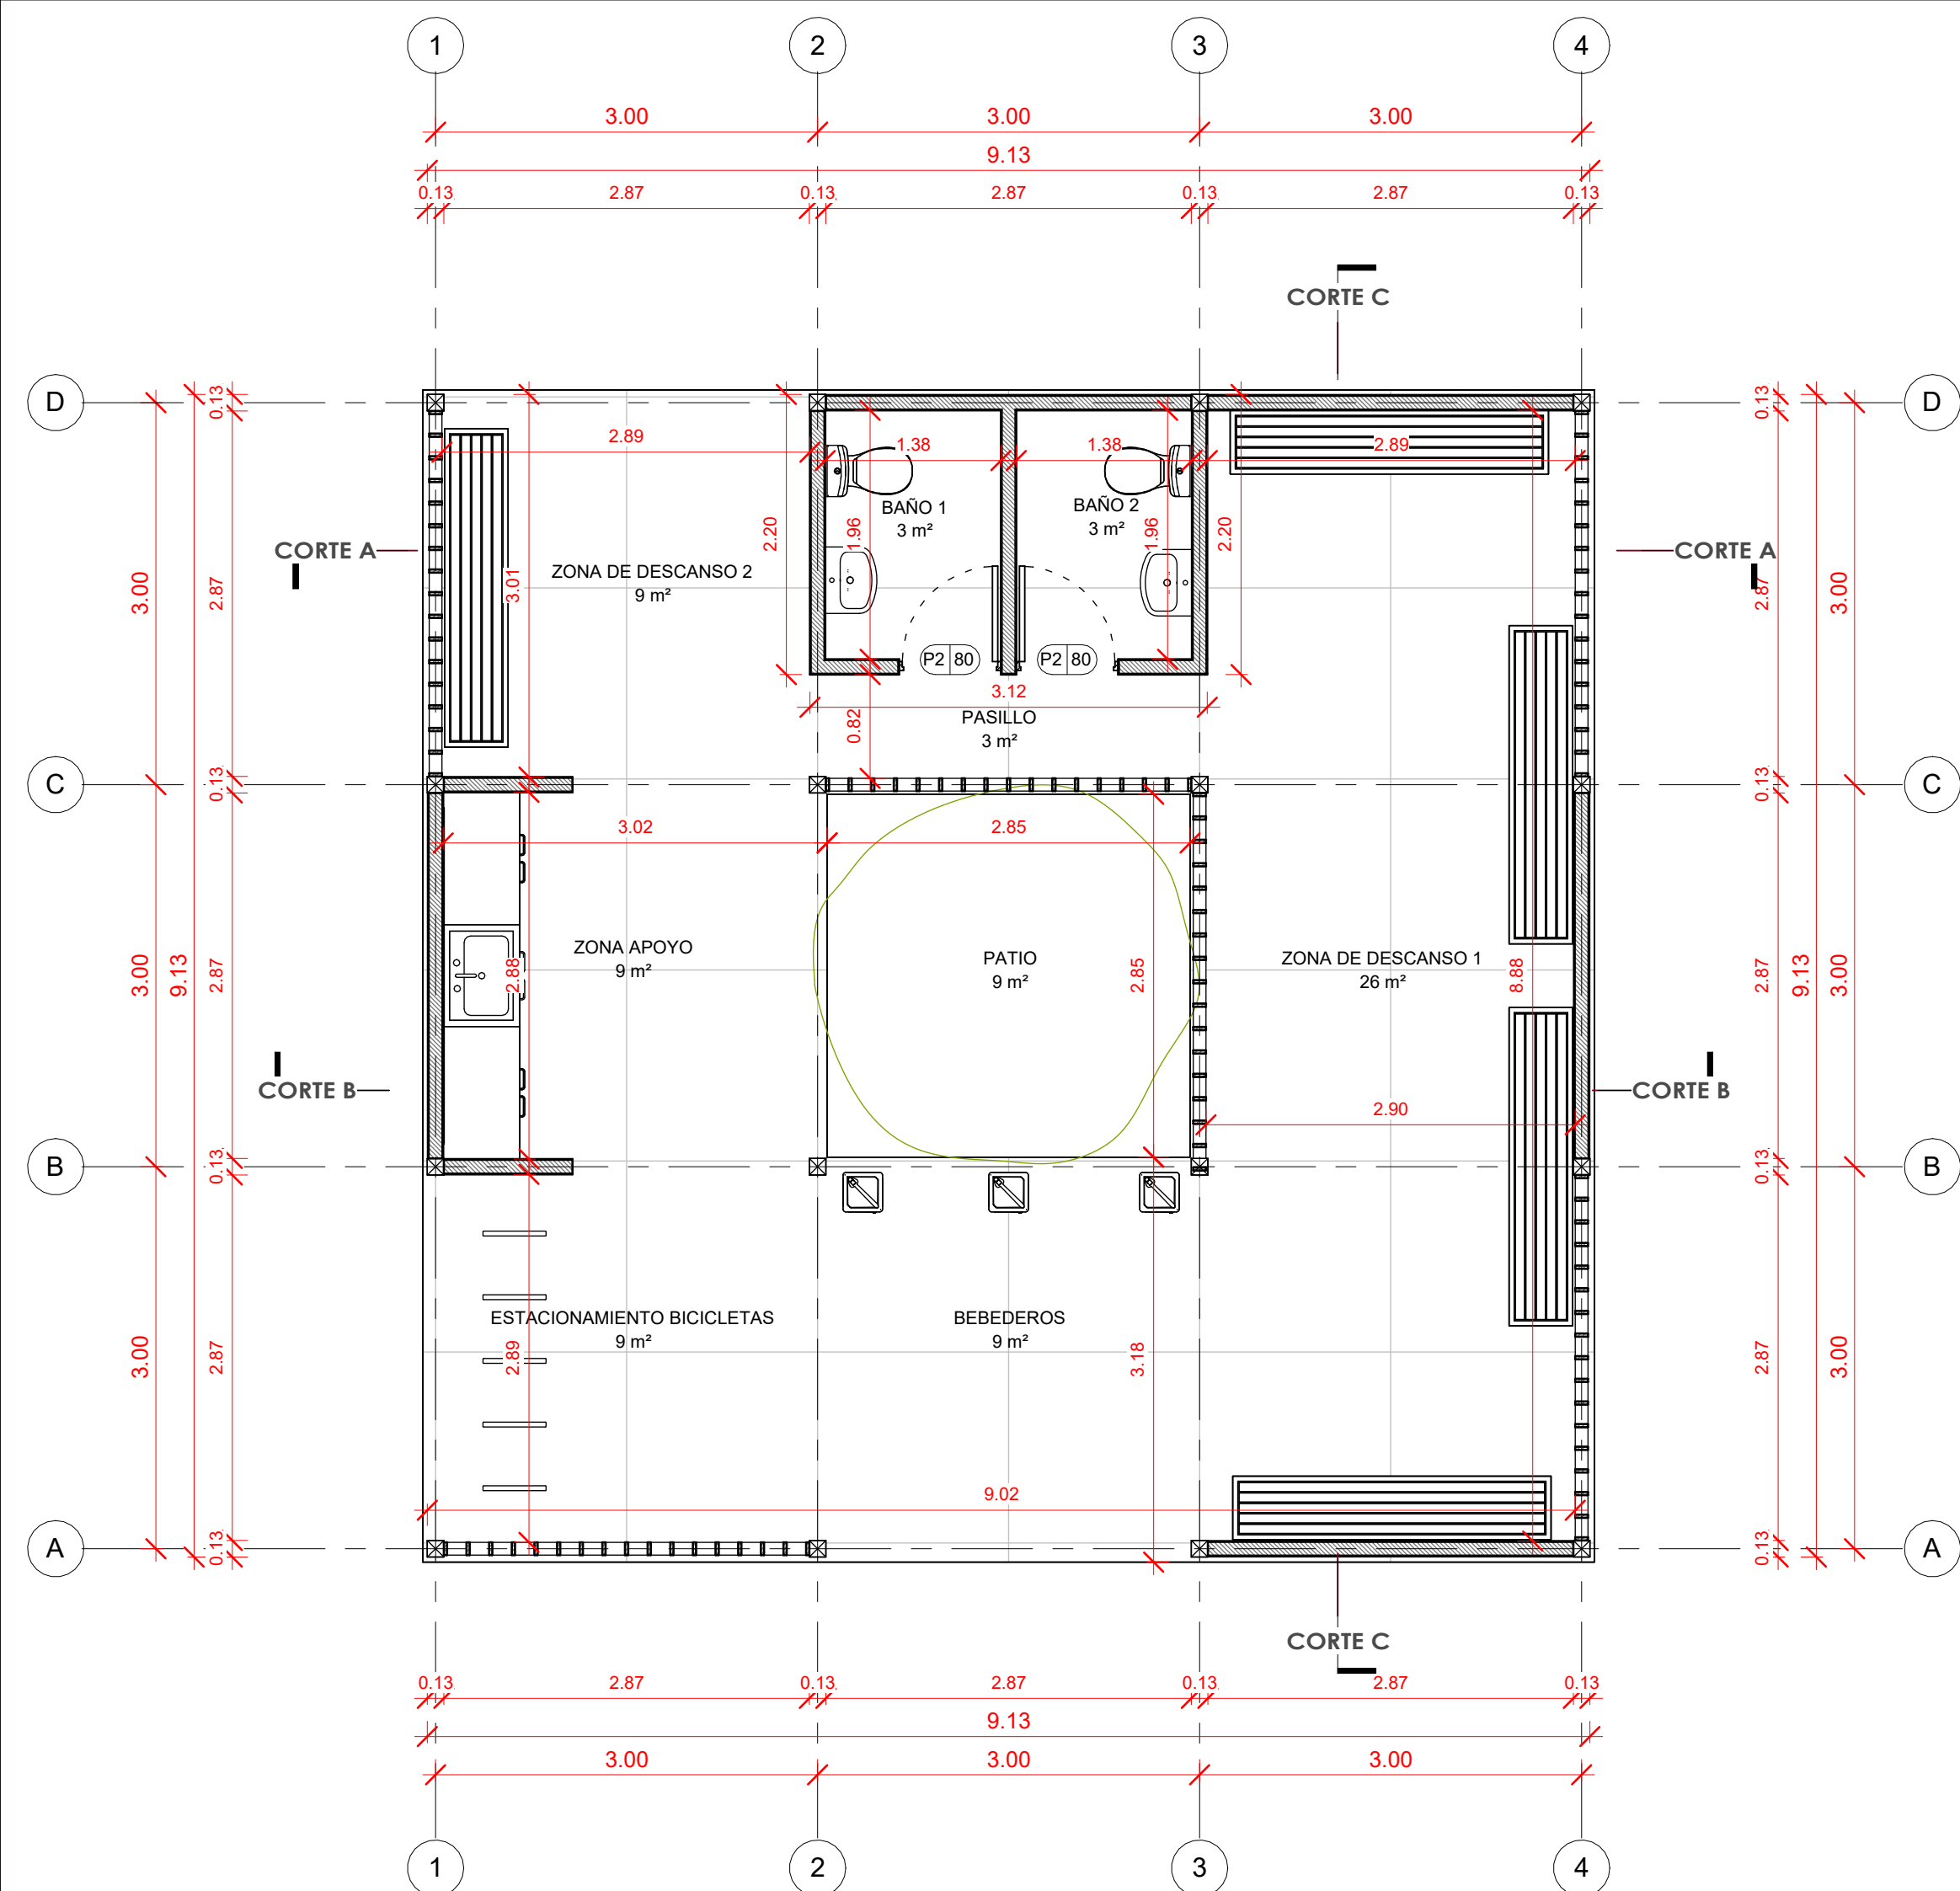


1 PLANTA DE ARQUITECTURA
1:50

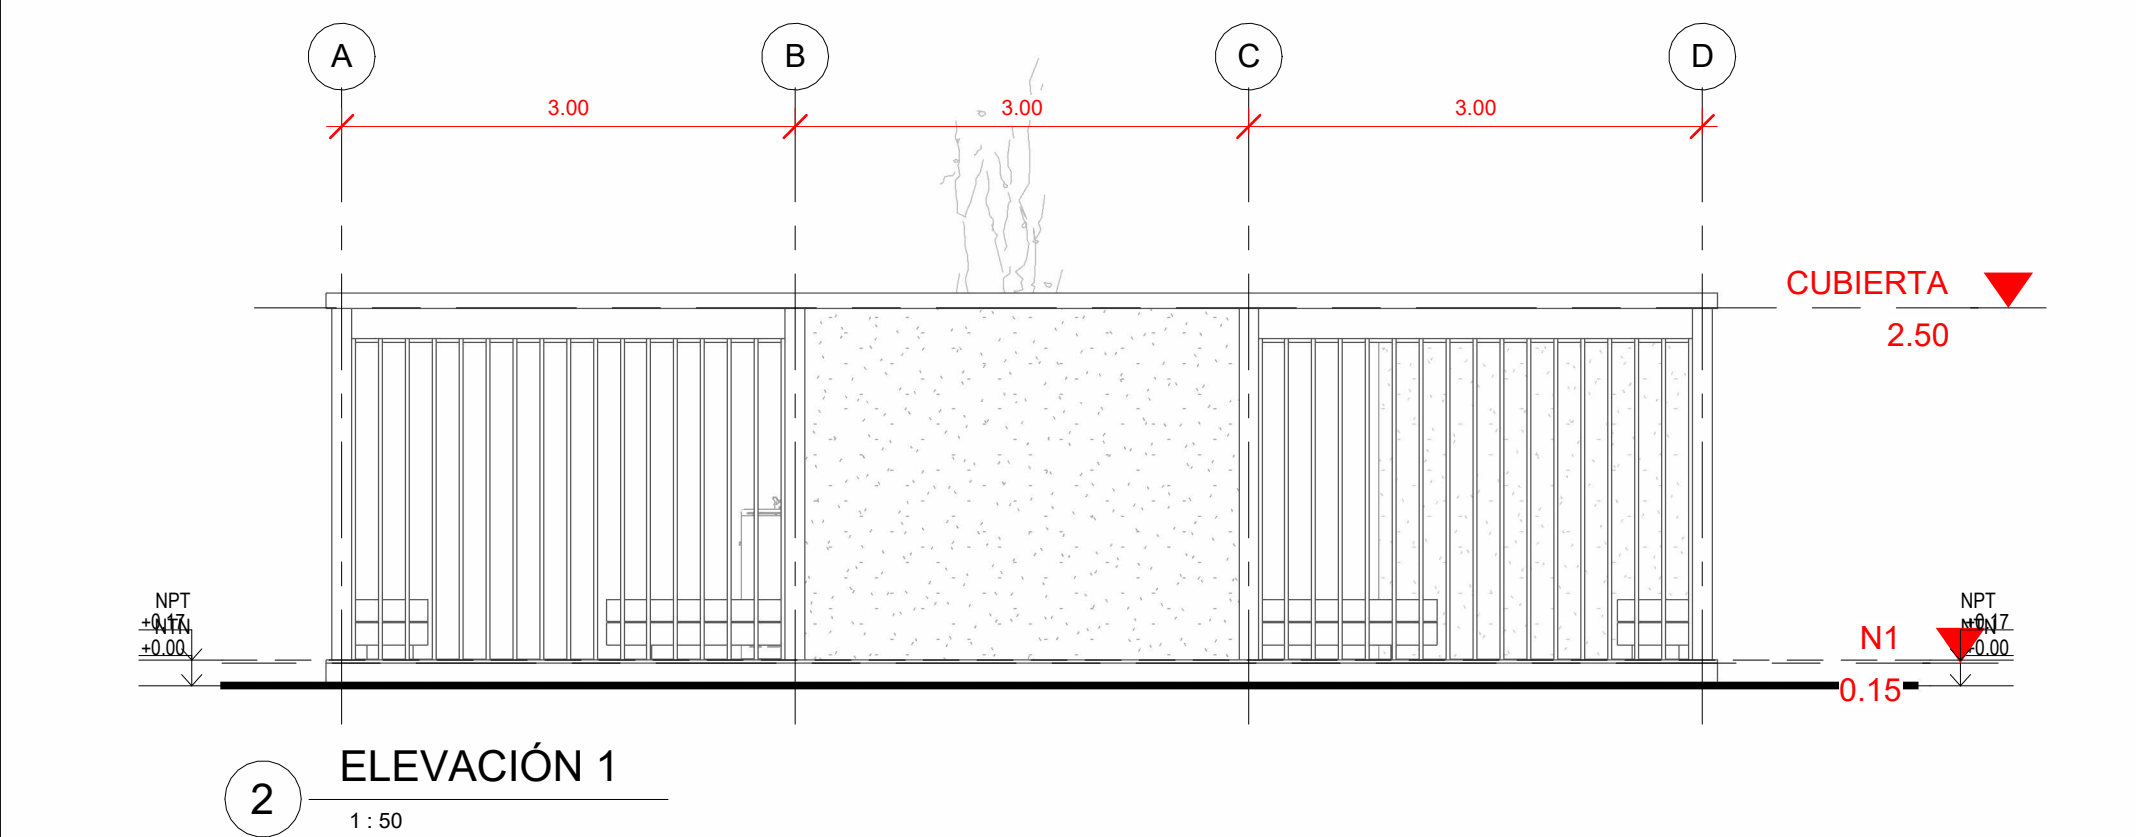


2 ELEVACIÓN 1
1:50

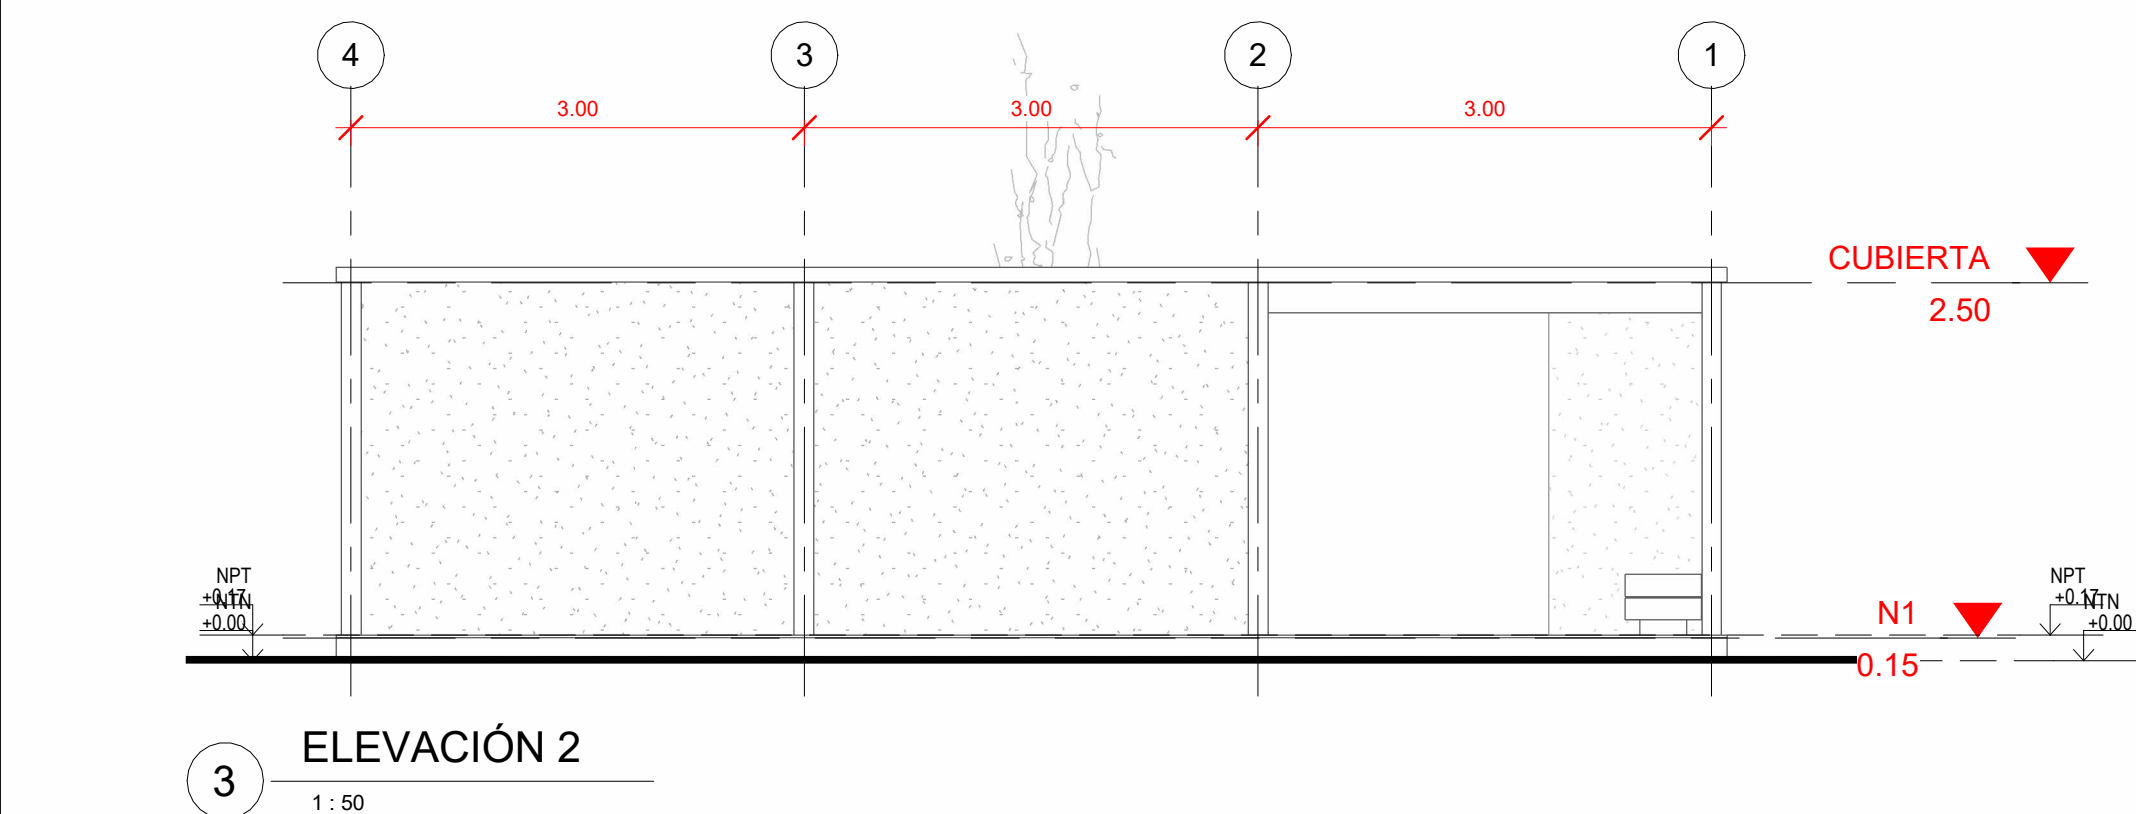


3 ELEVACIÓN 2
1:50

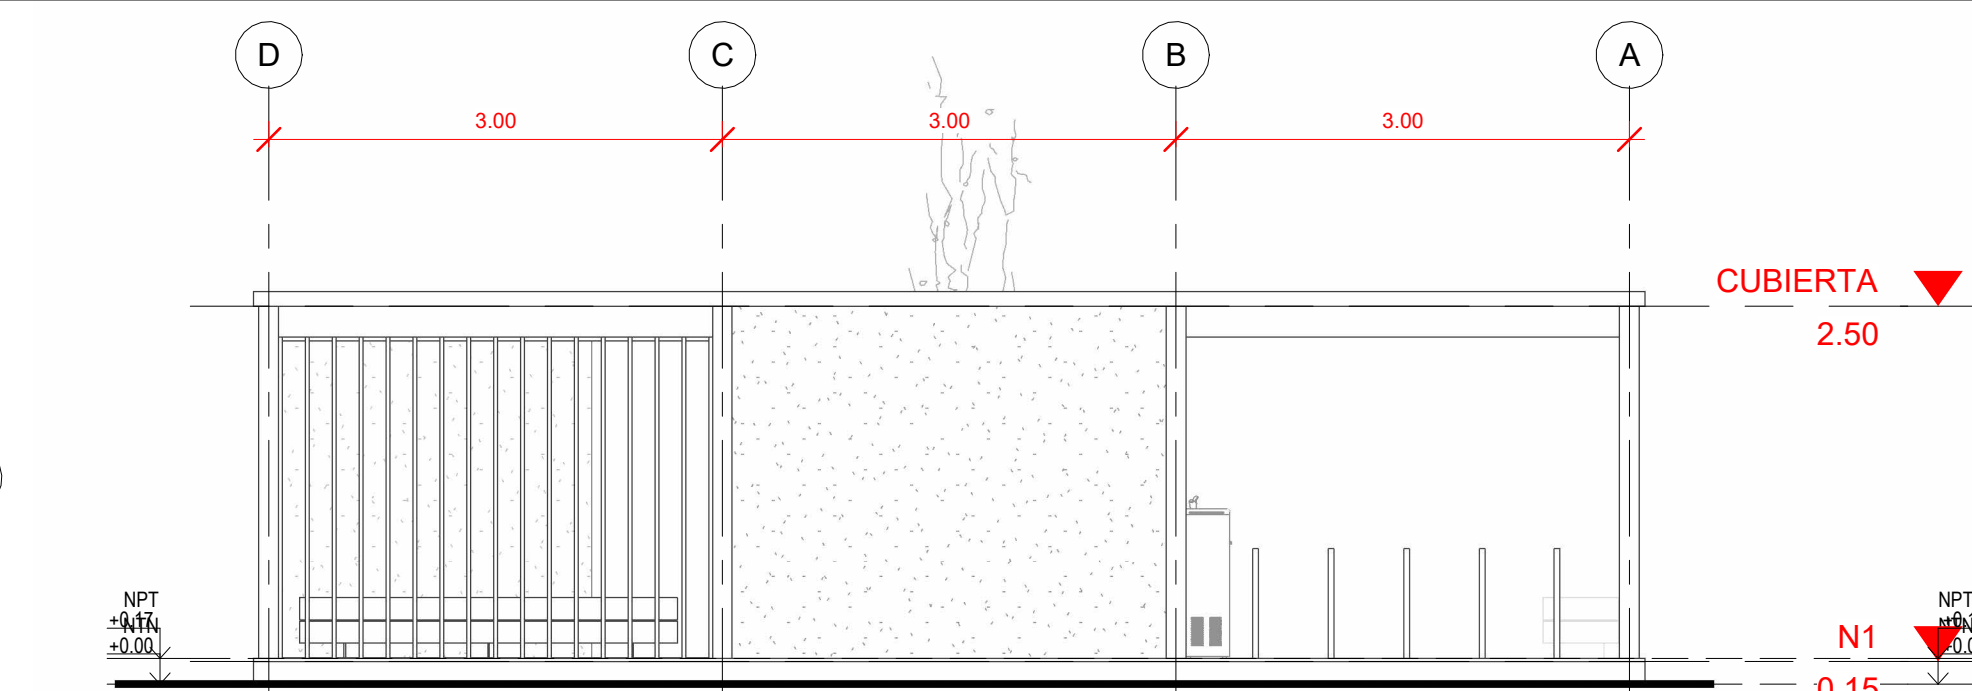


4 ELEVACIÓN 3
1:50

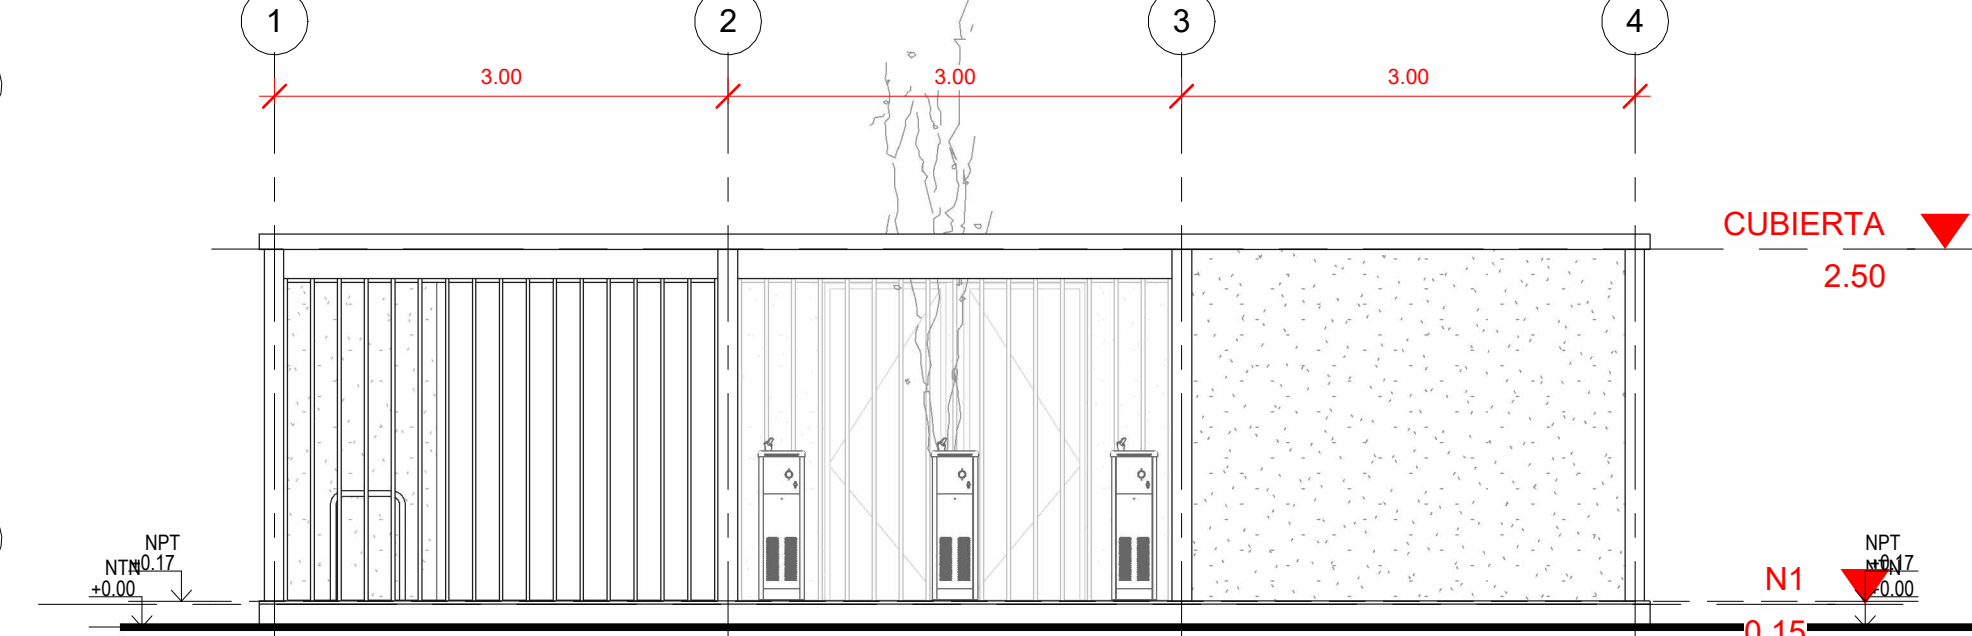


5 ELEVACIÓN 4
1:50

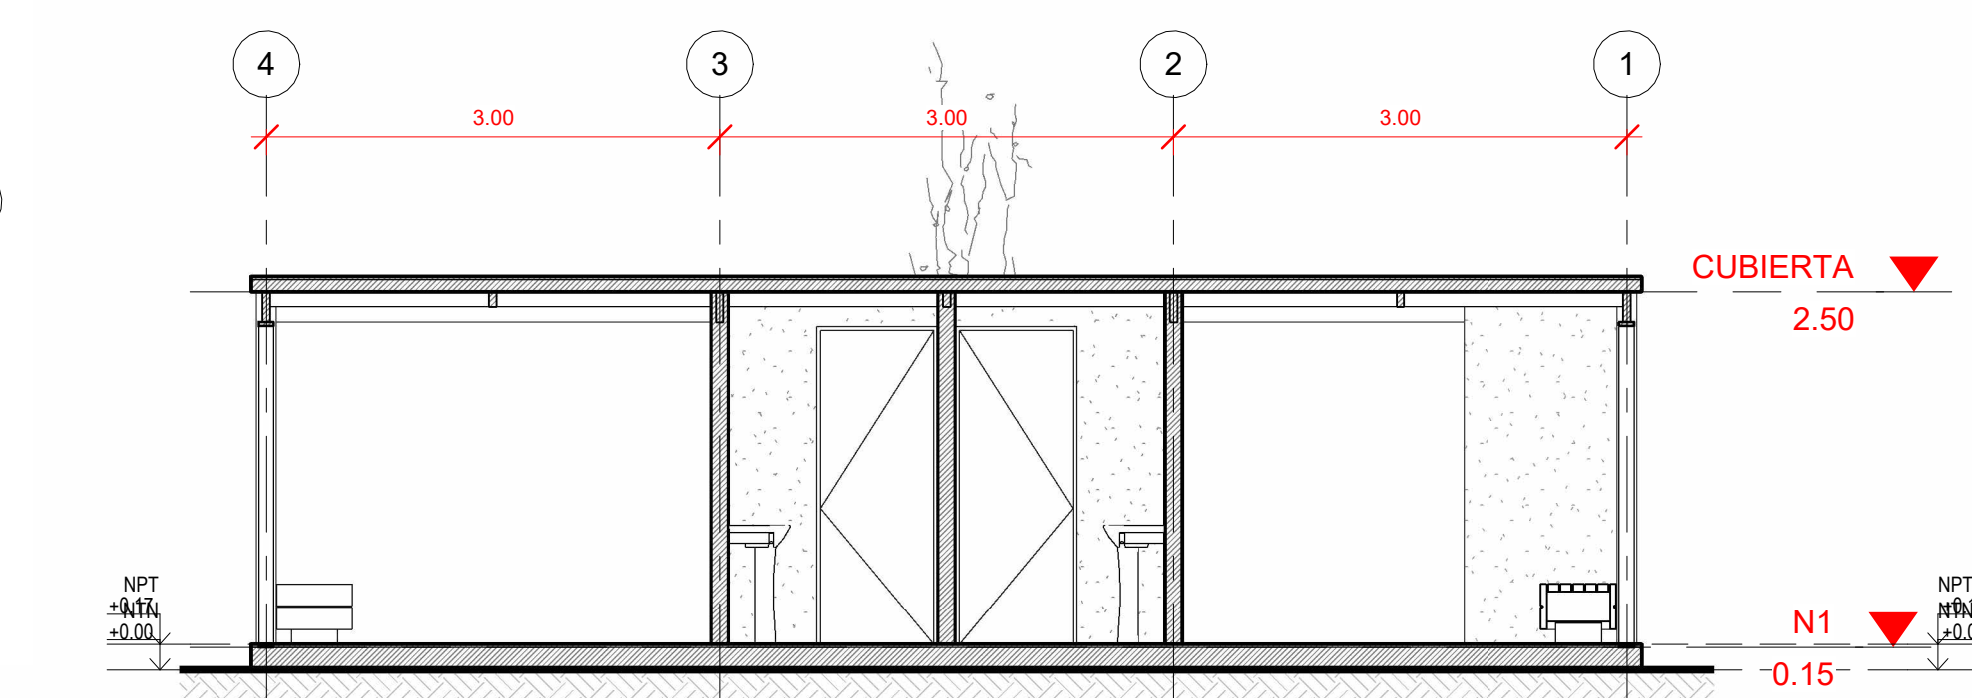


6 CORTE A
1:50

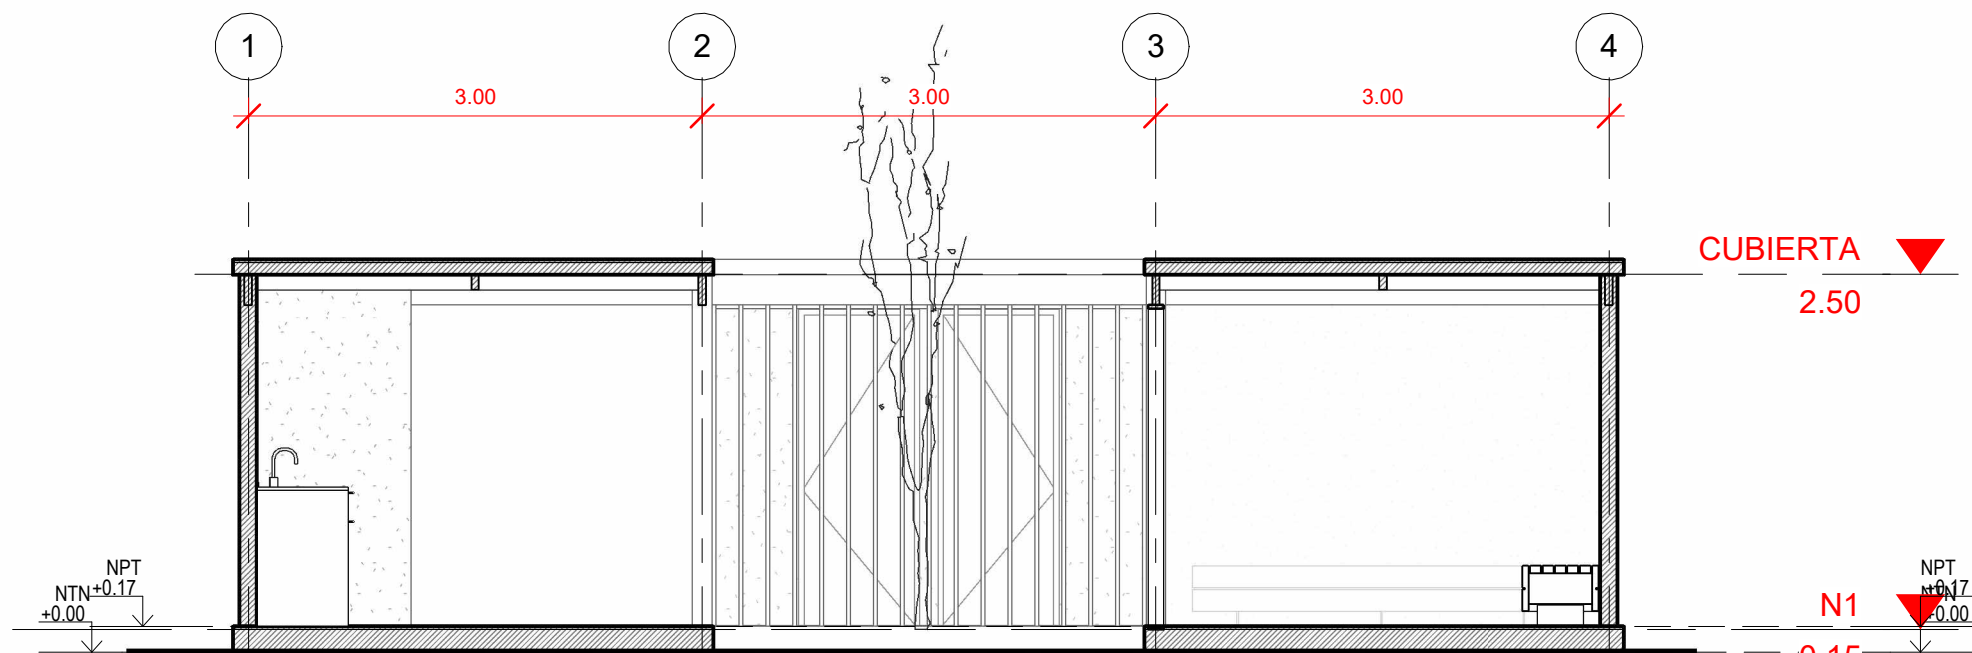


9 CORTE B
1:50

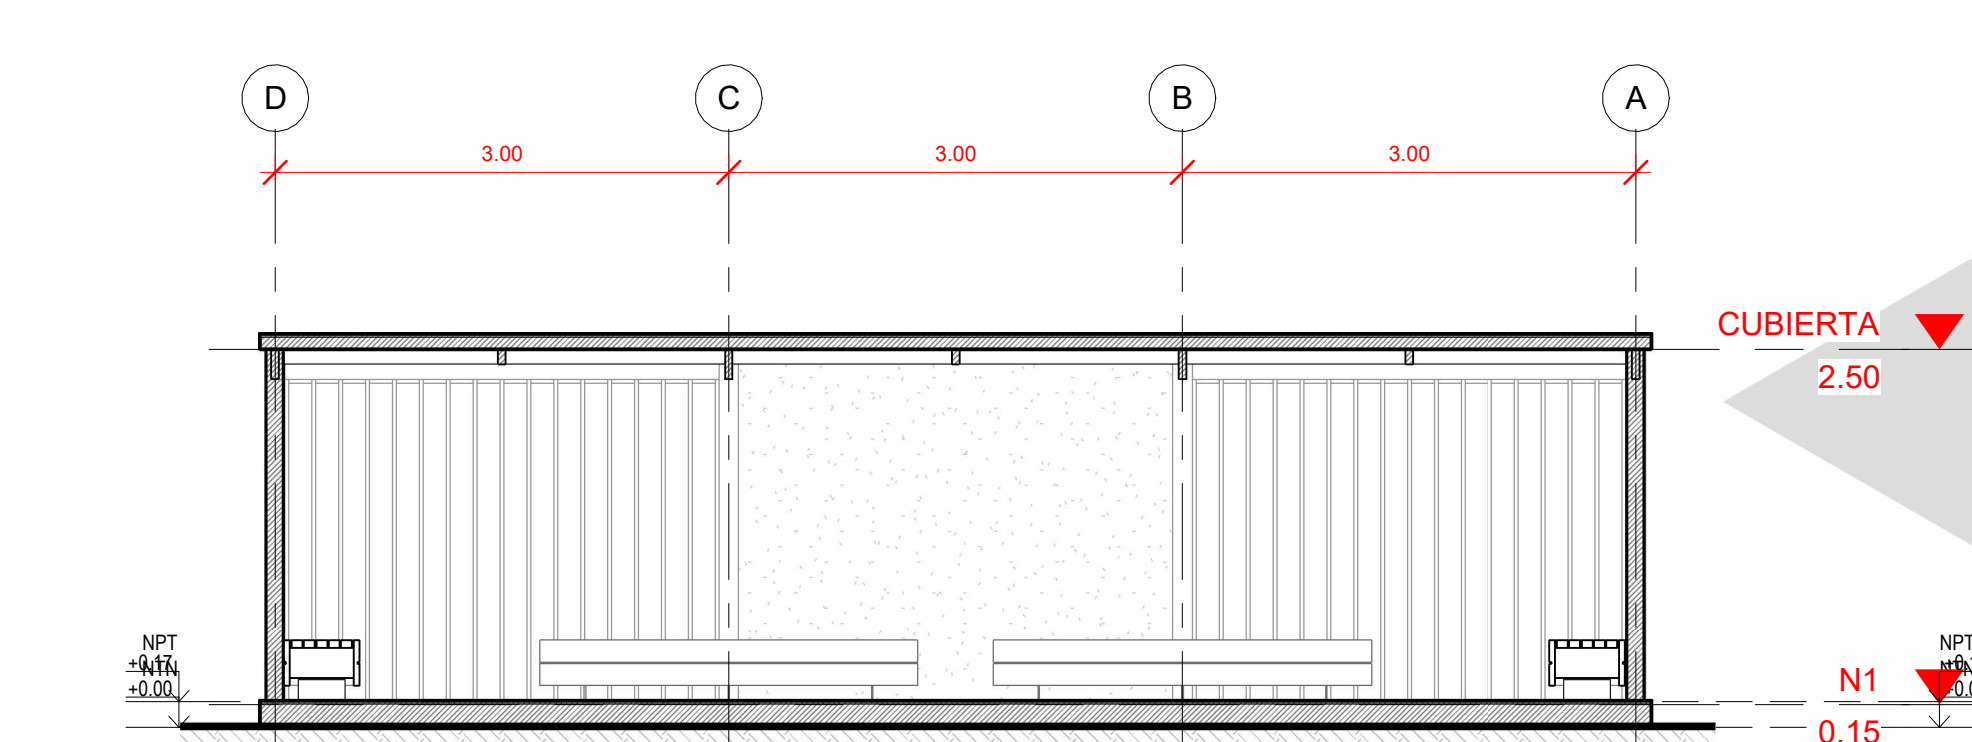

8 CORTE C
1:50

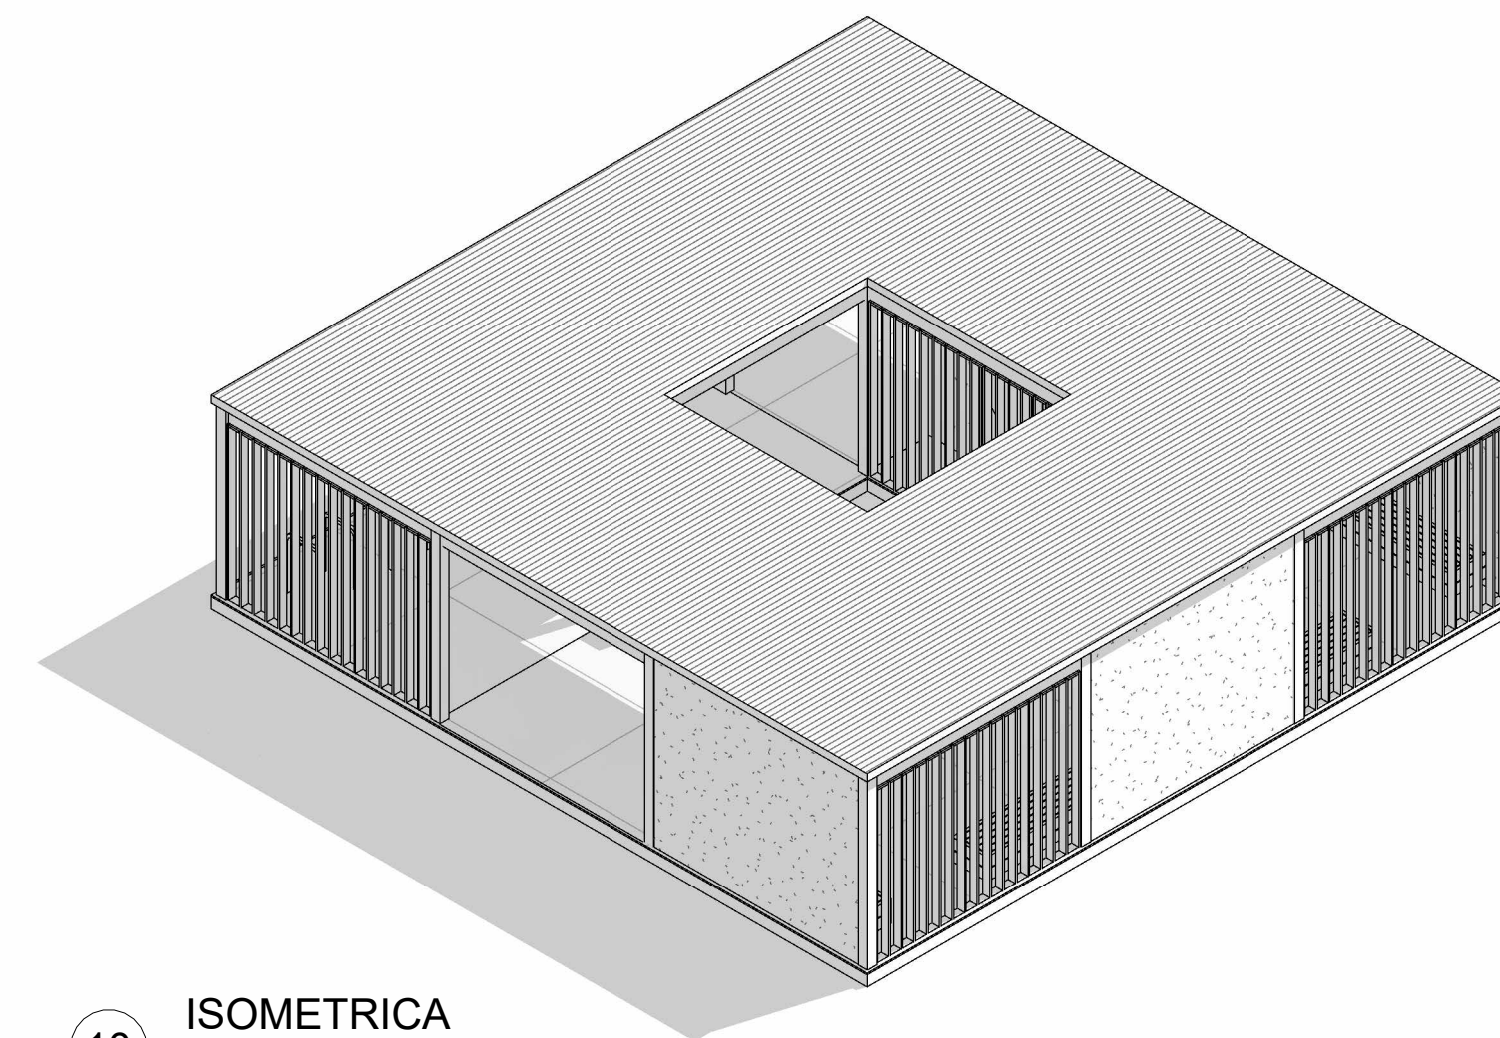

10 ISOMETRICA

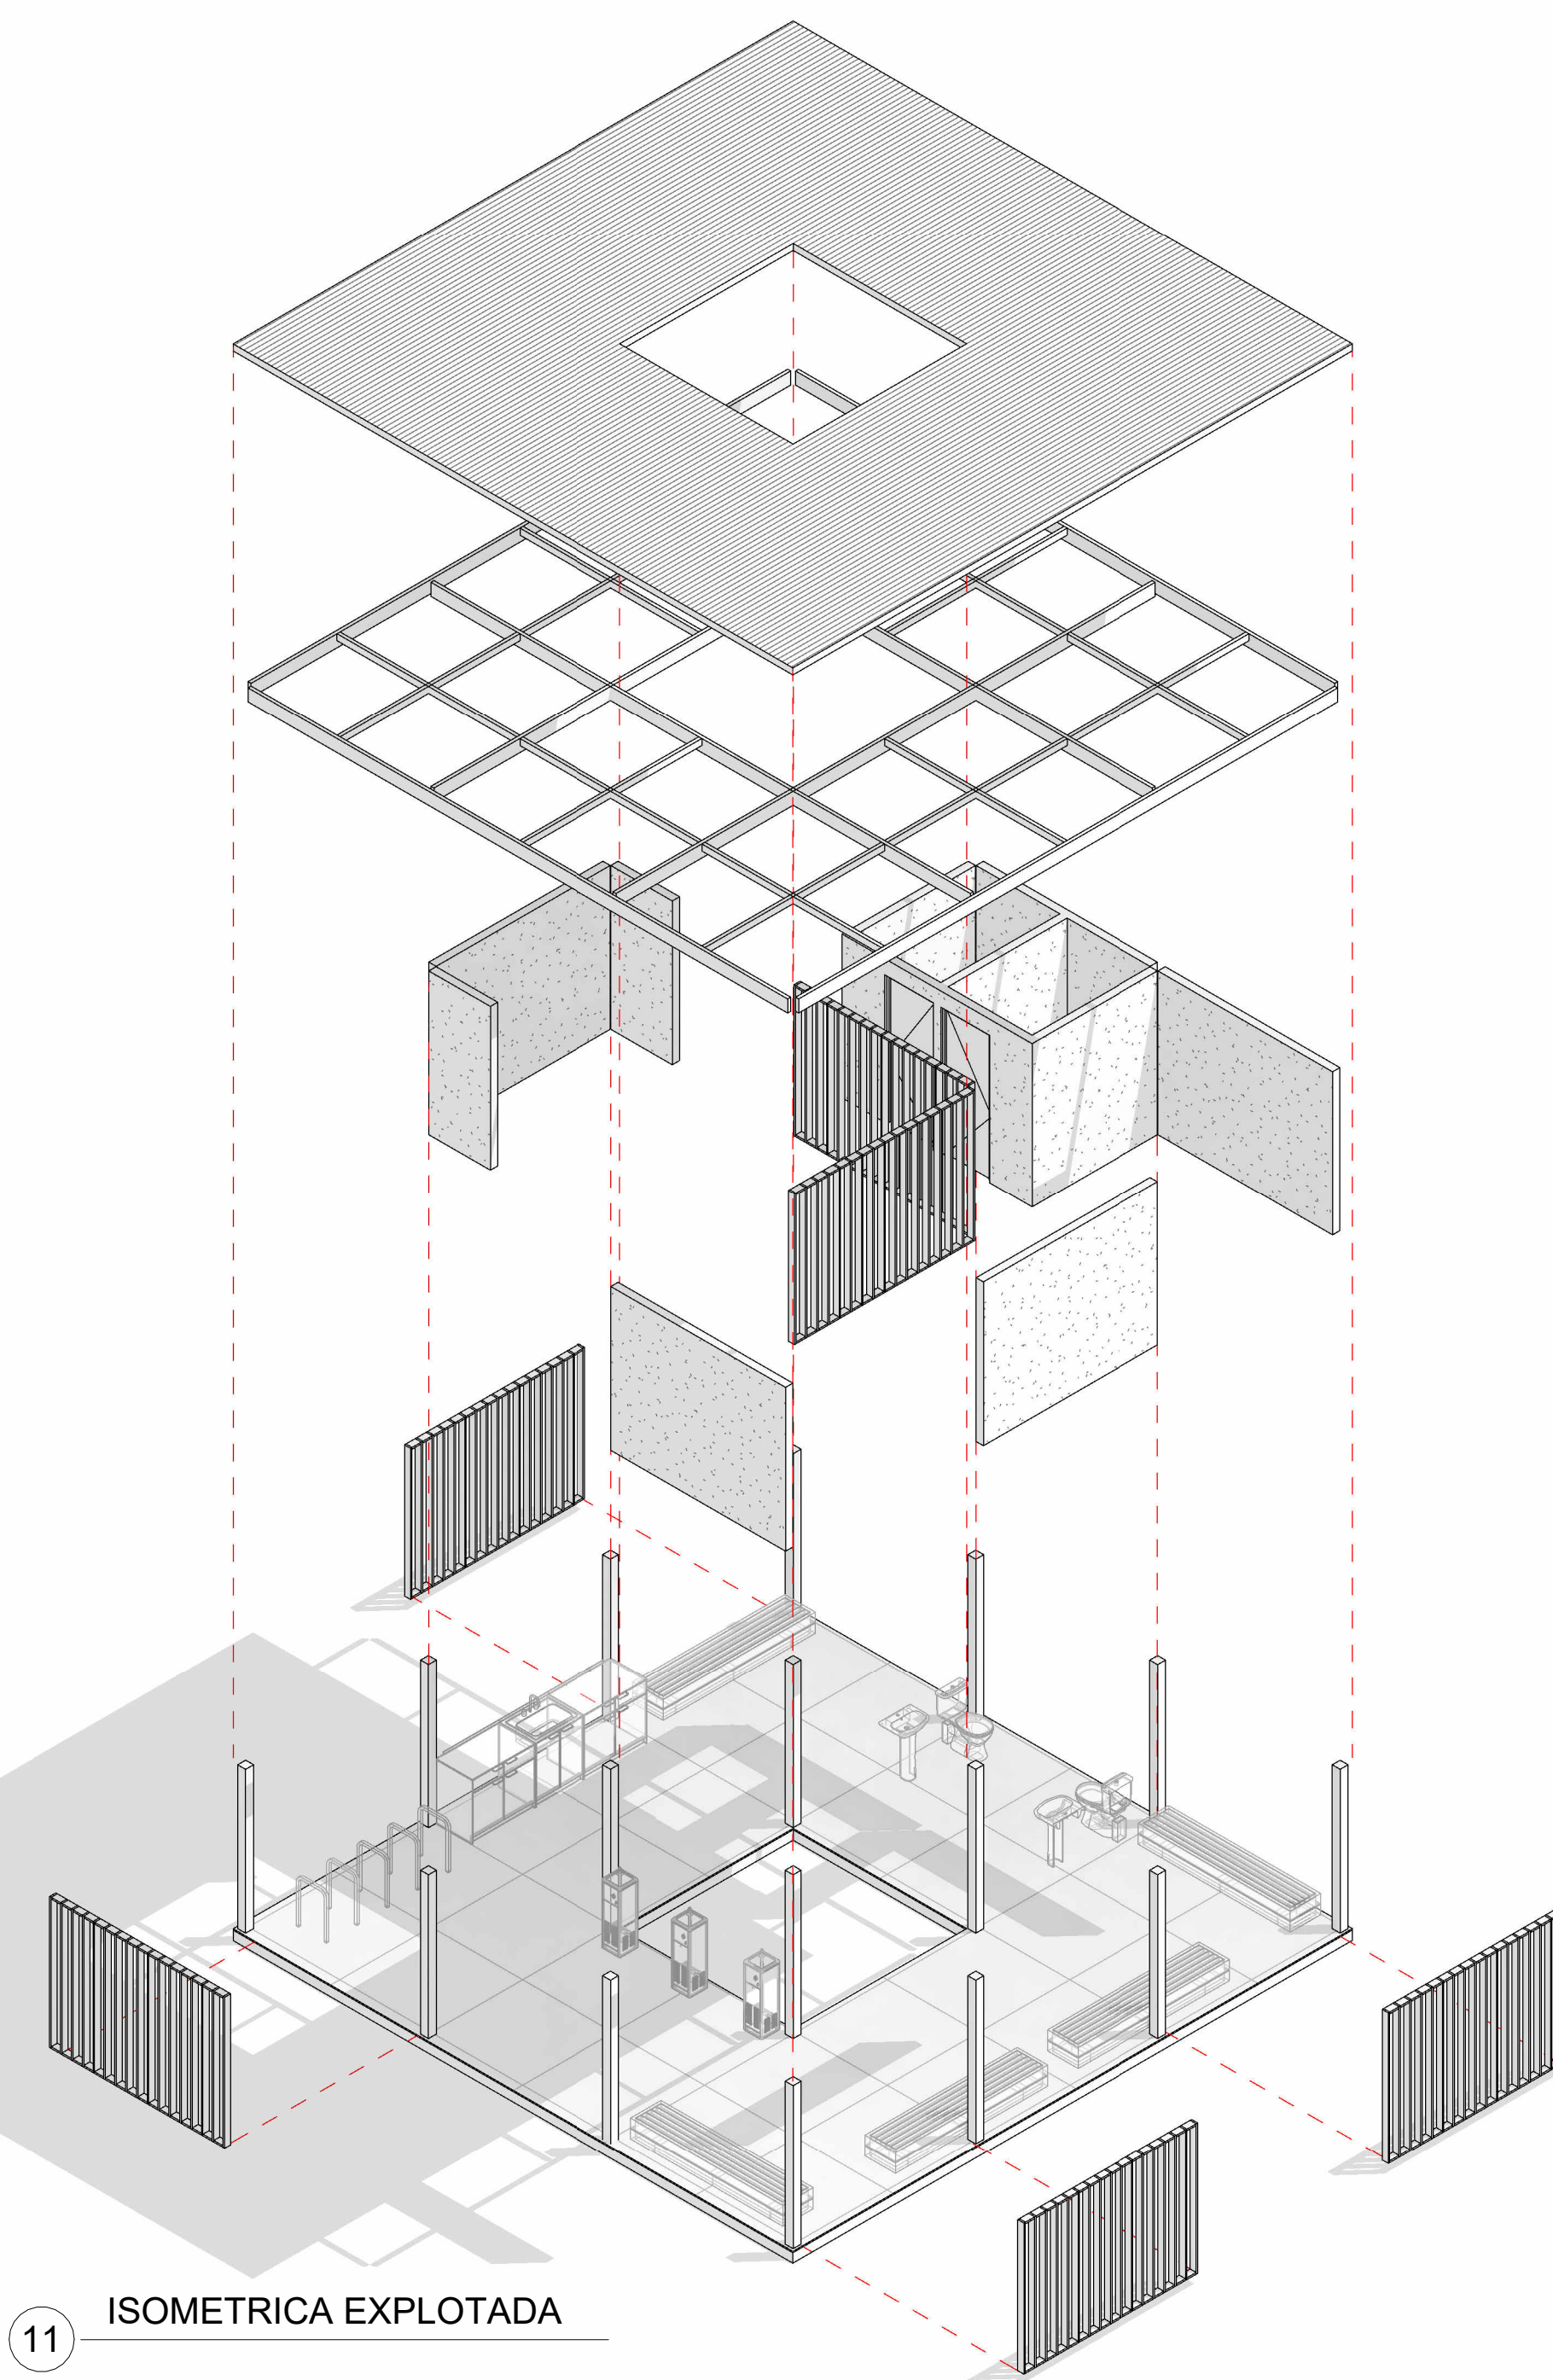

11 ISOMETRICA EXPLOTADA